

DRAWING INDEX	
GENERAL DRAWINGS	
XC-001	COVER SHEET AND DRAWING INDEX
PLAN DRAWINGS	
XC-A101	EAST BOWL PLAN
XC-D101	360 PLAN VIEW
ELEVATIONS	
XC-A201	EAST BOWL WEST ELEVATION
DETAILS	
XC-A501	EAST BOWL - SECTION & DETAILS @ CANOPY ROOF
XC-A502	EAST BOWL - WING WALL PLAN DETAILS
XC-A503	EAST BOWL - WING WALL ZEPP DETAILS
XC-A504	EAST BOWL - TYP ZEPP DETAILS
XC-A505	EAST BOWL - BACK KNIFE EDGE DETAIL
XC-A506	EAST BOWL - ANCHOR DETAILS
XC-D501	360 - TYPICAL CANOPY CROSS SECTION & DETAILS
XC-D502	360 - CANOPY CROSS SECTION AT WALKING PATH


miispel


CITY OF SCOTTSDALE CIVIC CENTER PLAZA

RITOCH-POWELL
RPA & Associates
602-263-1177
WWW.RPAENG.COM

LAKE | FLATO
© 2021 Lake|Flato Architects, Inc.
311 THIRD STREET
SAN ANTONIO, TEXAS 78205
P 210.227.3335 F 210.224.9515
www.lakeflato.com

ZAHNER
ARCHITECTURAL METAL
1400 EAST NINTH STREET
KANSAS CITY, MO 64106
TEL: (816) 474-8882
FAX: (816) 474-7994
WWW.AZAHNER.COM

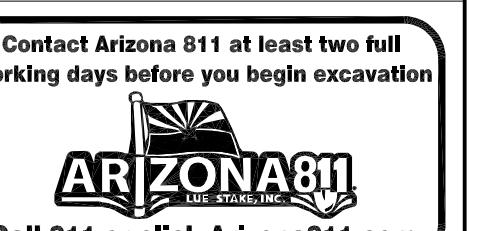SET ISSUE DATES				
DATE	ISSUE			
01/20/22 100% DRAWINGS				
<hr/> <hr/> <hr/>				
REVISIONS				
NO.	DATE	DESCRIPTION		
<hr/> <hr/> <hr/>				
Contact Arizona 811 at least two full working days before you begin excavation				
 Call 811 or click Arizona811.com				
DATE: 01/20/2022		REVISION:		
BY:				
		PUBLIC WORKS		
		CAPITAL PROJECT MANAGEMENT		
		7447 E. INDIAN SCHOOL RD. SCOTTSDALE, ARIZONA 85251		
SHEET TITLE				
COVER SHEET AND DRAWING INDEX				
PROJECT TITLE				
CITY OF SCOTTSDALE CIVIC CENTER PLAZA				
THIS SHEET SCALED FOR 24X36" BORDER	SCALE	DESIGNED	BID NO.	XC-001
	DRAWN DS	AS-BUILT	COS PROJECT NO. DG04	

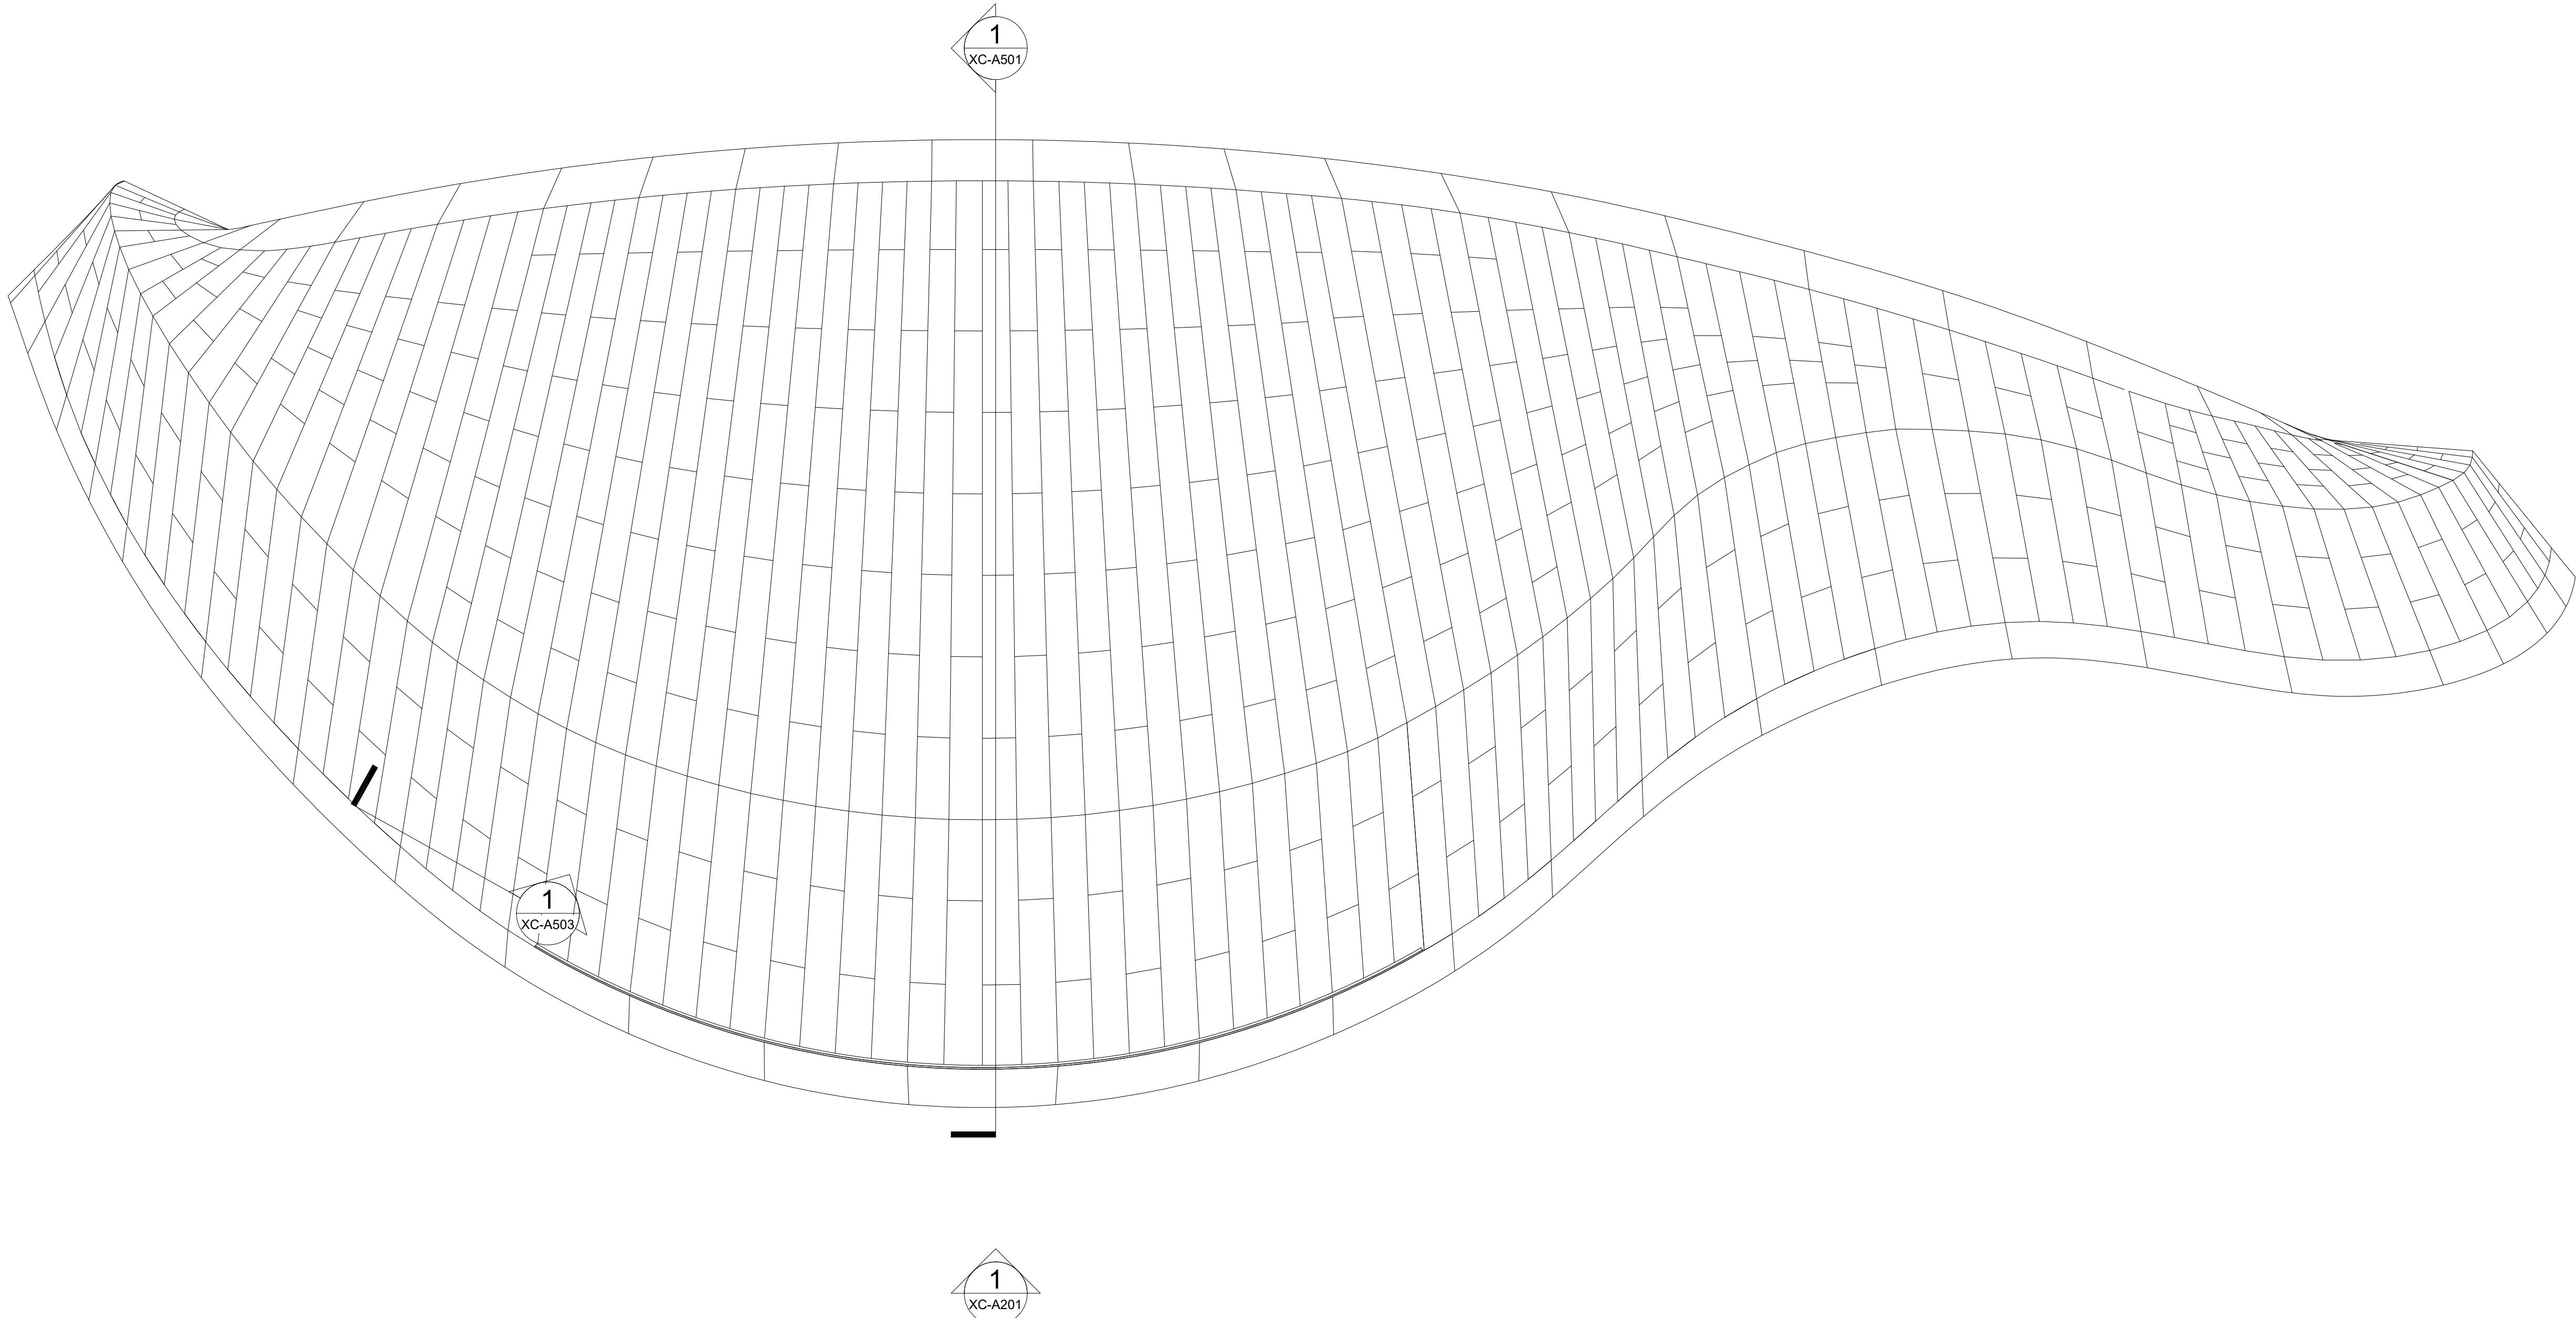


EAST BOWL PLAN VIEW

SCALE: 3/16" = 1'-0"

ZAHNER REF: N/A
ARCH REF: N/A

SET ISSUE DATES		
DATE	ISSUE	
01/20/22 100% DRAWINGS		

REVISIONS		
NO.	DATE	DESCRIPTION

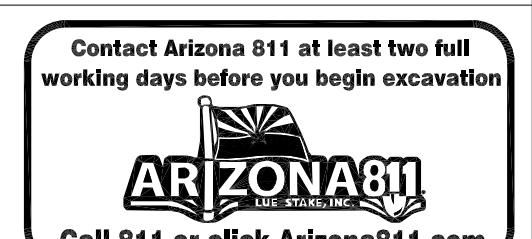


DATE: 01/20/2022		REVISION:	BY:
ENGINEER		PUBLIC WORKS	
		CAPITAL PROJECT MANAGEMENT	
		7447 E. INDIAN SCHOOL RD., SCOTTSDALE, ARIZONA 85251	
SHEET TITLE			

EAST BOWL PLAN

PROJECT TITLE		CITY OF SCOTTSDALE CIVIC CENTER PLAZA	
---------------	--	--	--

THIS SHEET SCALED FOR 24X36" BORDER	SCALE	DESIGNED	BID NO.	XC-A101
	DRAWN DS	AS-BUILT	COS PROJECT NO. DG04	

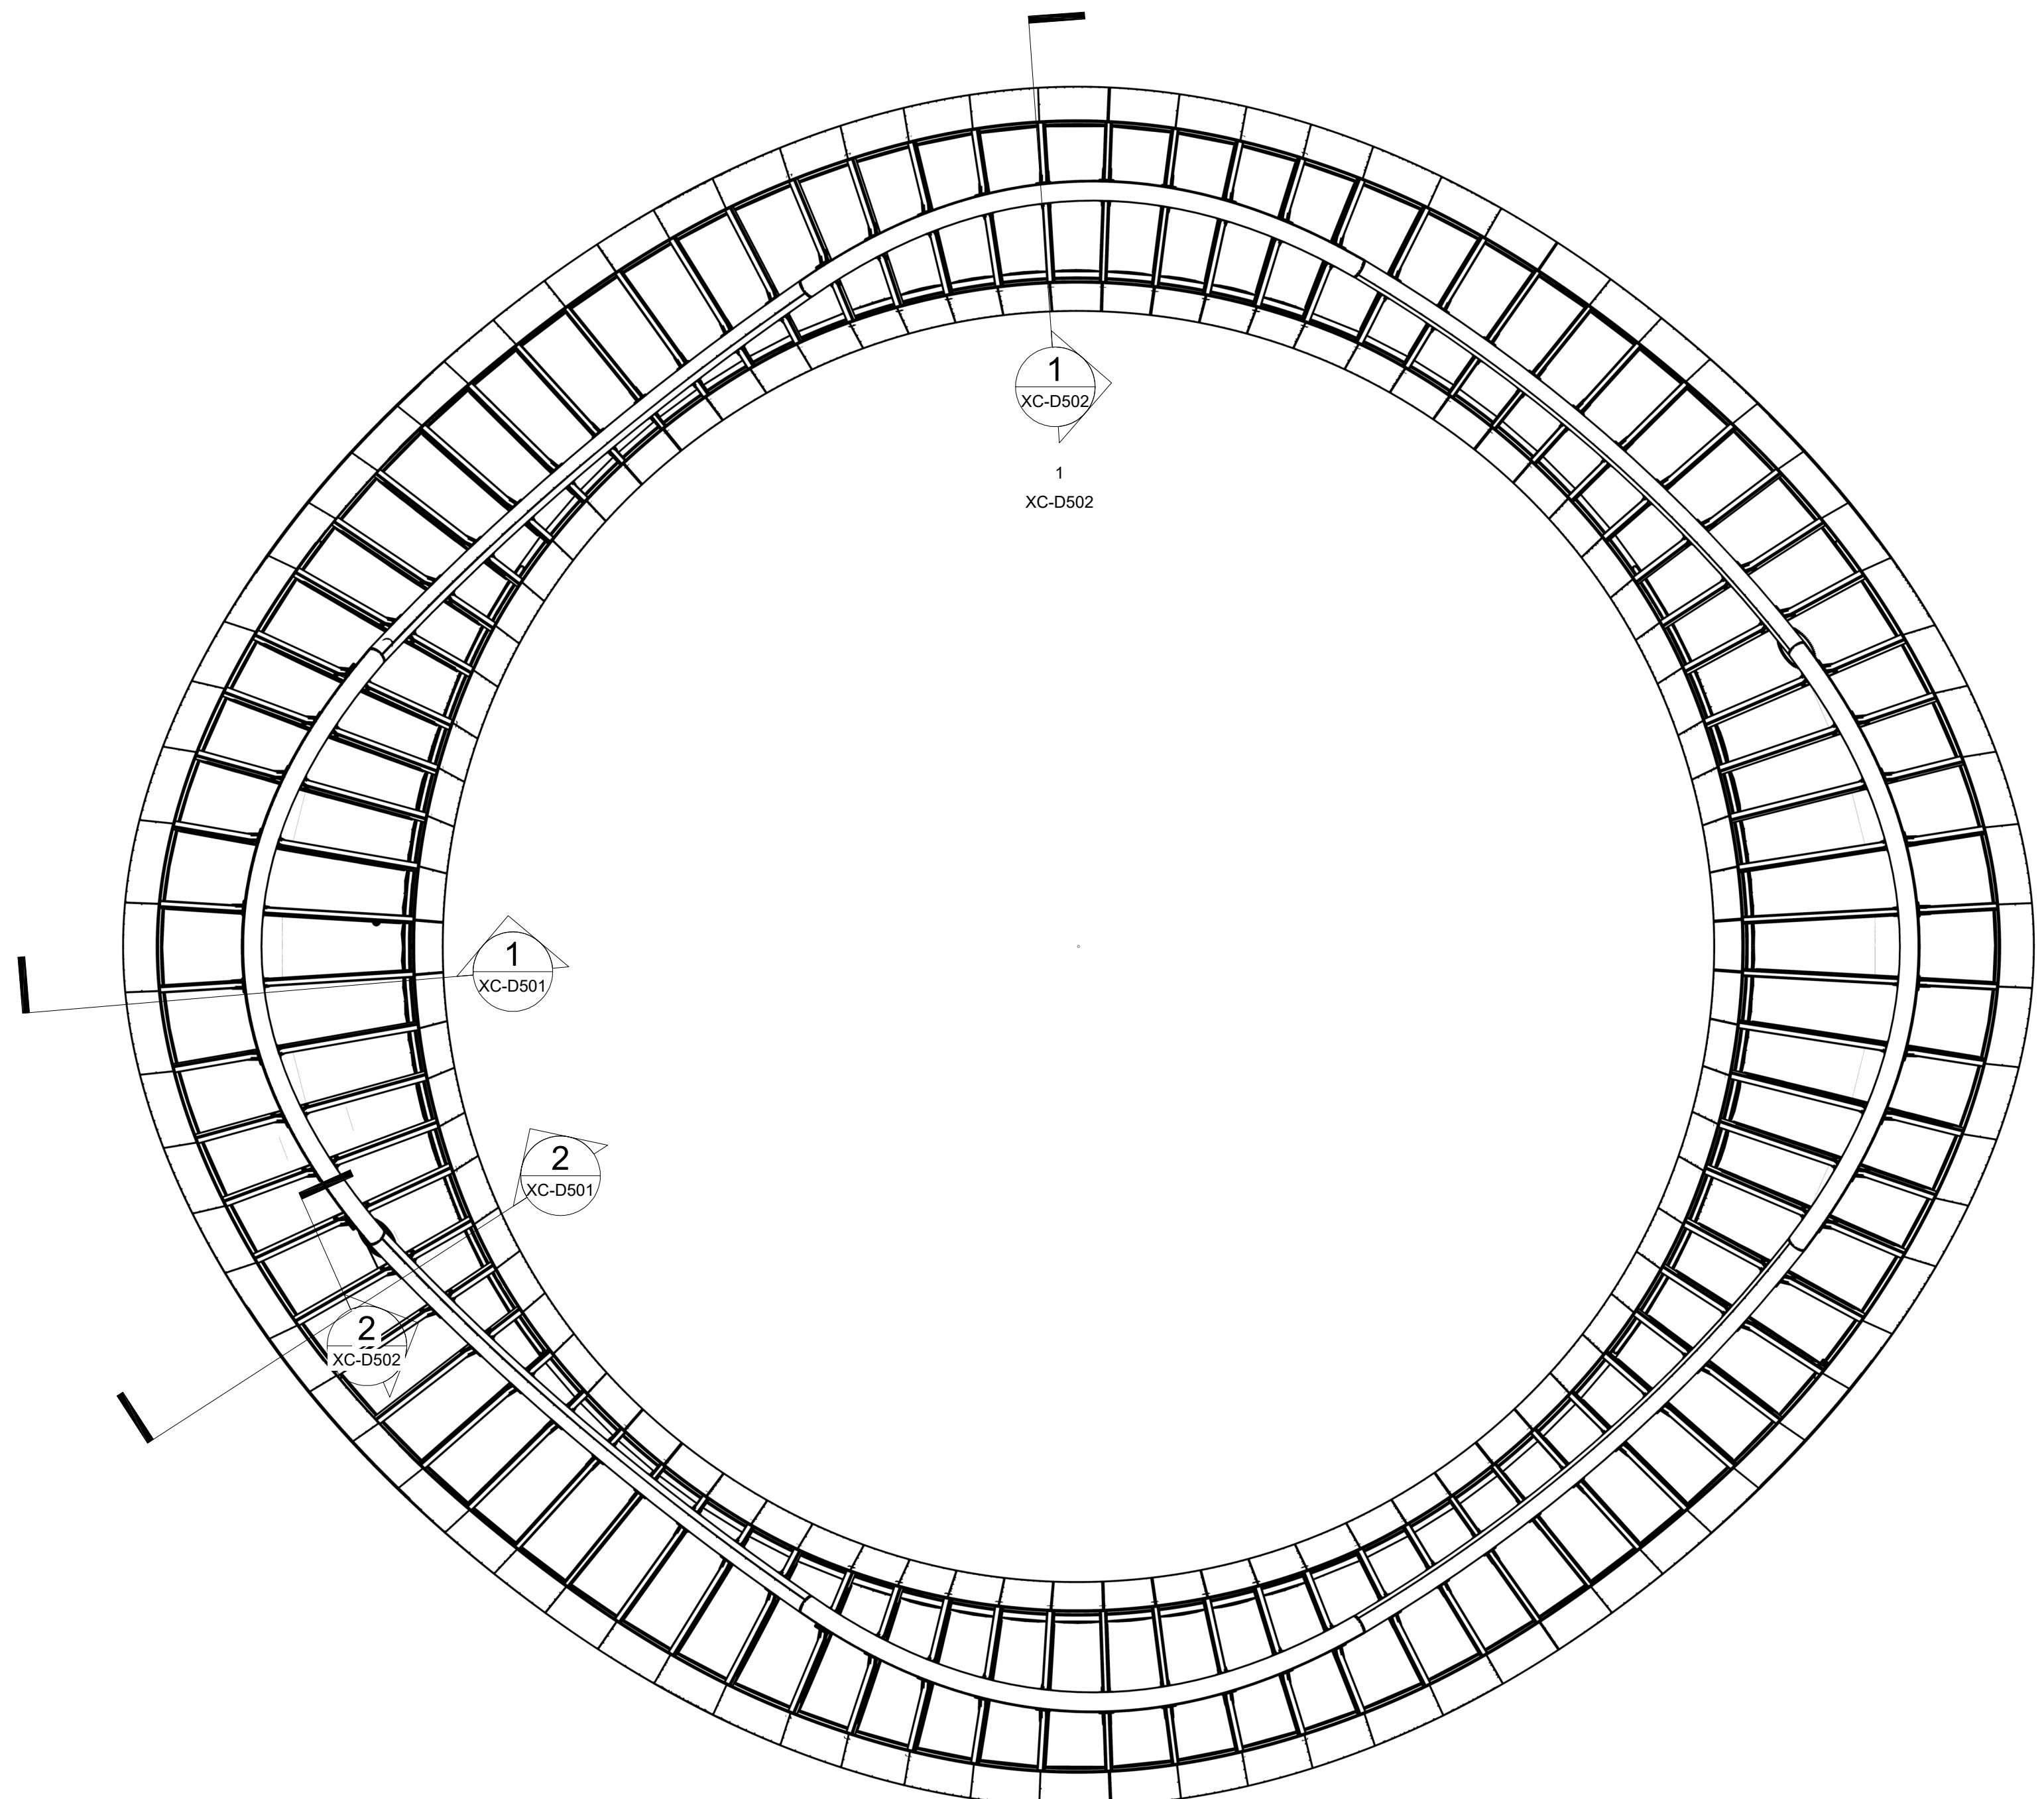

1 360 CANOPY - PLAN VIEW

SCALE: 1/8" = 1'-0"


ZAHNER REF: XX
ARCH REF: XX

360 CANOPY PLAN


PROJECT TITLE CITY OF SCOTTSDALE
CIVIC CENTER PLAZA


THIS SHEET SCALED FOR 24X36" BORDER	SCALE	DESIGNED	BID NO.	XC-D101
		DRAWN DS	AS-BUILT	COS PROJECT NO. DG04

SET ISSUE DATES		
DATE	ISSUE	
01/20/22 100% DRAWINGS		
<hr/> <hr/> <hr/>		
REVISIONS		
NO.	DATE	DESCRIPTION
<hr/> <hr/> <hr/>		

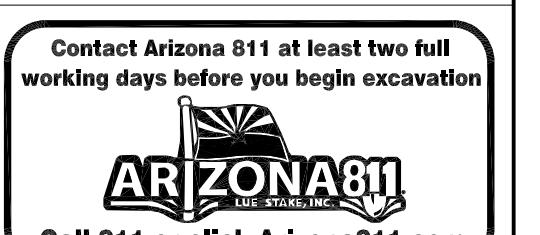


DATE: 01/20/2022	REVISION:	BY:
ENGINEER		PUBLIC WORKS
		CAPITAL PROJECT MANAGEMENT
		7447 E. INDIAN SCHOOL RD. SCOTTSDALE, ARIZONA 85251
SHEET TITLE		

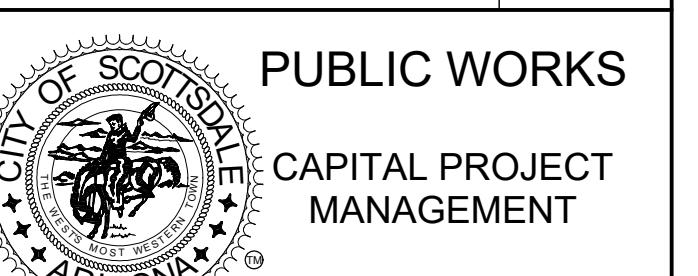

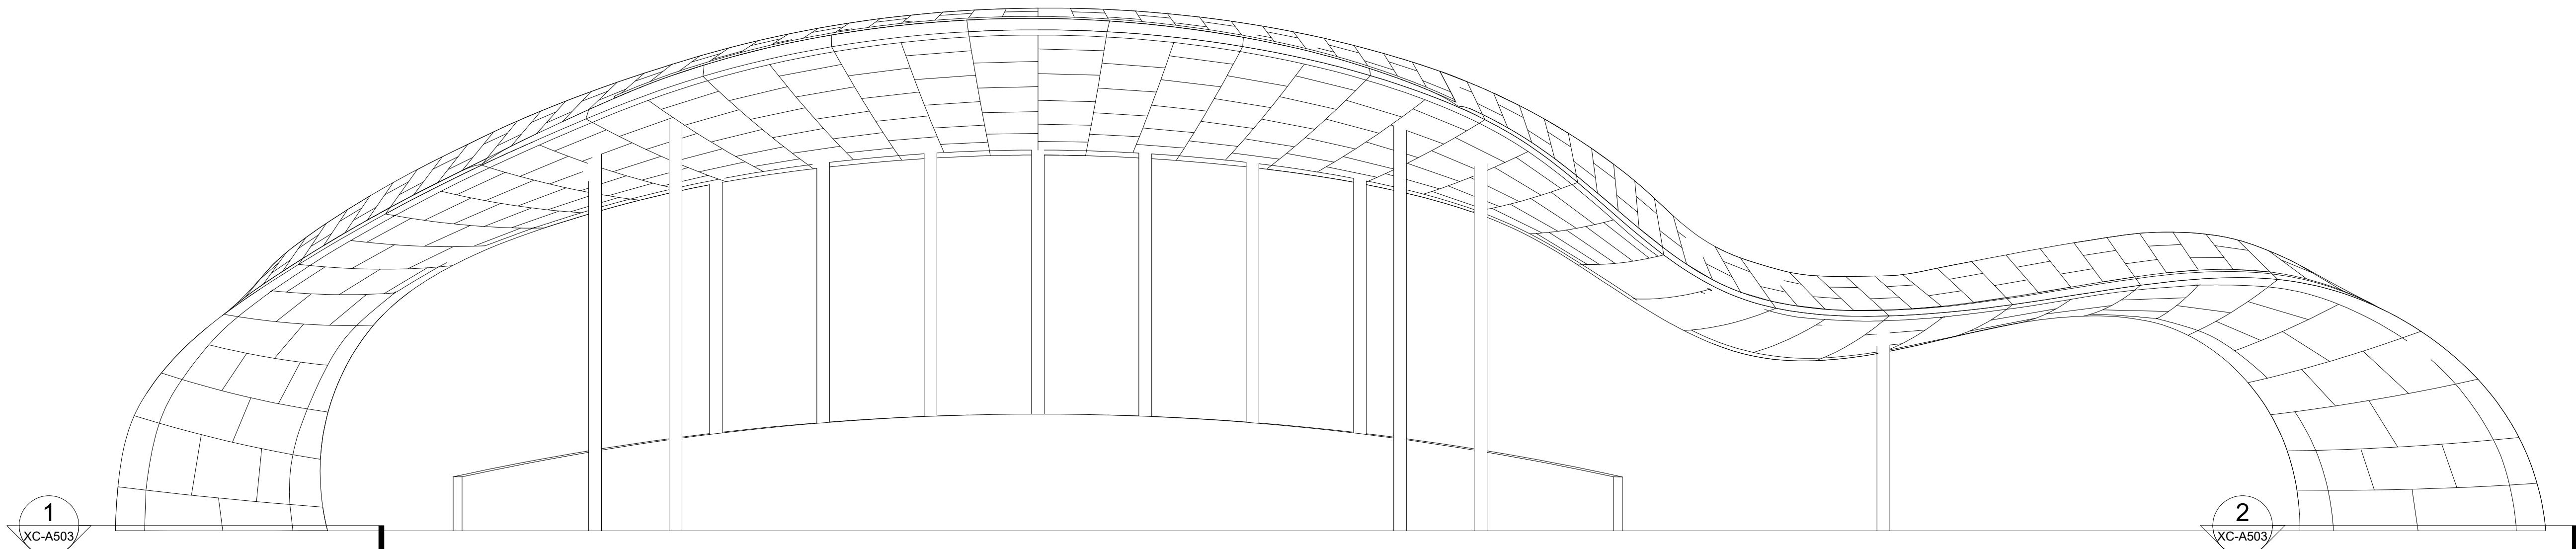

① EAST BOWL WEST ELEVATION
SCALE: 3/16" = 1'-0"
ZAHNER REF: N/A
ARCH REF: N/A

SET ISSUE DATES		
DATE	ISSUE	BY:
01/20/22 100% DRAWINGS		
REVISIONS		
NO.	DATE	DESCRIPTION

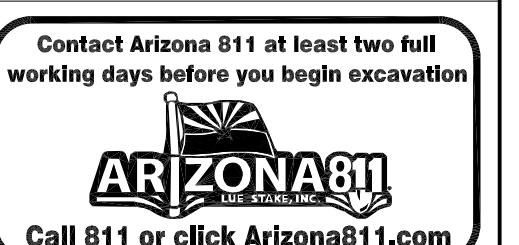


DATE: 01/20/2022	REVISION:	BY:
ENGINEER		PUBLIC WORKS
		CAPITAL PROJECT MANAGEMENT
SHEET TITLE CITY OF SCOTTSDALE CIVIC CENTER PLAZA		

EAST BOWL WEST ELEVATION

PROJECT TITLE		CITY OF SCOTTSDALE CIVIC CENTER PLAZA	
DESIGNED	BID NO.	SCALE	XC-A201
DRAWN DS	AS-BUILT	COS PROJECT NO.	DG04

THIS SHEET SCALED
FOR 24X36" BORDER

BY:
PROTECTED
BY:

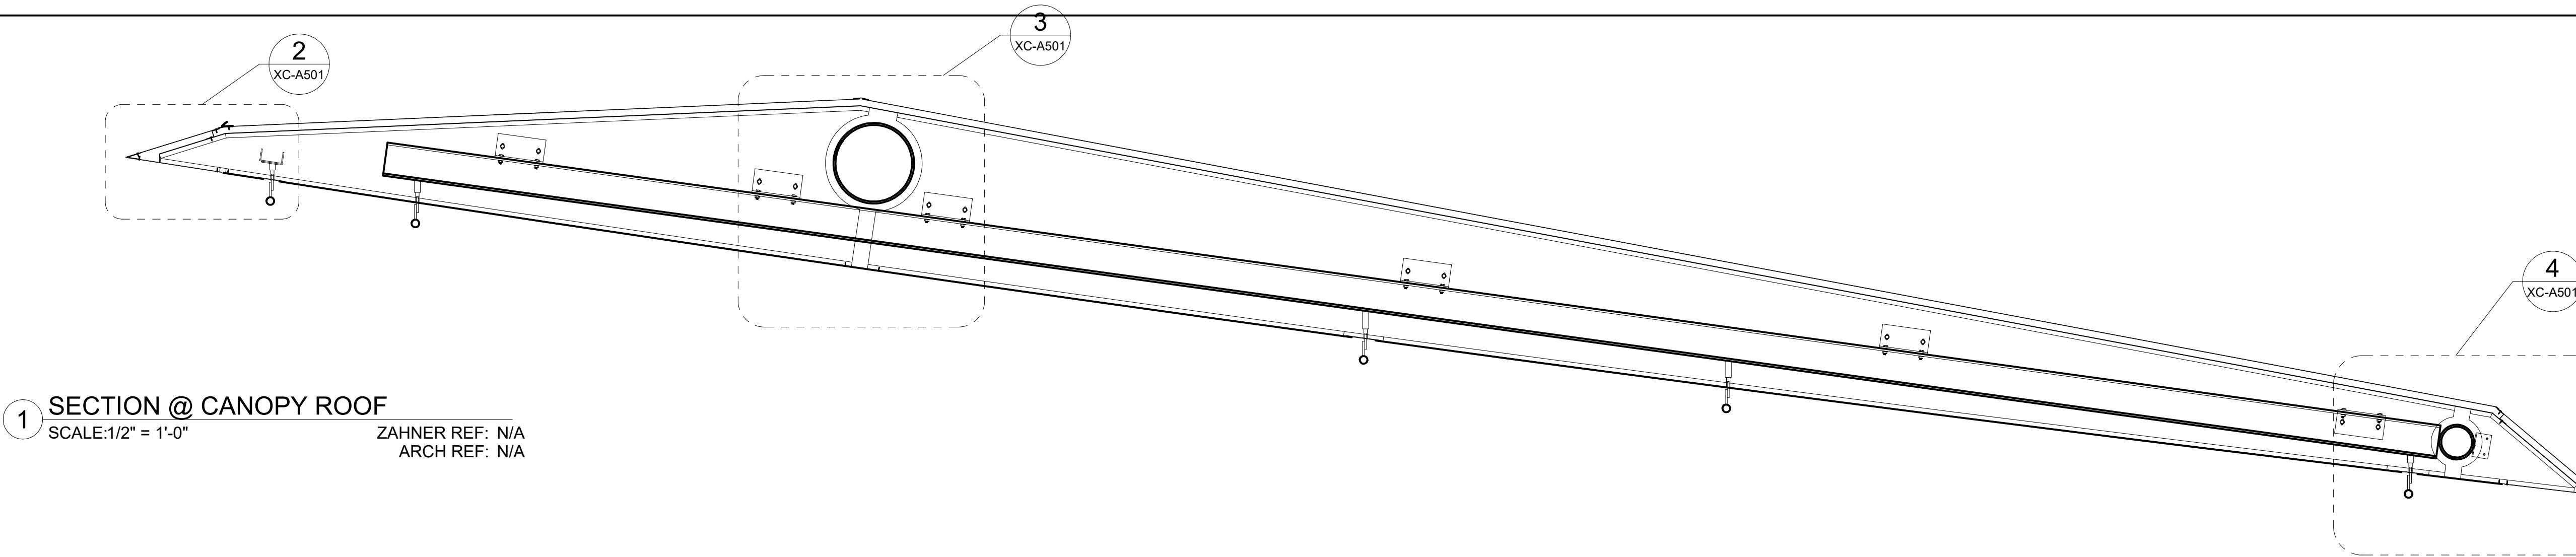


1 SECTION @ CANOPY ROOF

SCALE: 1/2" = 1'-0"
 ZAHNER REF: N/A
 ARCH REF: N/A


2 SECTION DETAIL @ DOWNSTAGE CANOPY

SCALE: 1 1/2" = 1'-0"
 ZAHNER REF: N/A
 ARCH REF: N/A

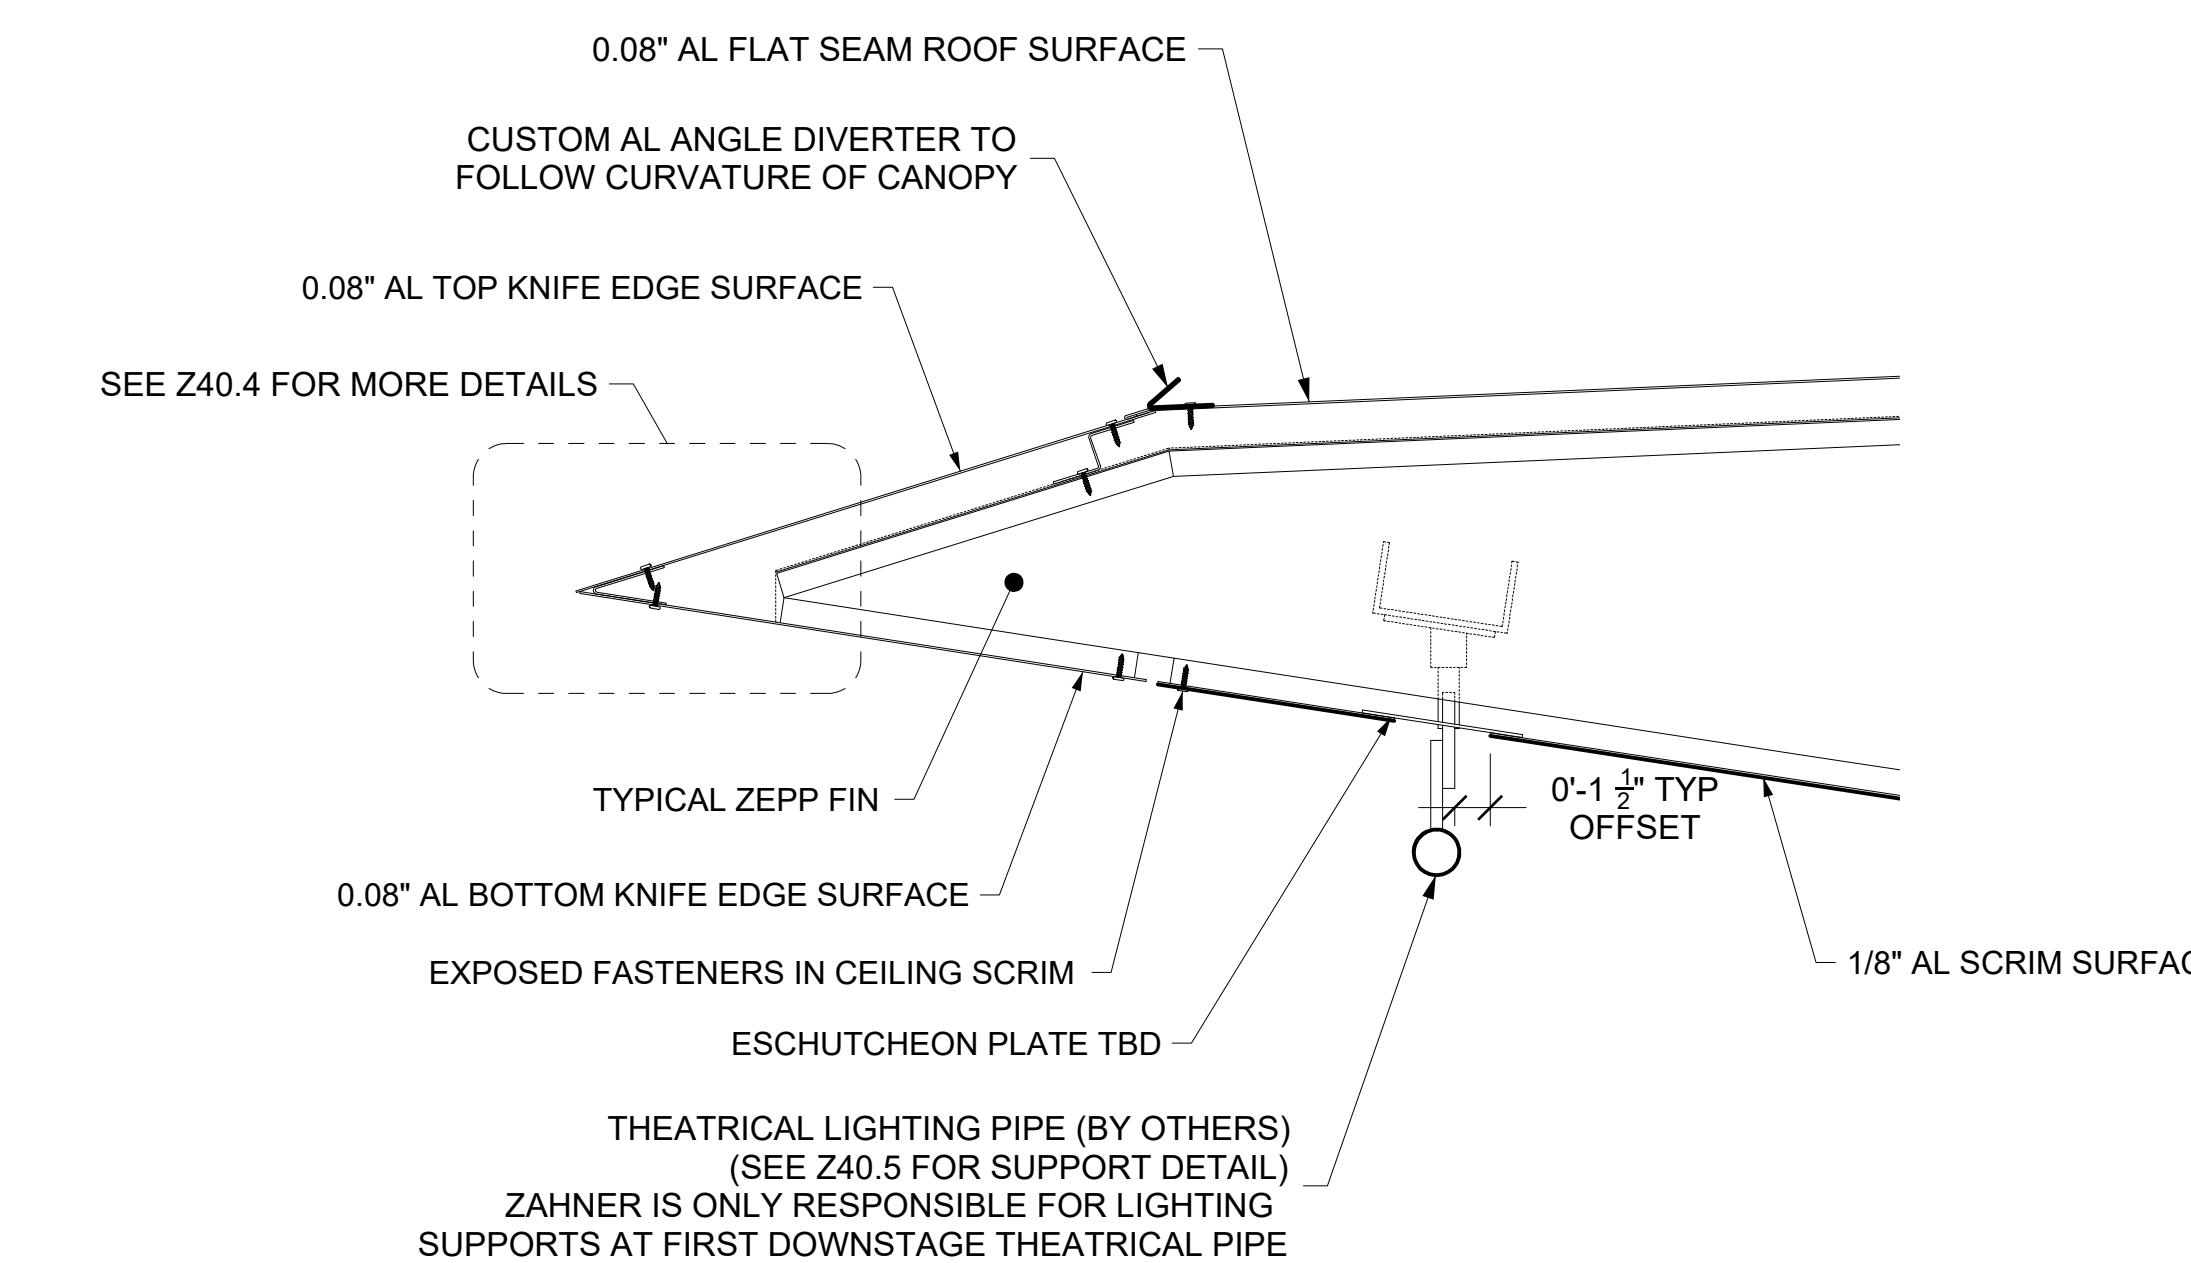

3 SECTION DETAIL @ DOWNSTAGE CANOPY

SCALE: 1 1/2" = 1'-0"
 ZAHNER REF: N/A
 ARCH REF: N/A

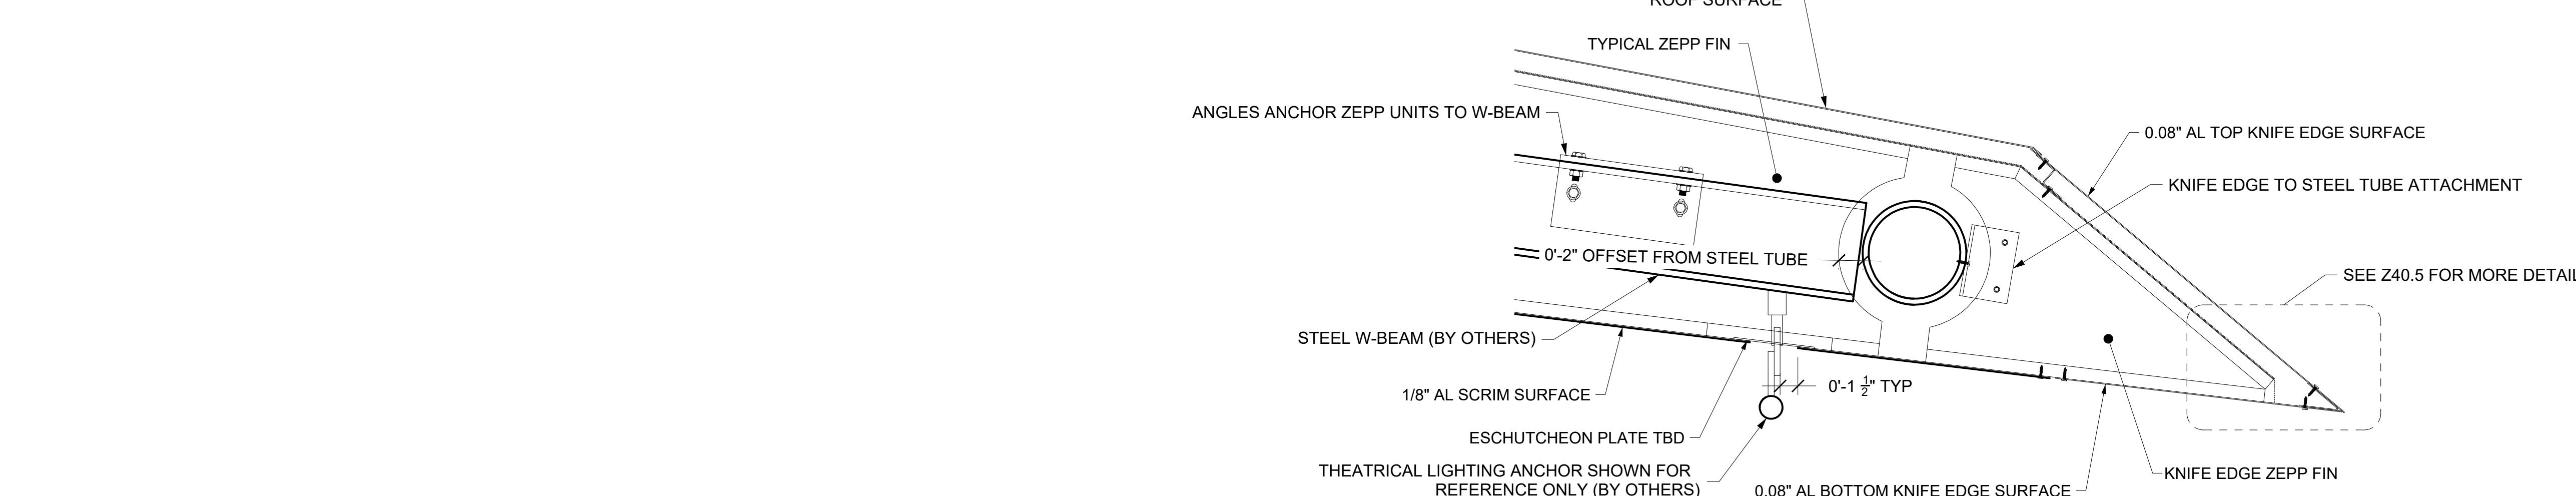


4 SECTION DETAIL @ UPSTAGE CANOPY

SCALE: 1 1/2" = 1'-0"
 ZAHNER REF: N/A
 ARCH REF: N/A

SET ISSUE DATES	
DATE	ISSUE
01/20/22 100% DRAWINGS	

REVISIONS		
NO.	DATE	DESCRIPTION

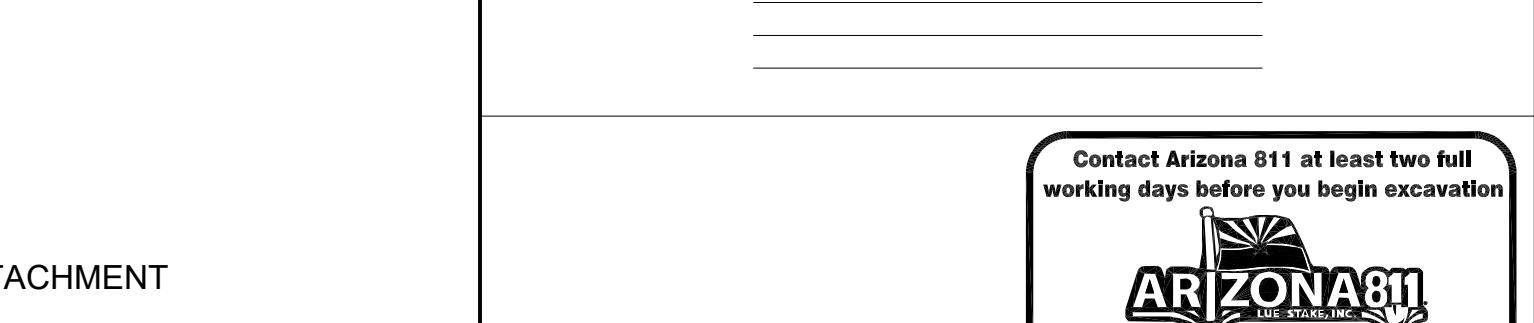


DATE: 01/20/2022	REVISION:	BY:
ENGINEER		PUBLIC WORKS
		CAPITAL PROJECT MANAGEMENT
		7447 E. INDIAN SCHOOL RD., SCOTTSDALE, ARIZONA 85251
SHEET TITLE		


EAST BOWL - SECTION & DETAILS

PROJECT TITLE: CITY OF SCOTTSDALE CIVIC CENTER PLAZA


THIS SHEET SCALED FOR 24X36" BORDER	SCALE	DESIGNED	BID NO.	XC-A501
		DRAWN DS	AS-BUILT	COS PROJECT NO. DG04

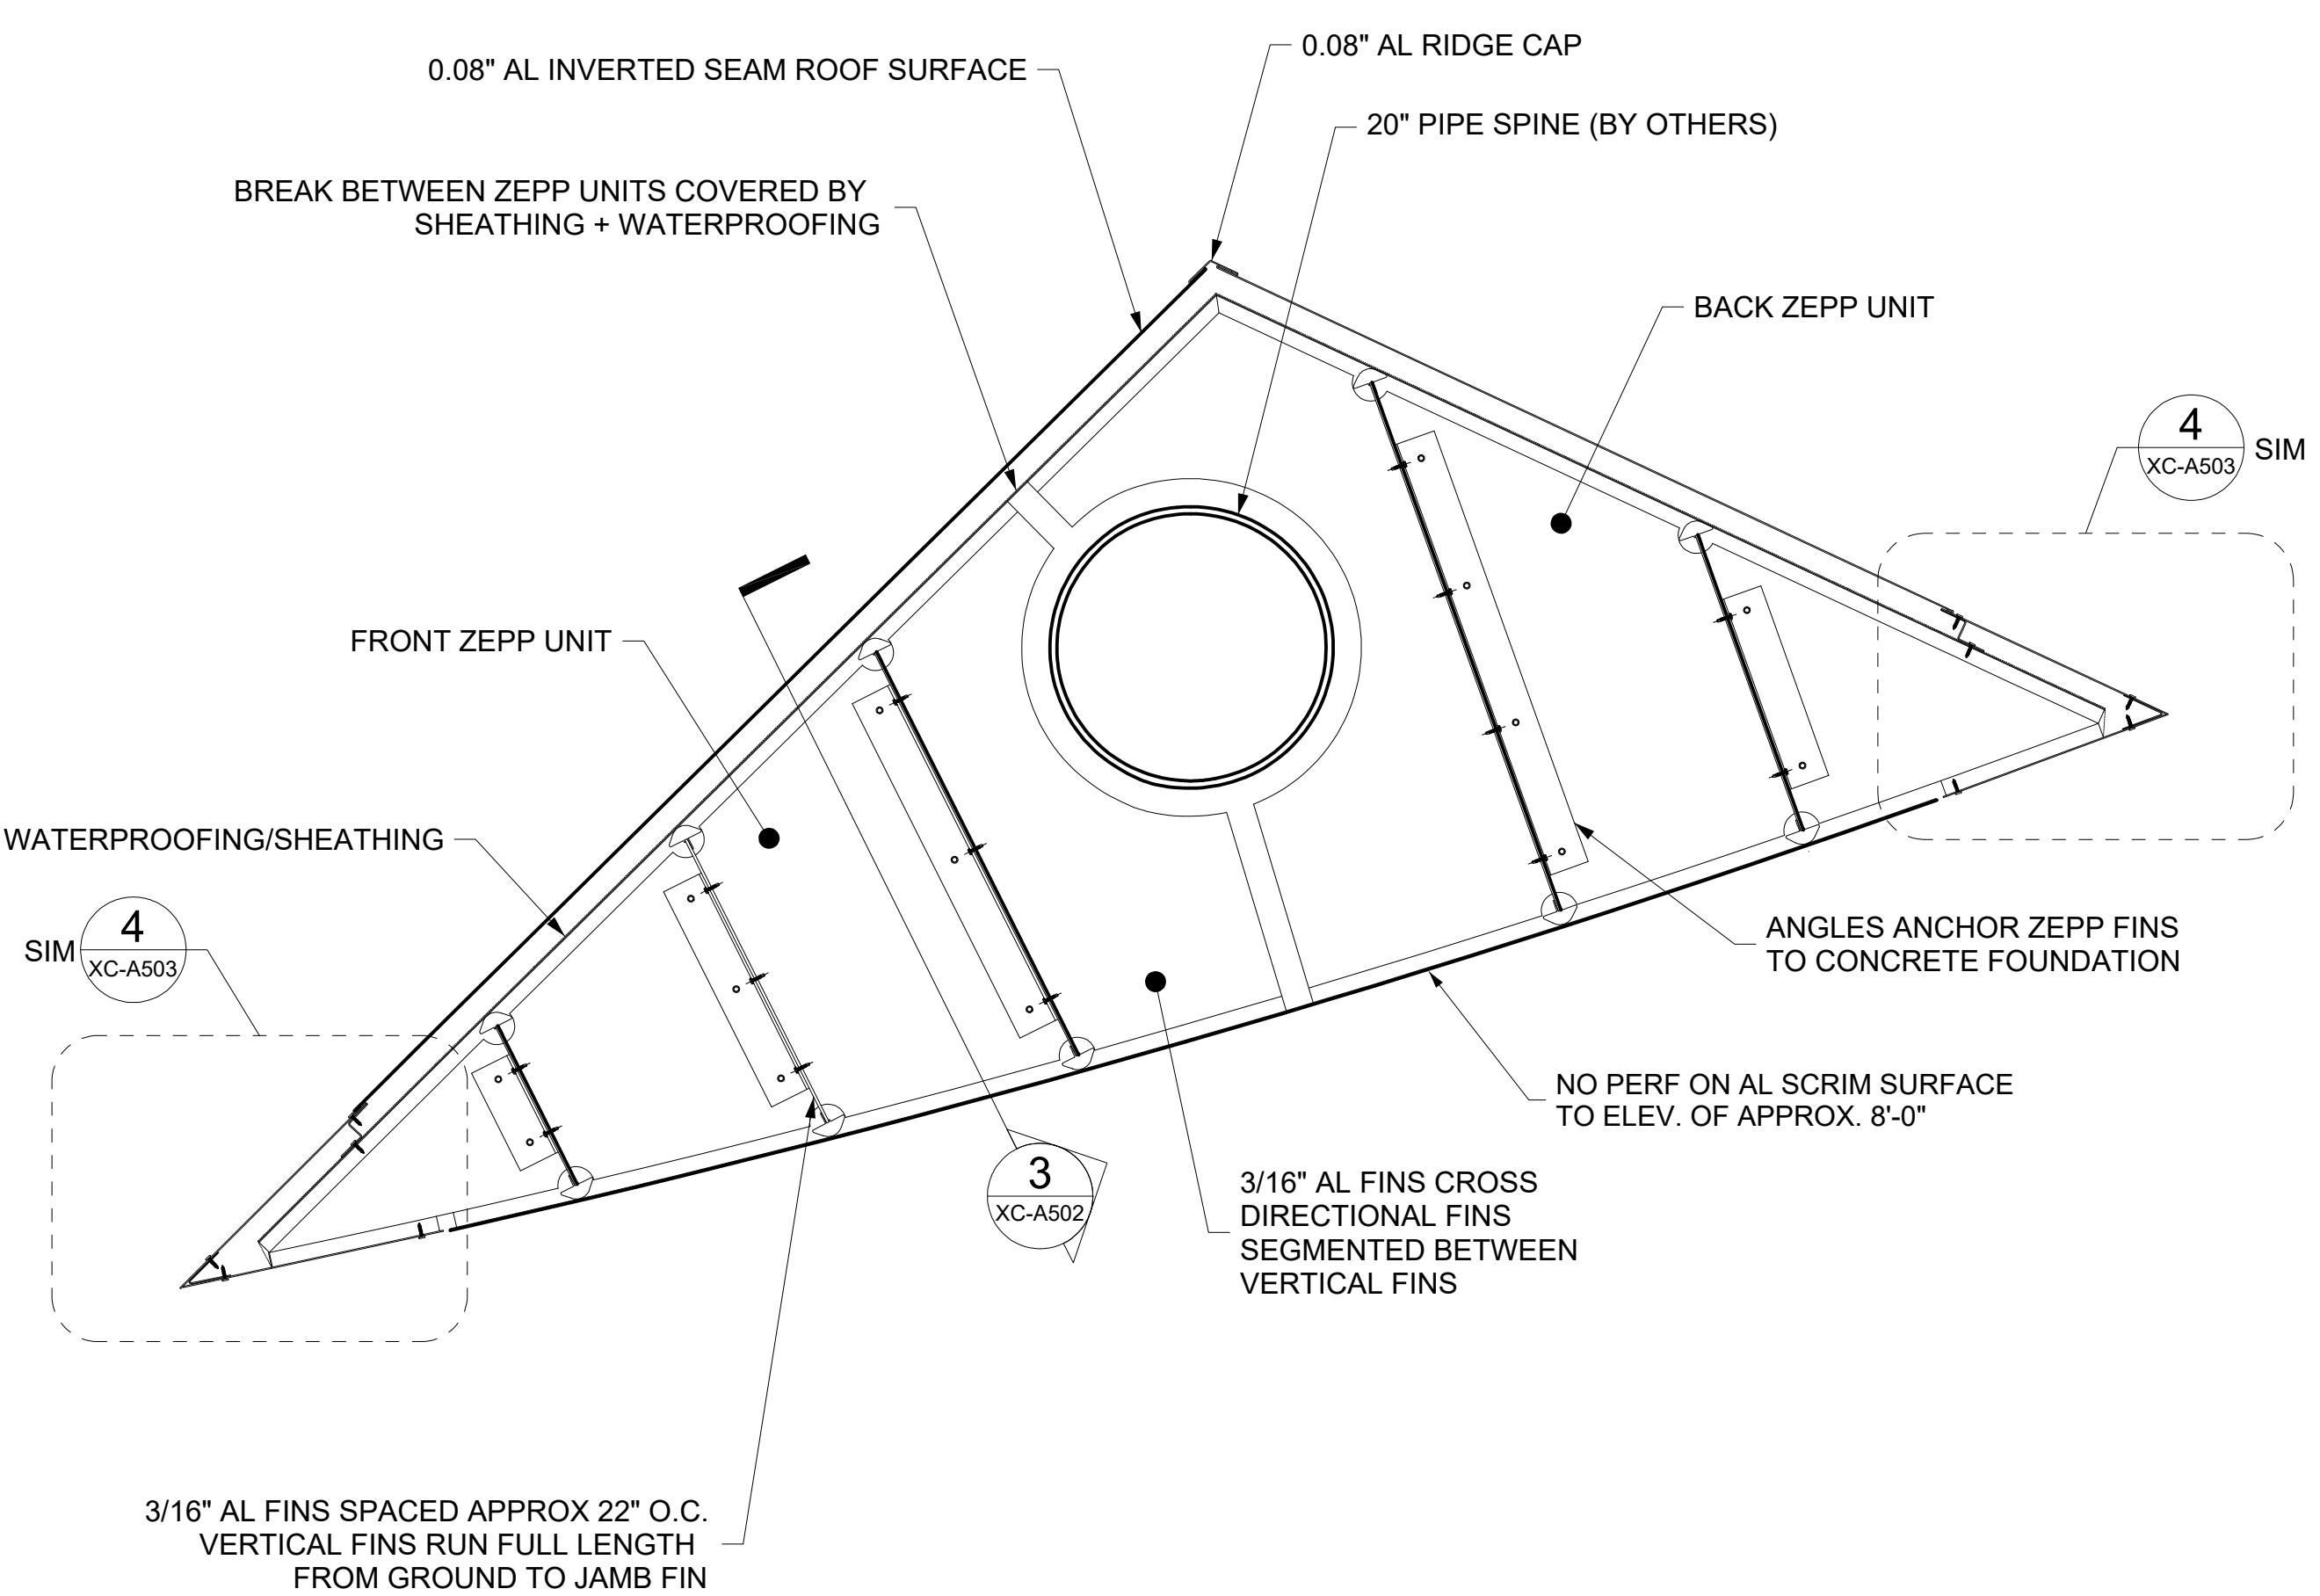

1 PLAN DETAIL @ NORTH WING WALL
SCALE: 1" = 1'-0"
ZAHNER REF: N/A
ARCH REF: N/A

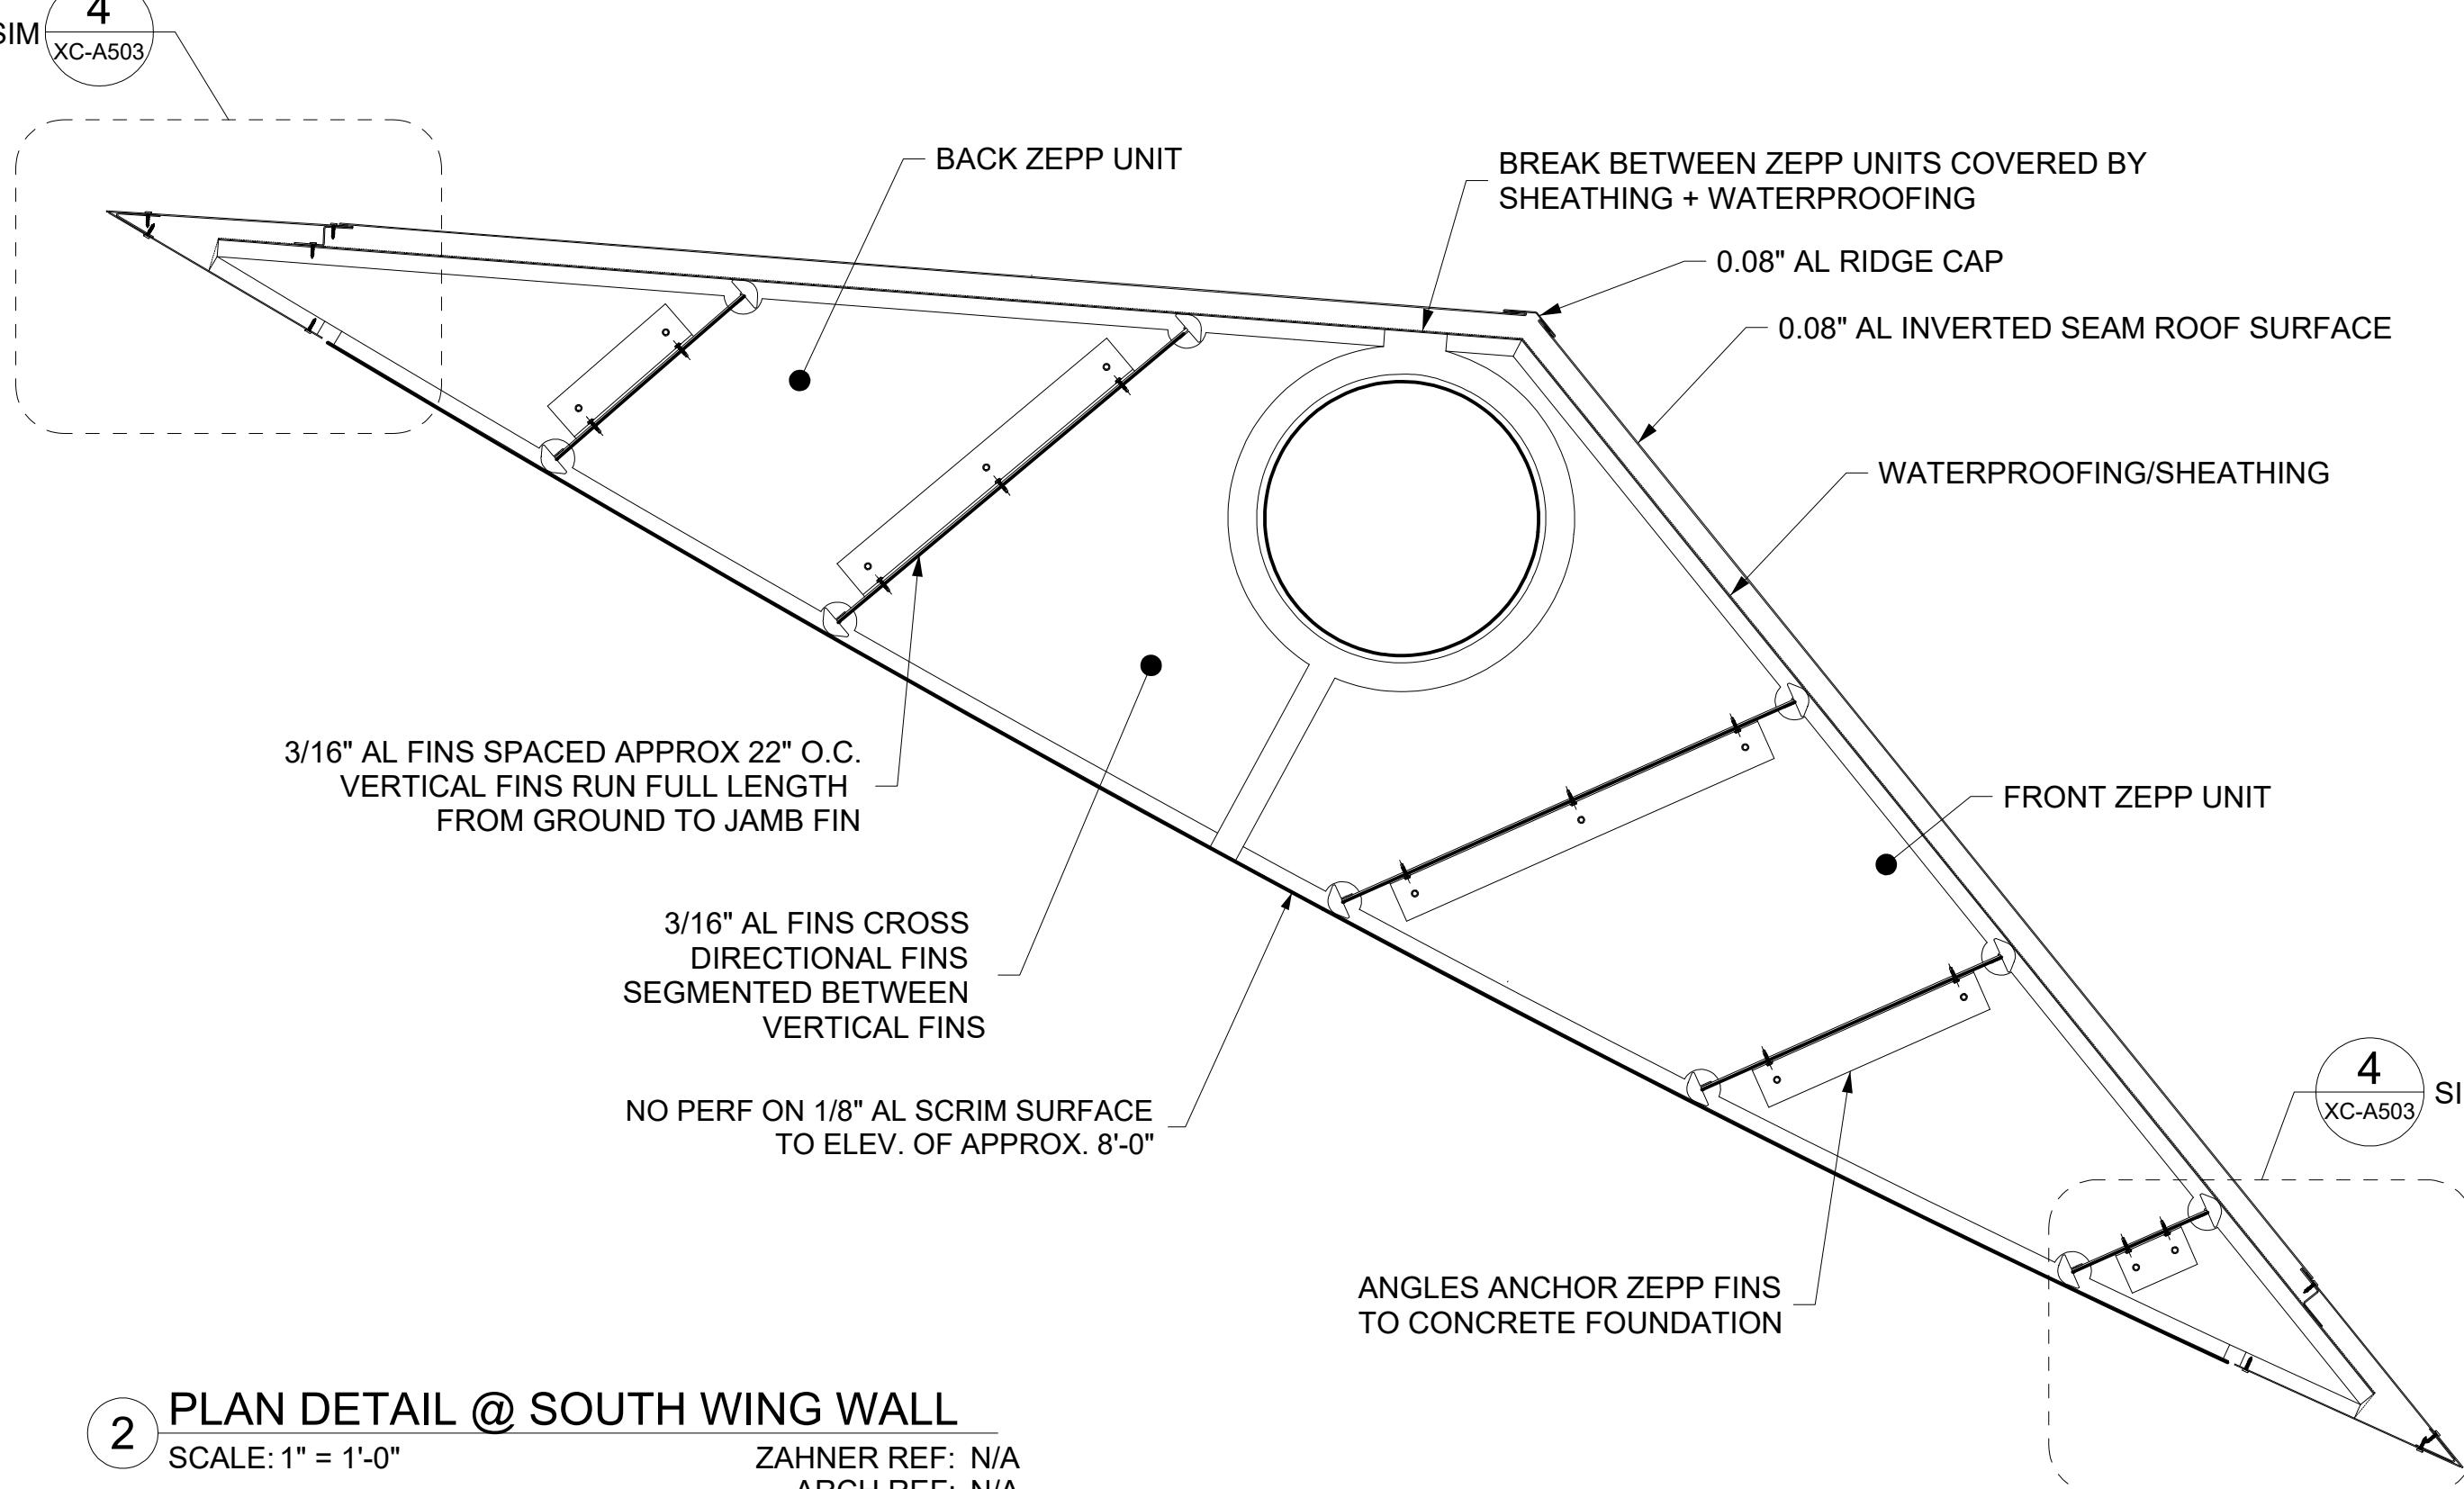


2 PLAN DETAIL @ SOUTH WING WALL
SCALE: 1" = 1'-0"
ZAHNER REF: N/A
ARCH REF: N/A

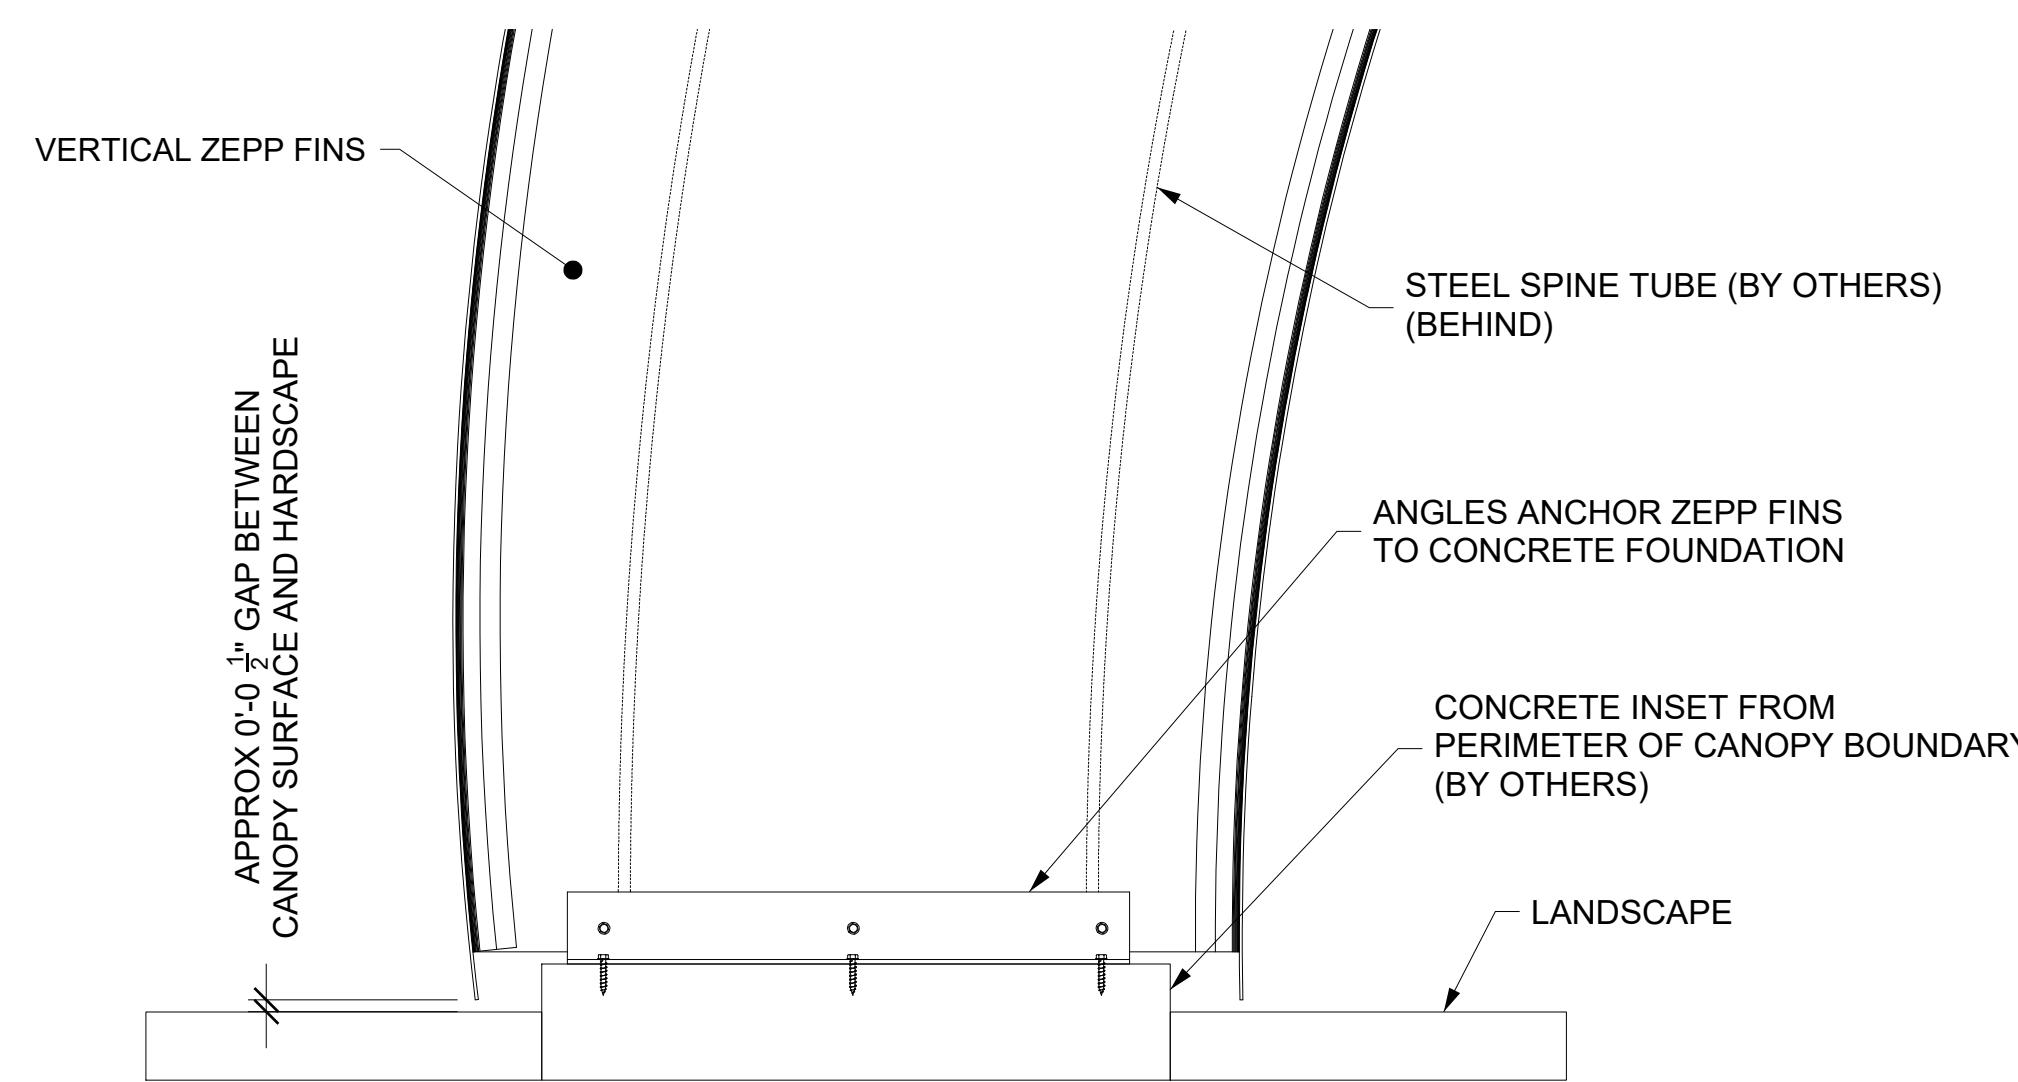

3 SECTION DETAIL @ NORTH WING WALL
SCALE: 1 1/2" = 1'-0"
ZAHNER REF: N/A
ARCH REF: N/A

SET ISSUE DATES		
DATE	ISSUE	
01/20/22 100% DRAWINGS		
REVISIONS		
NO.	DATE	DESCRIPTION

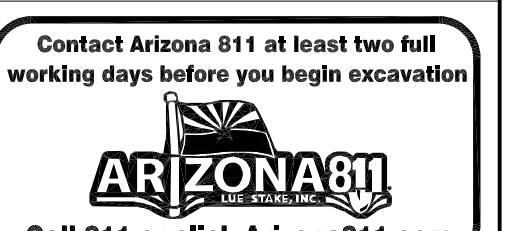


DATE: 01/20/2022	REVISION:	BY:
ENGINEER		PUBLIC WORKS
		CAPITAL PROJECT MANAGEMENT
7447 E. INDIAN SCHOOL RD., SCOTTSDALE, ARIZONA 85251		
SHEET TITLE		


EAST BOWL - WING WALL PLAN DETAILS

PROJECT TITLE CITY OF SCOTTSDALE
CIVIC CENTER PLAZA


THIS SHEET SCALED FOR 24X36" BORDER	SCALE	DESIGNED	BID NO.	XC-A502
	DRAWN DS	AS-BUILT	COS PROJECT NO. DG04	

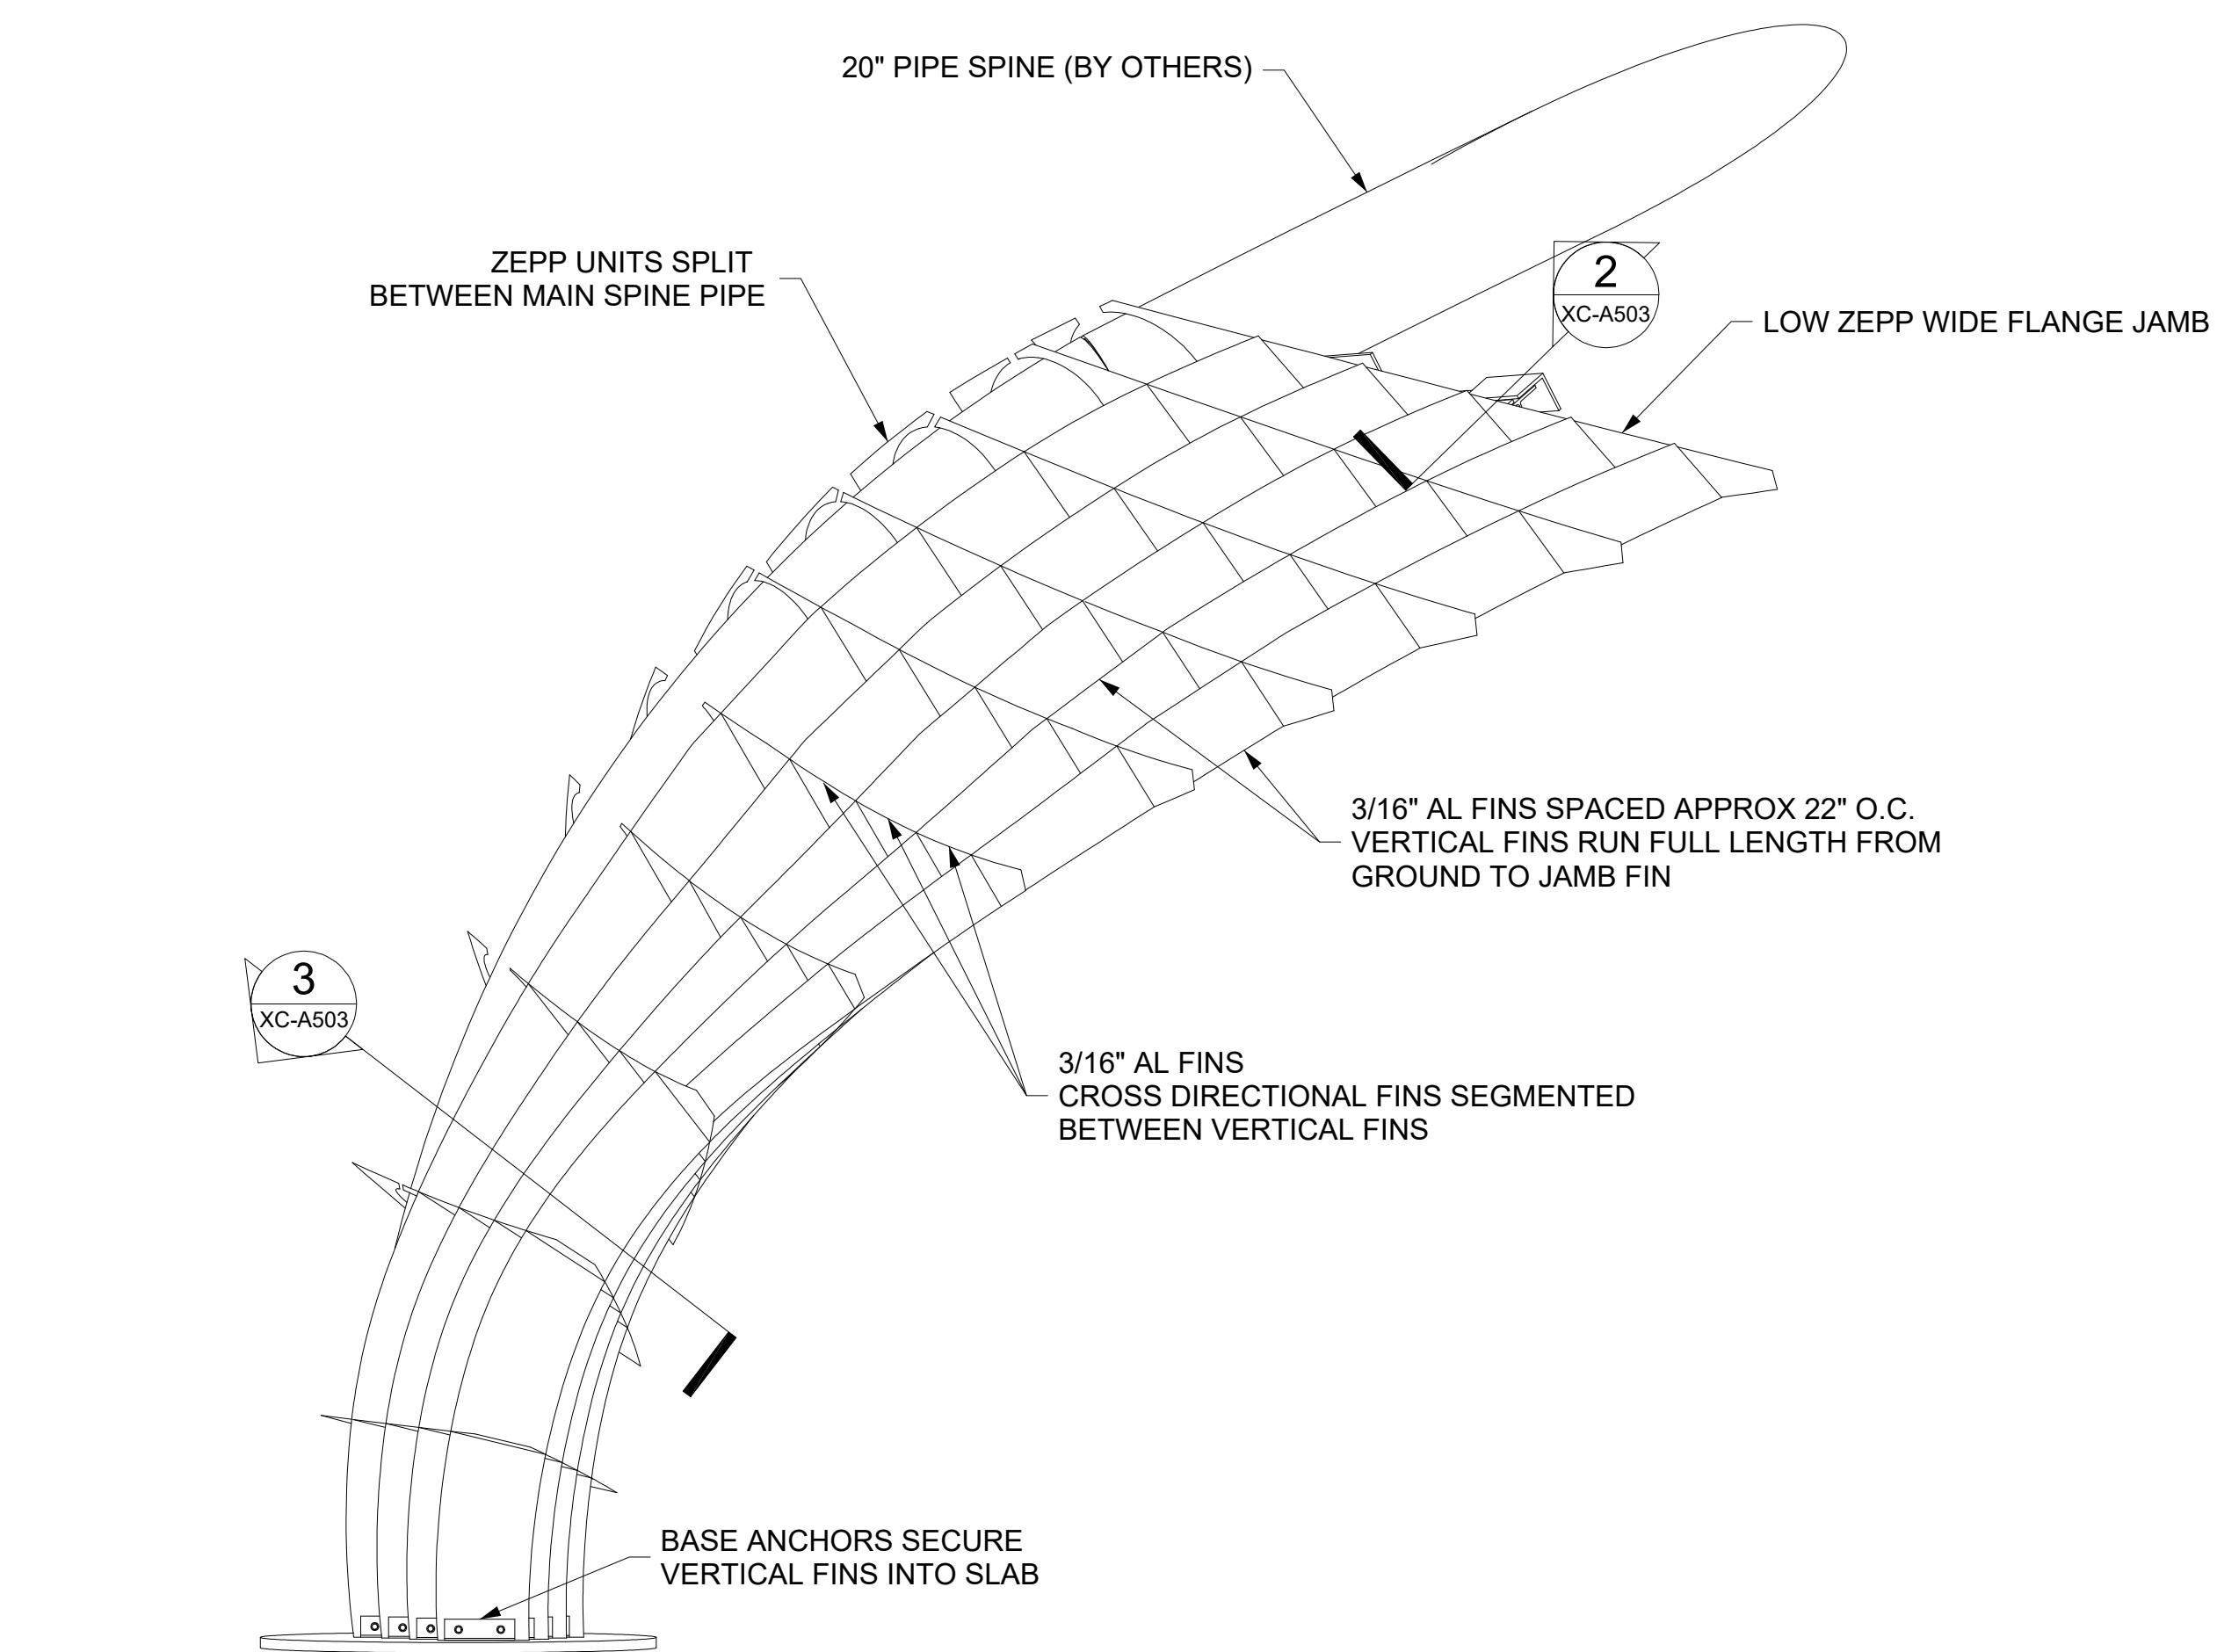


1 WING WALL ZEPP SUB STRUCTURE
 SCALE: 1/2" = 1'-0"
 ZAHNER REF: N/A
 ARCH REF: N/A

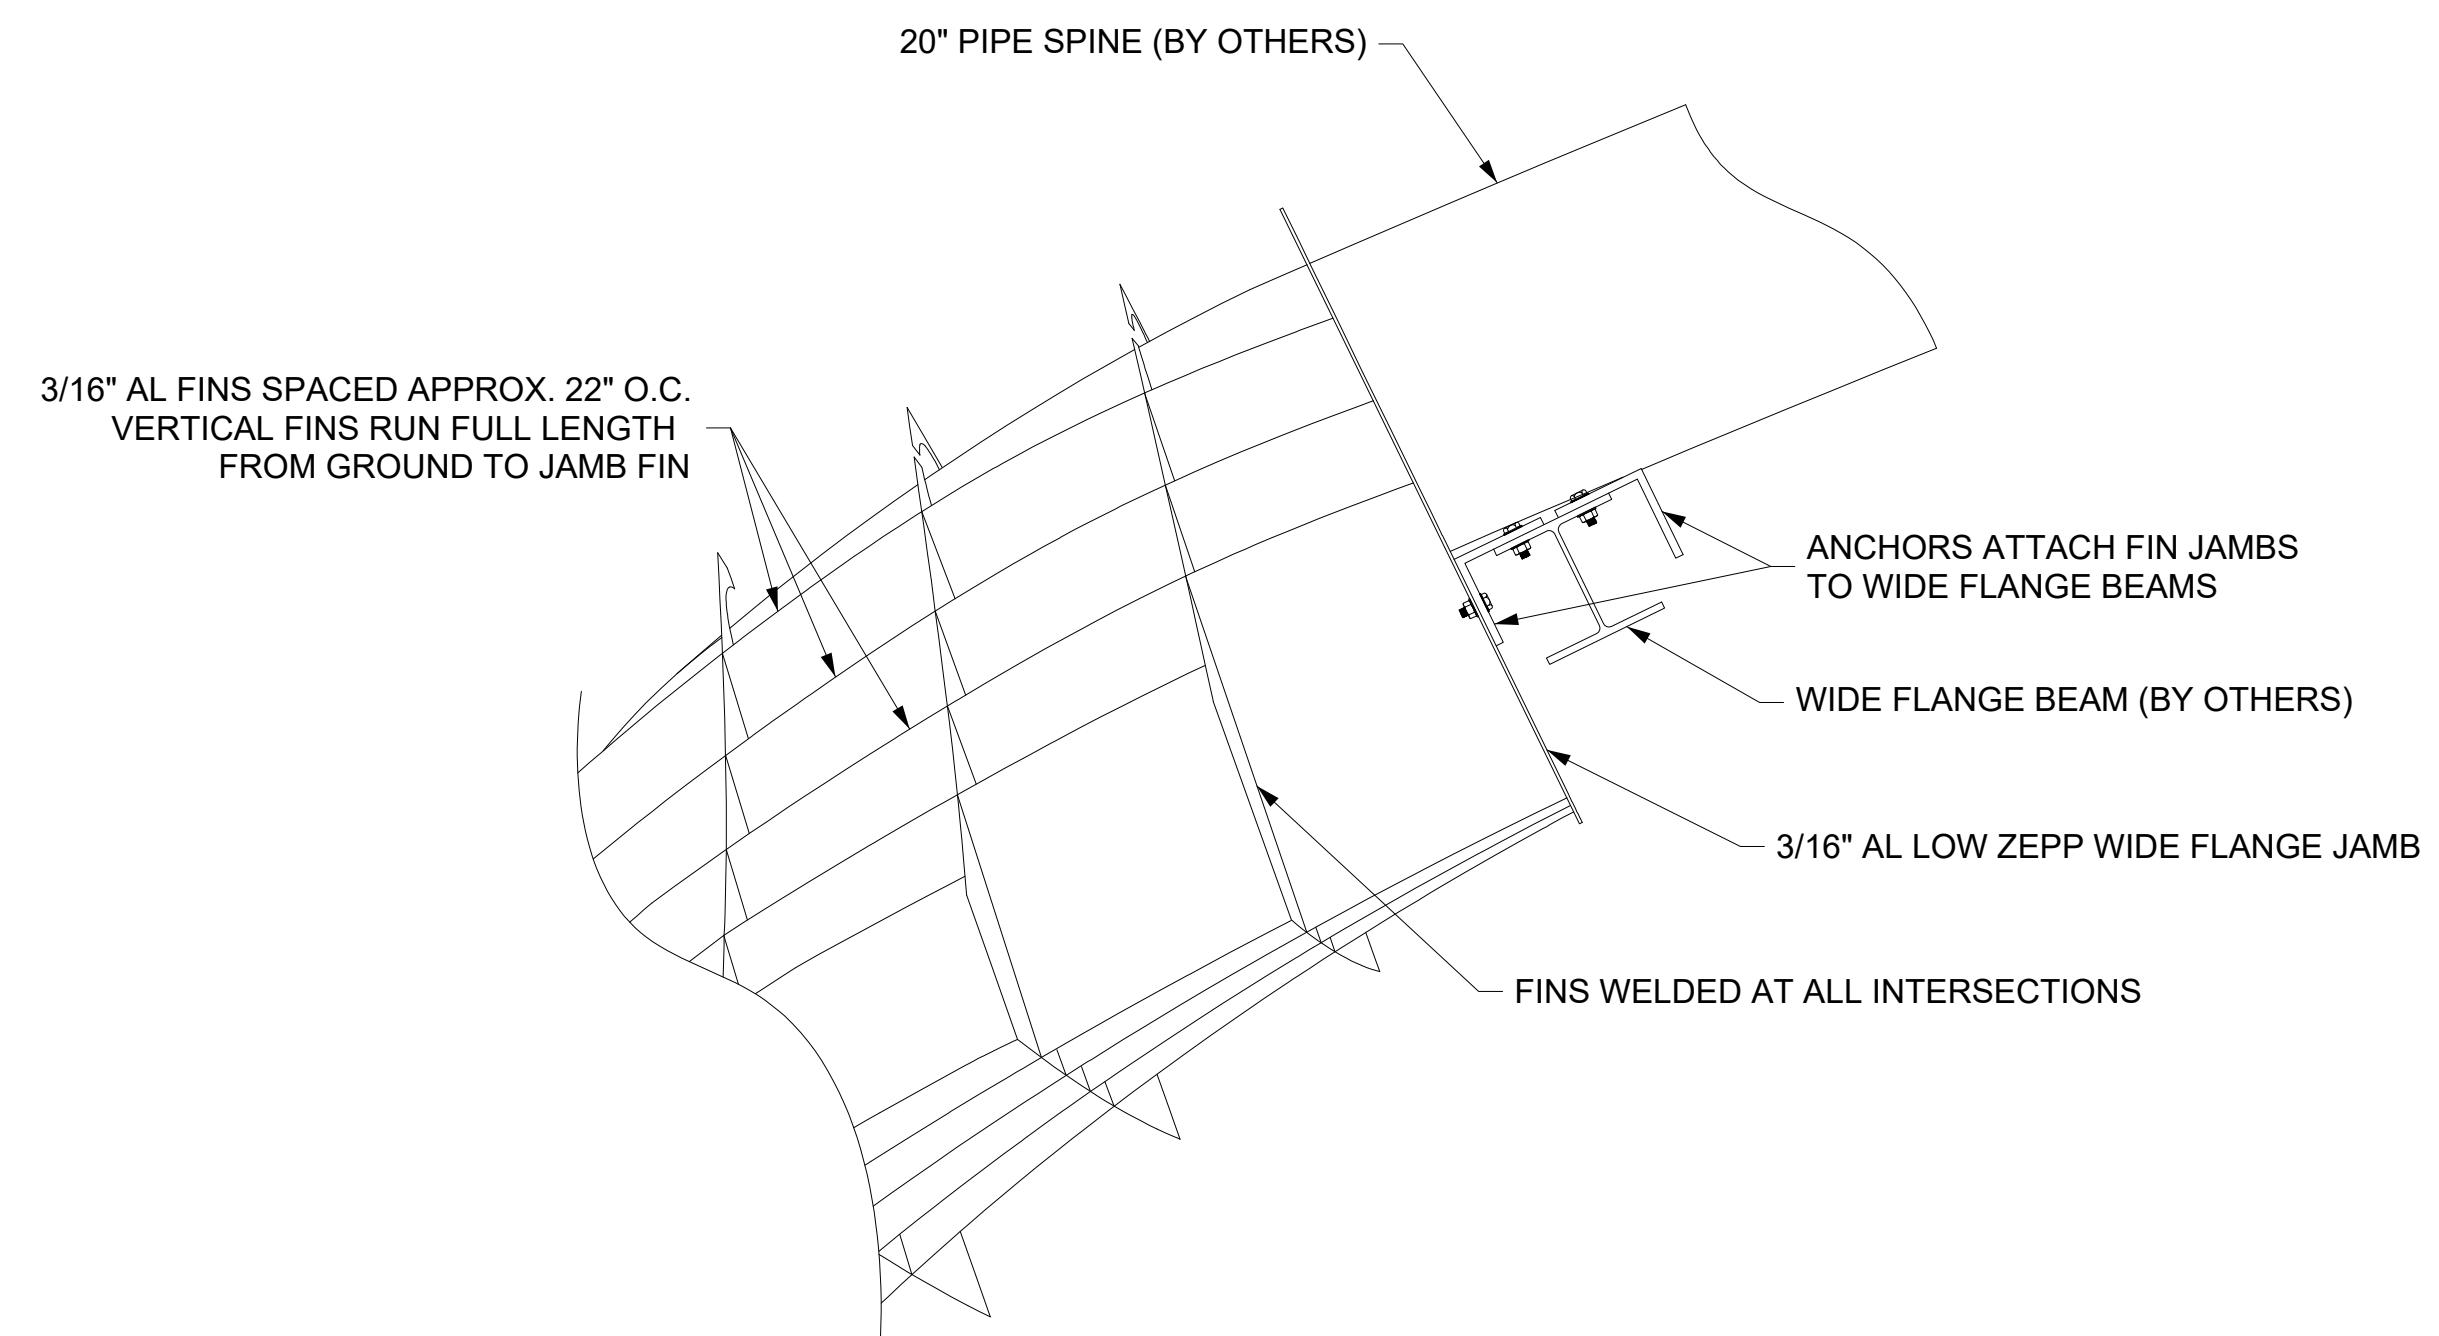

2 WING WALL ZEPP UNIT ATTACHMENT TO STEEL
 SCALE: 1" = 1'-0"
 ZAHNER REF: N/A
 ARCH REF: N/A

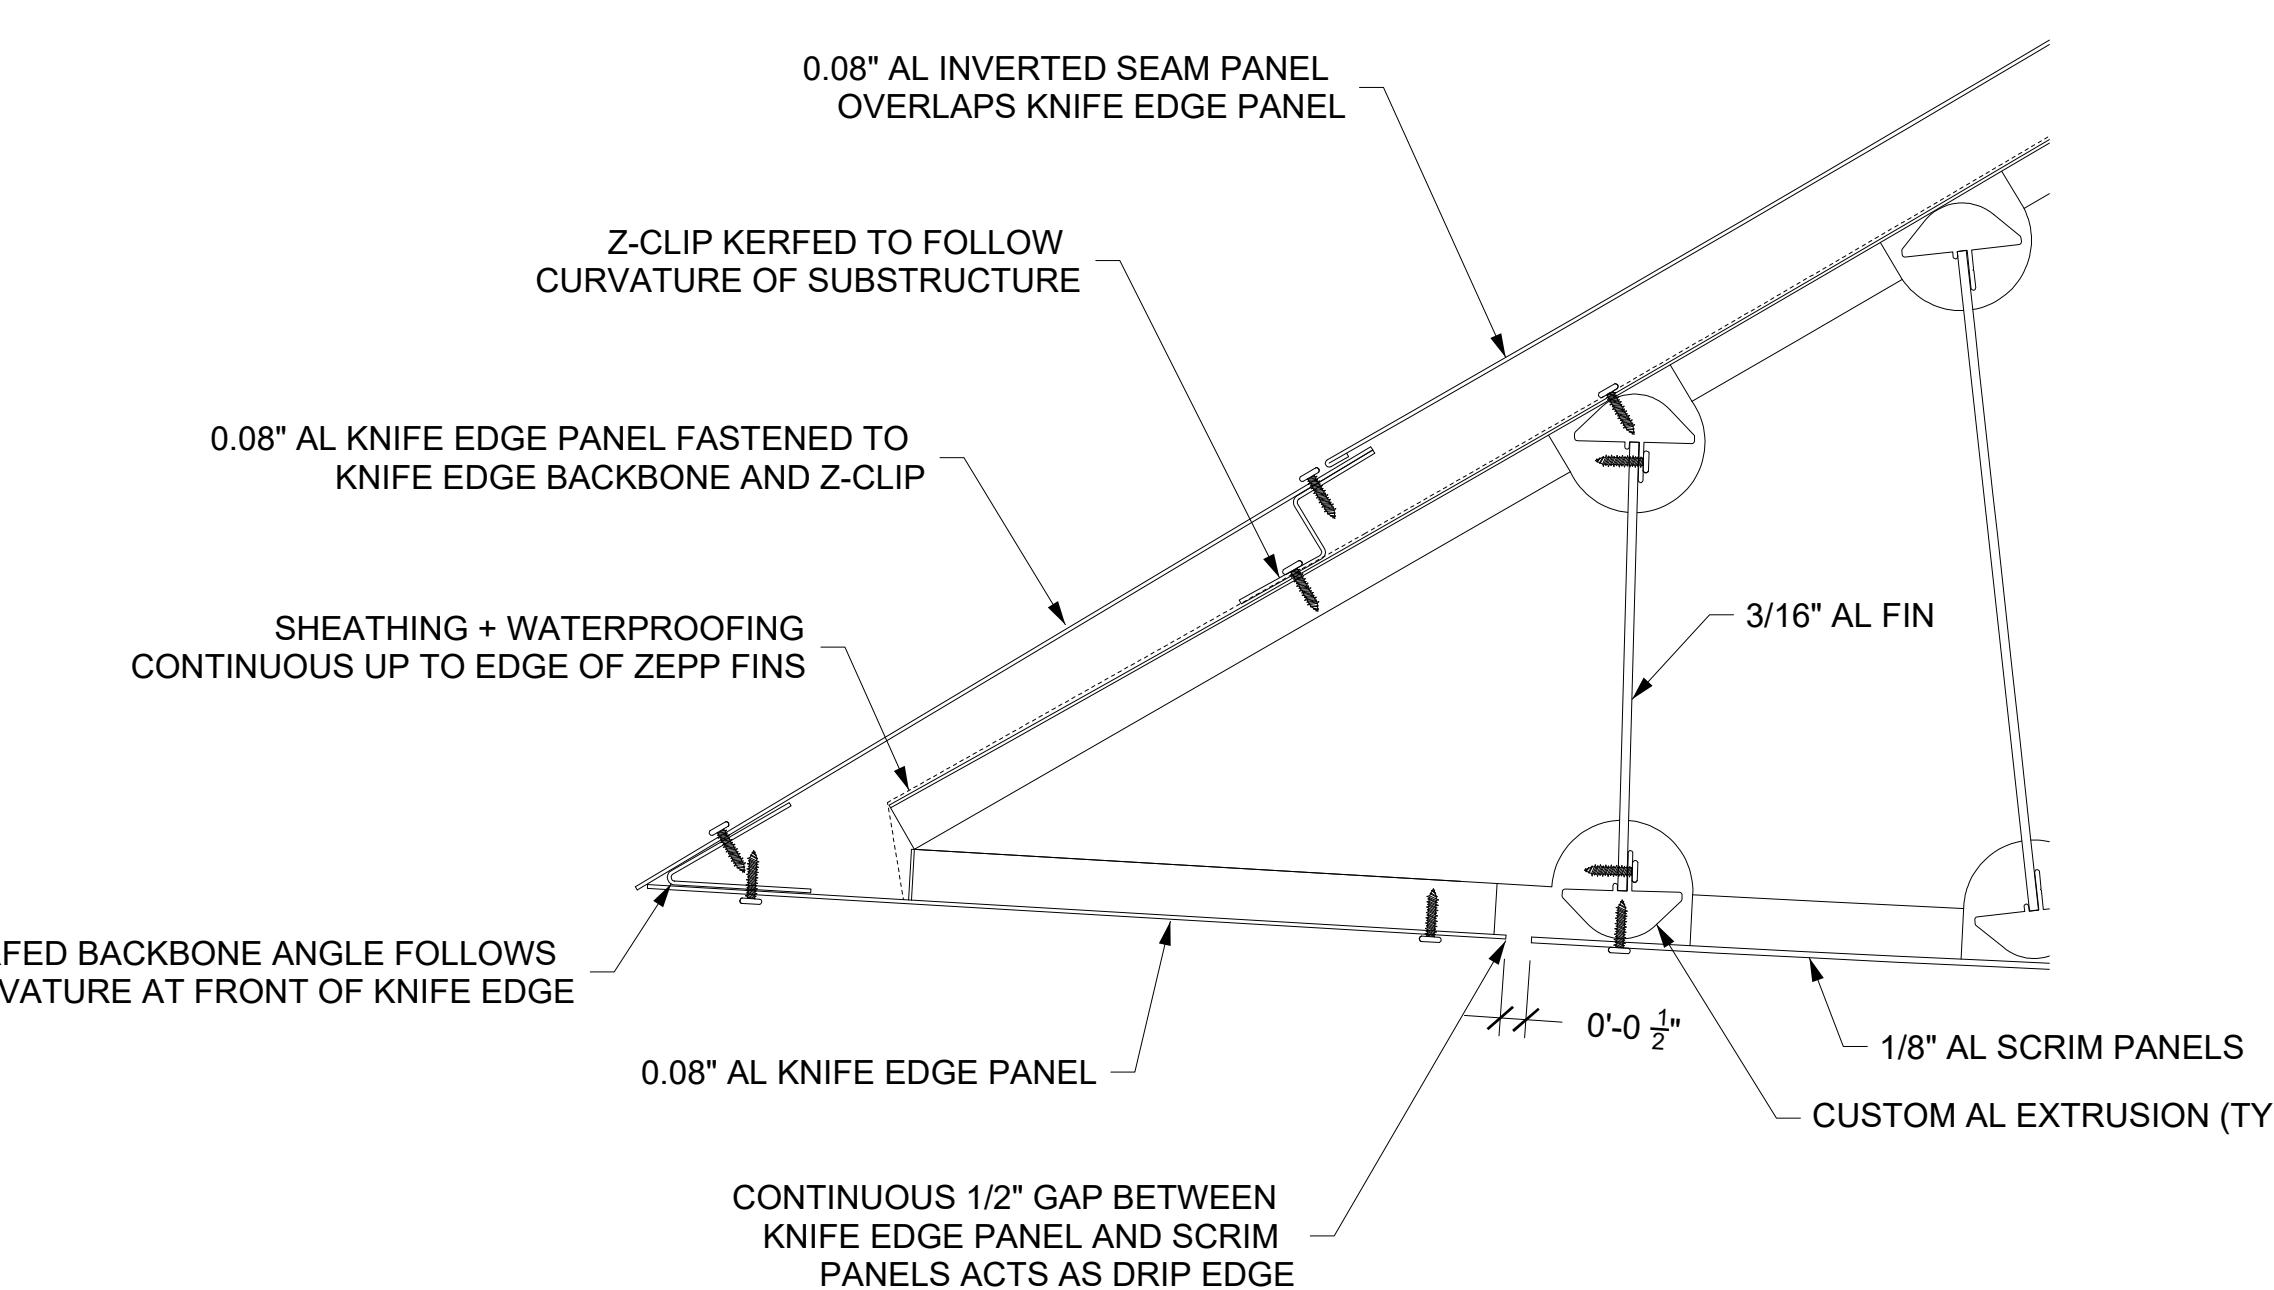

4 KNIFE EDGE DETAILS
 SCALE: 3" = 1'-0"
 ZAHNER REF: N/A
 ARCH REF: N/A

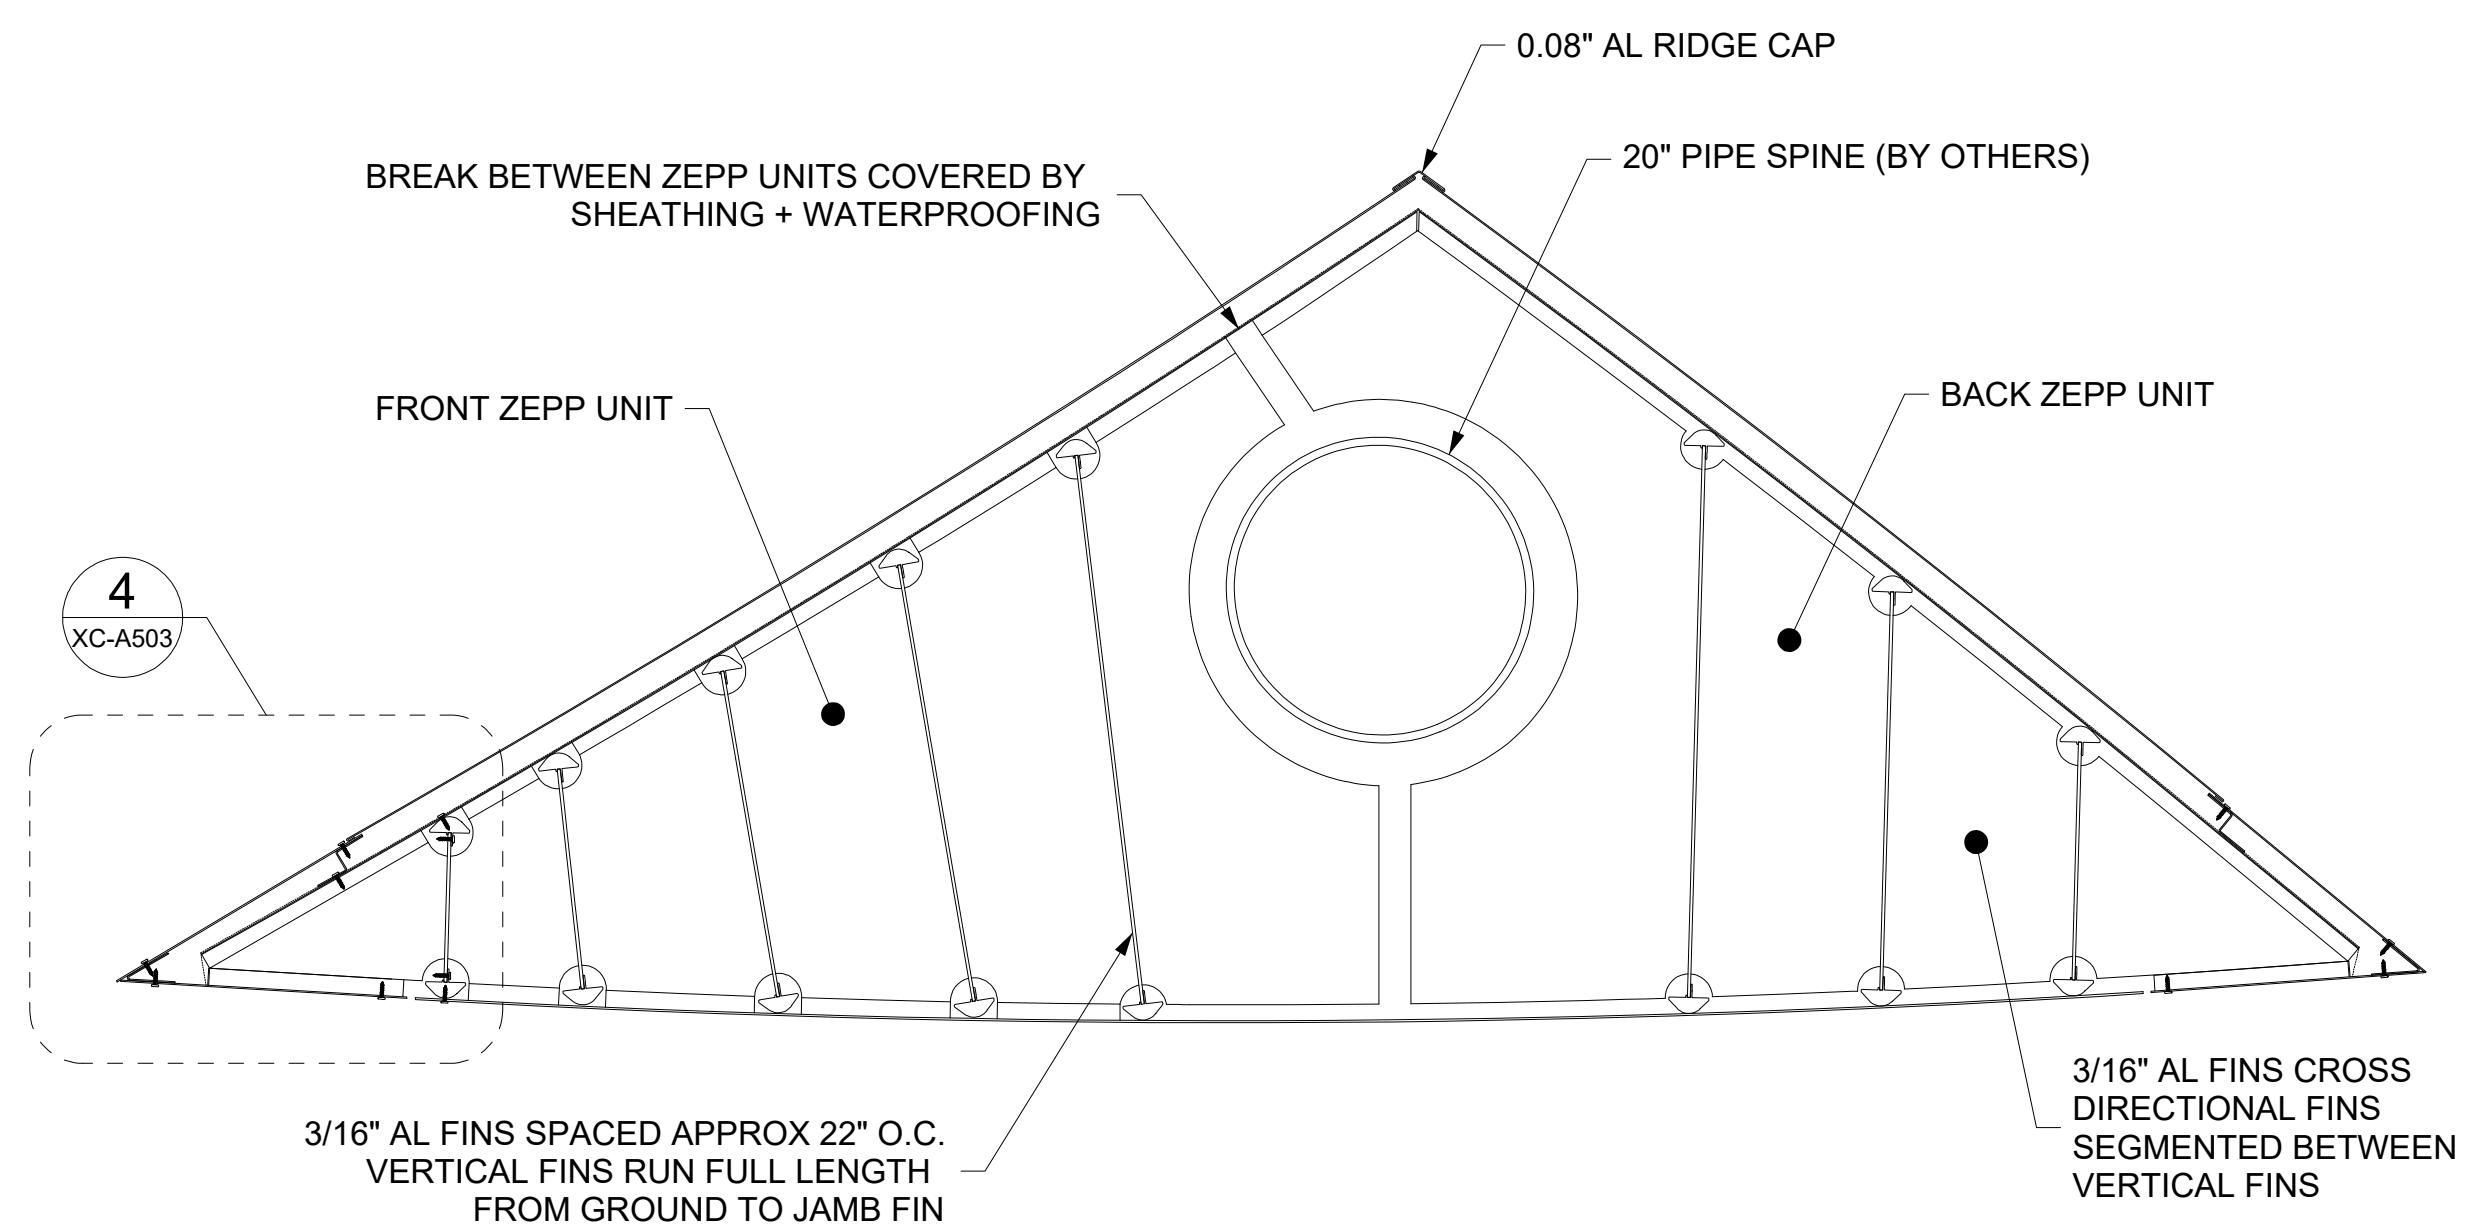

SECTION B-B
WING WALL ZEPP TYPICAL CROSS SECTION
 SCALE: ---
 ZAHNER REF: N/A
 ARCH REF: N/A




SET ISSUE DATES		
DATE	ISSUE	
01/20/22 100% DRAWINGS		
REVISIONS		
NO.	DATE	DESCRIPTION




DATE: 01/20/2022		REVISION:	BY:
ENGINEER		PUBLIC WORKS	
		CAPITAL PROJECT MANAGEMENT	
SHEET TITLE		7447 E. INDIAN SCHOOL RD. SCOTTSDALE, ARIZONA 85251	

EAST BOWL - WING WALL ZEPP DETAILS
 PROJECT TITLE: CITY OF SCOTTSDALE CIVIC CENTER PLAZA

THIS SHEET SCALED FOR 24X36" BORDER	SCALE	DESIGNED	BID NO.	XC-A503
	DRAWN DS	AS-BUILT	COS PROJECT NO.	DG04

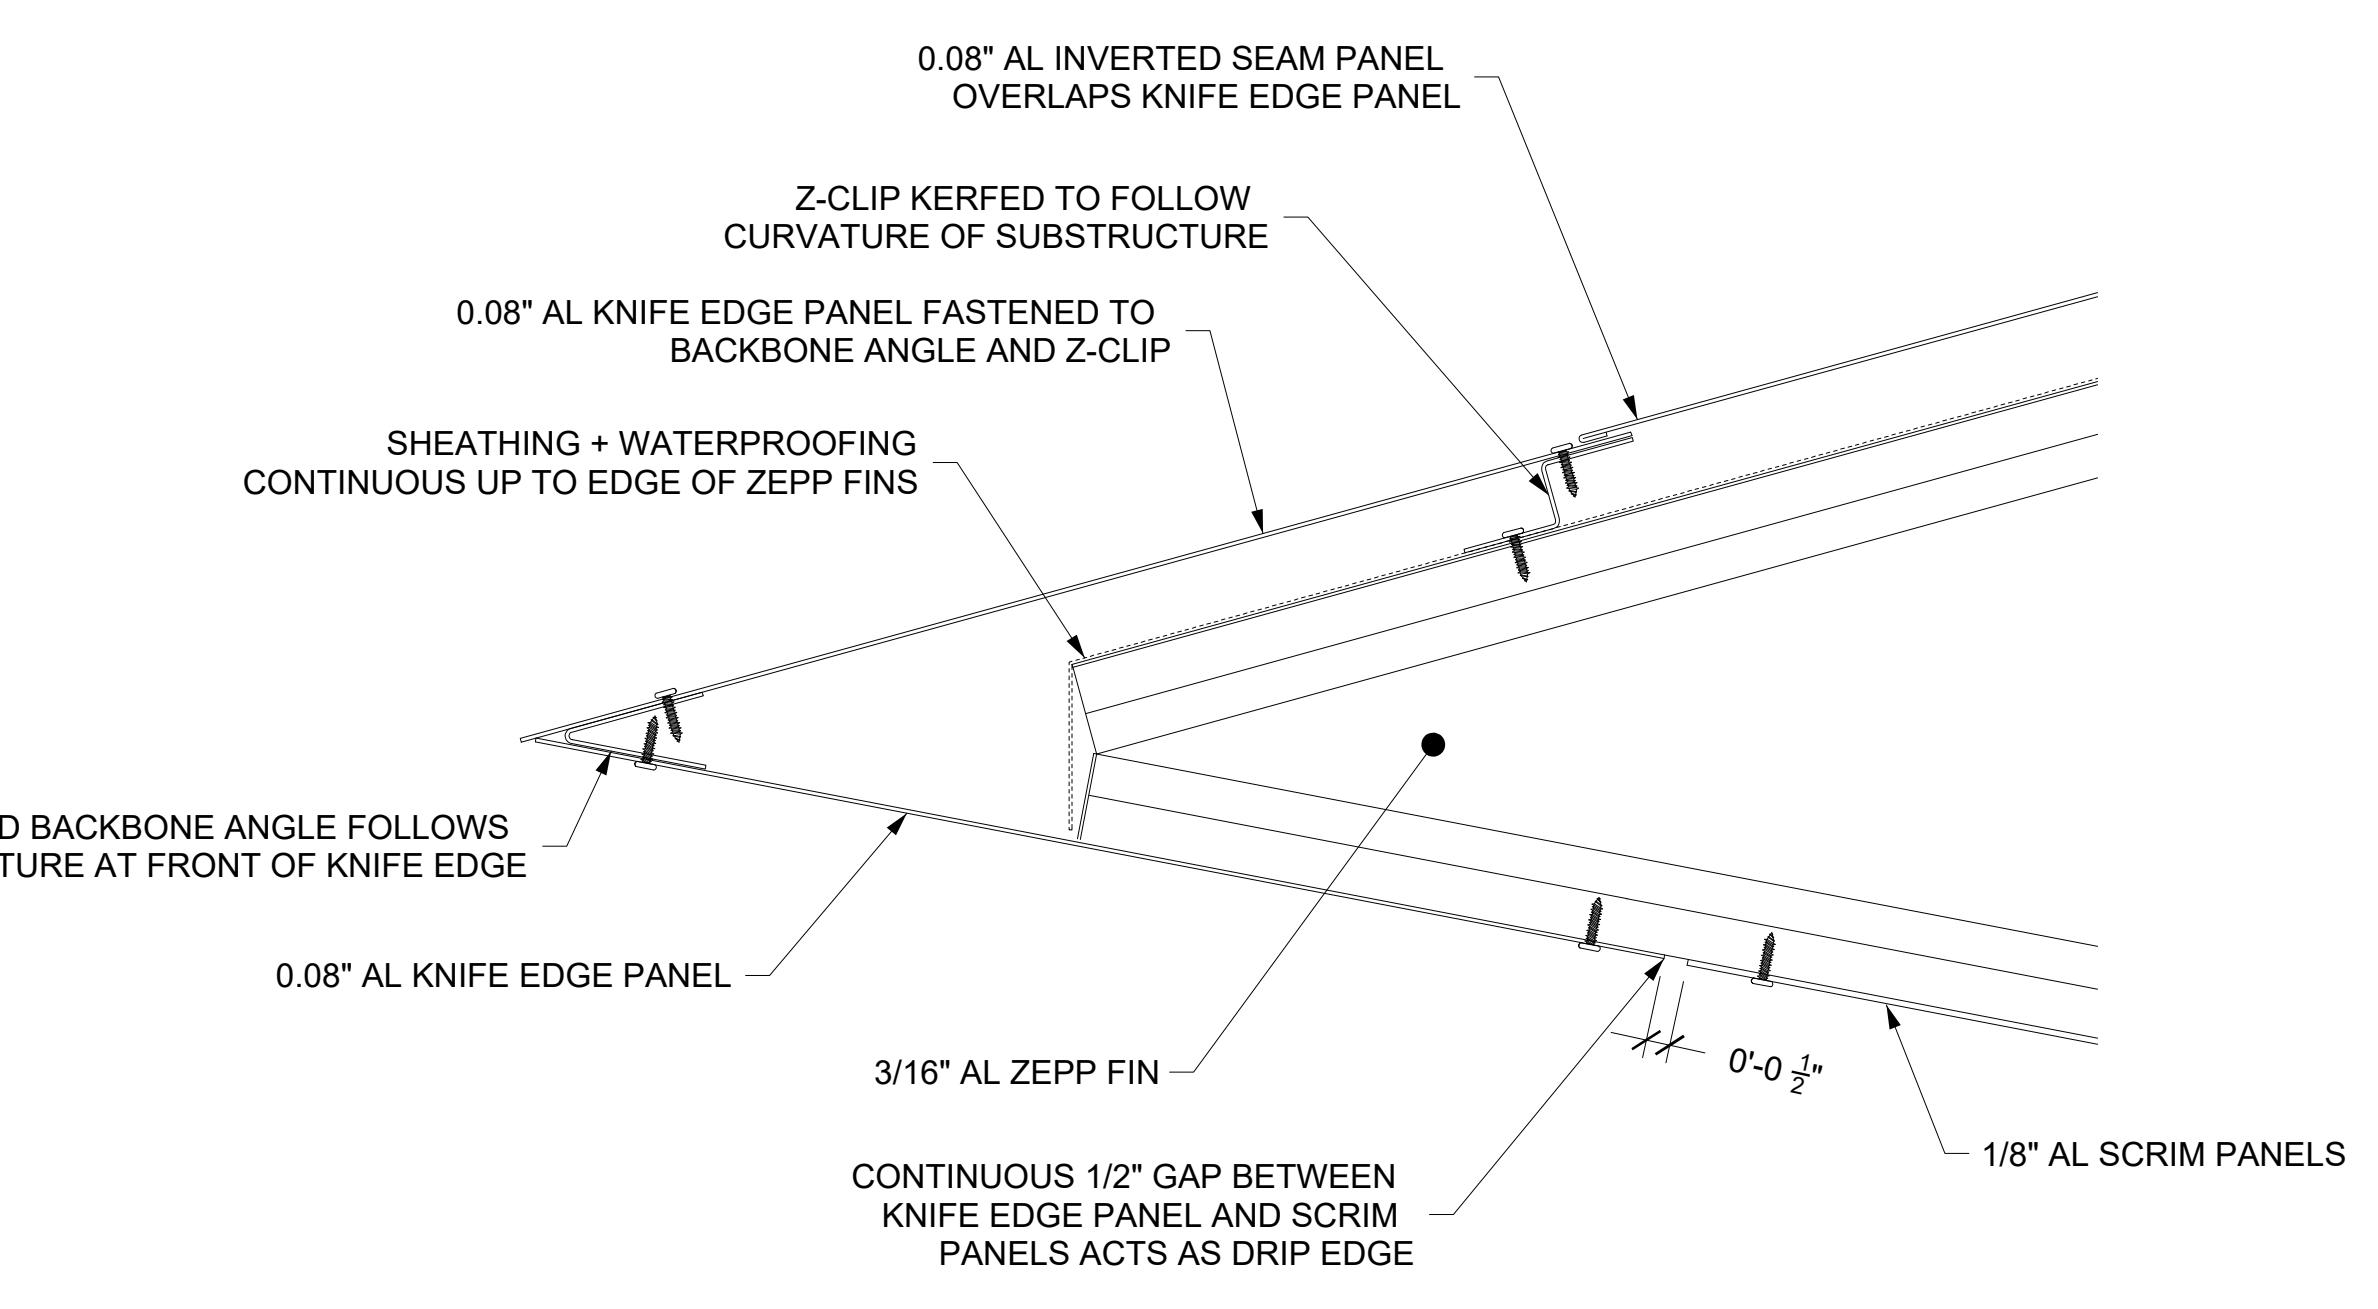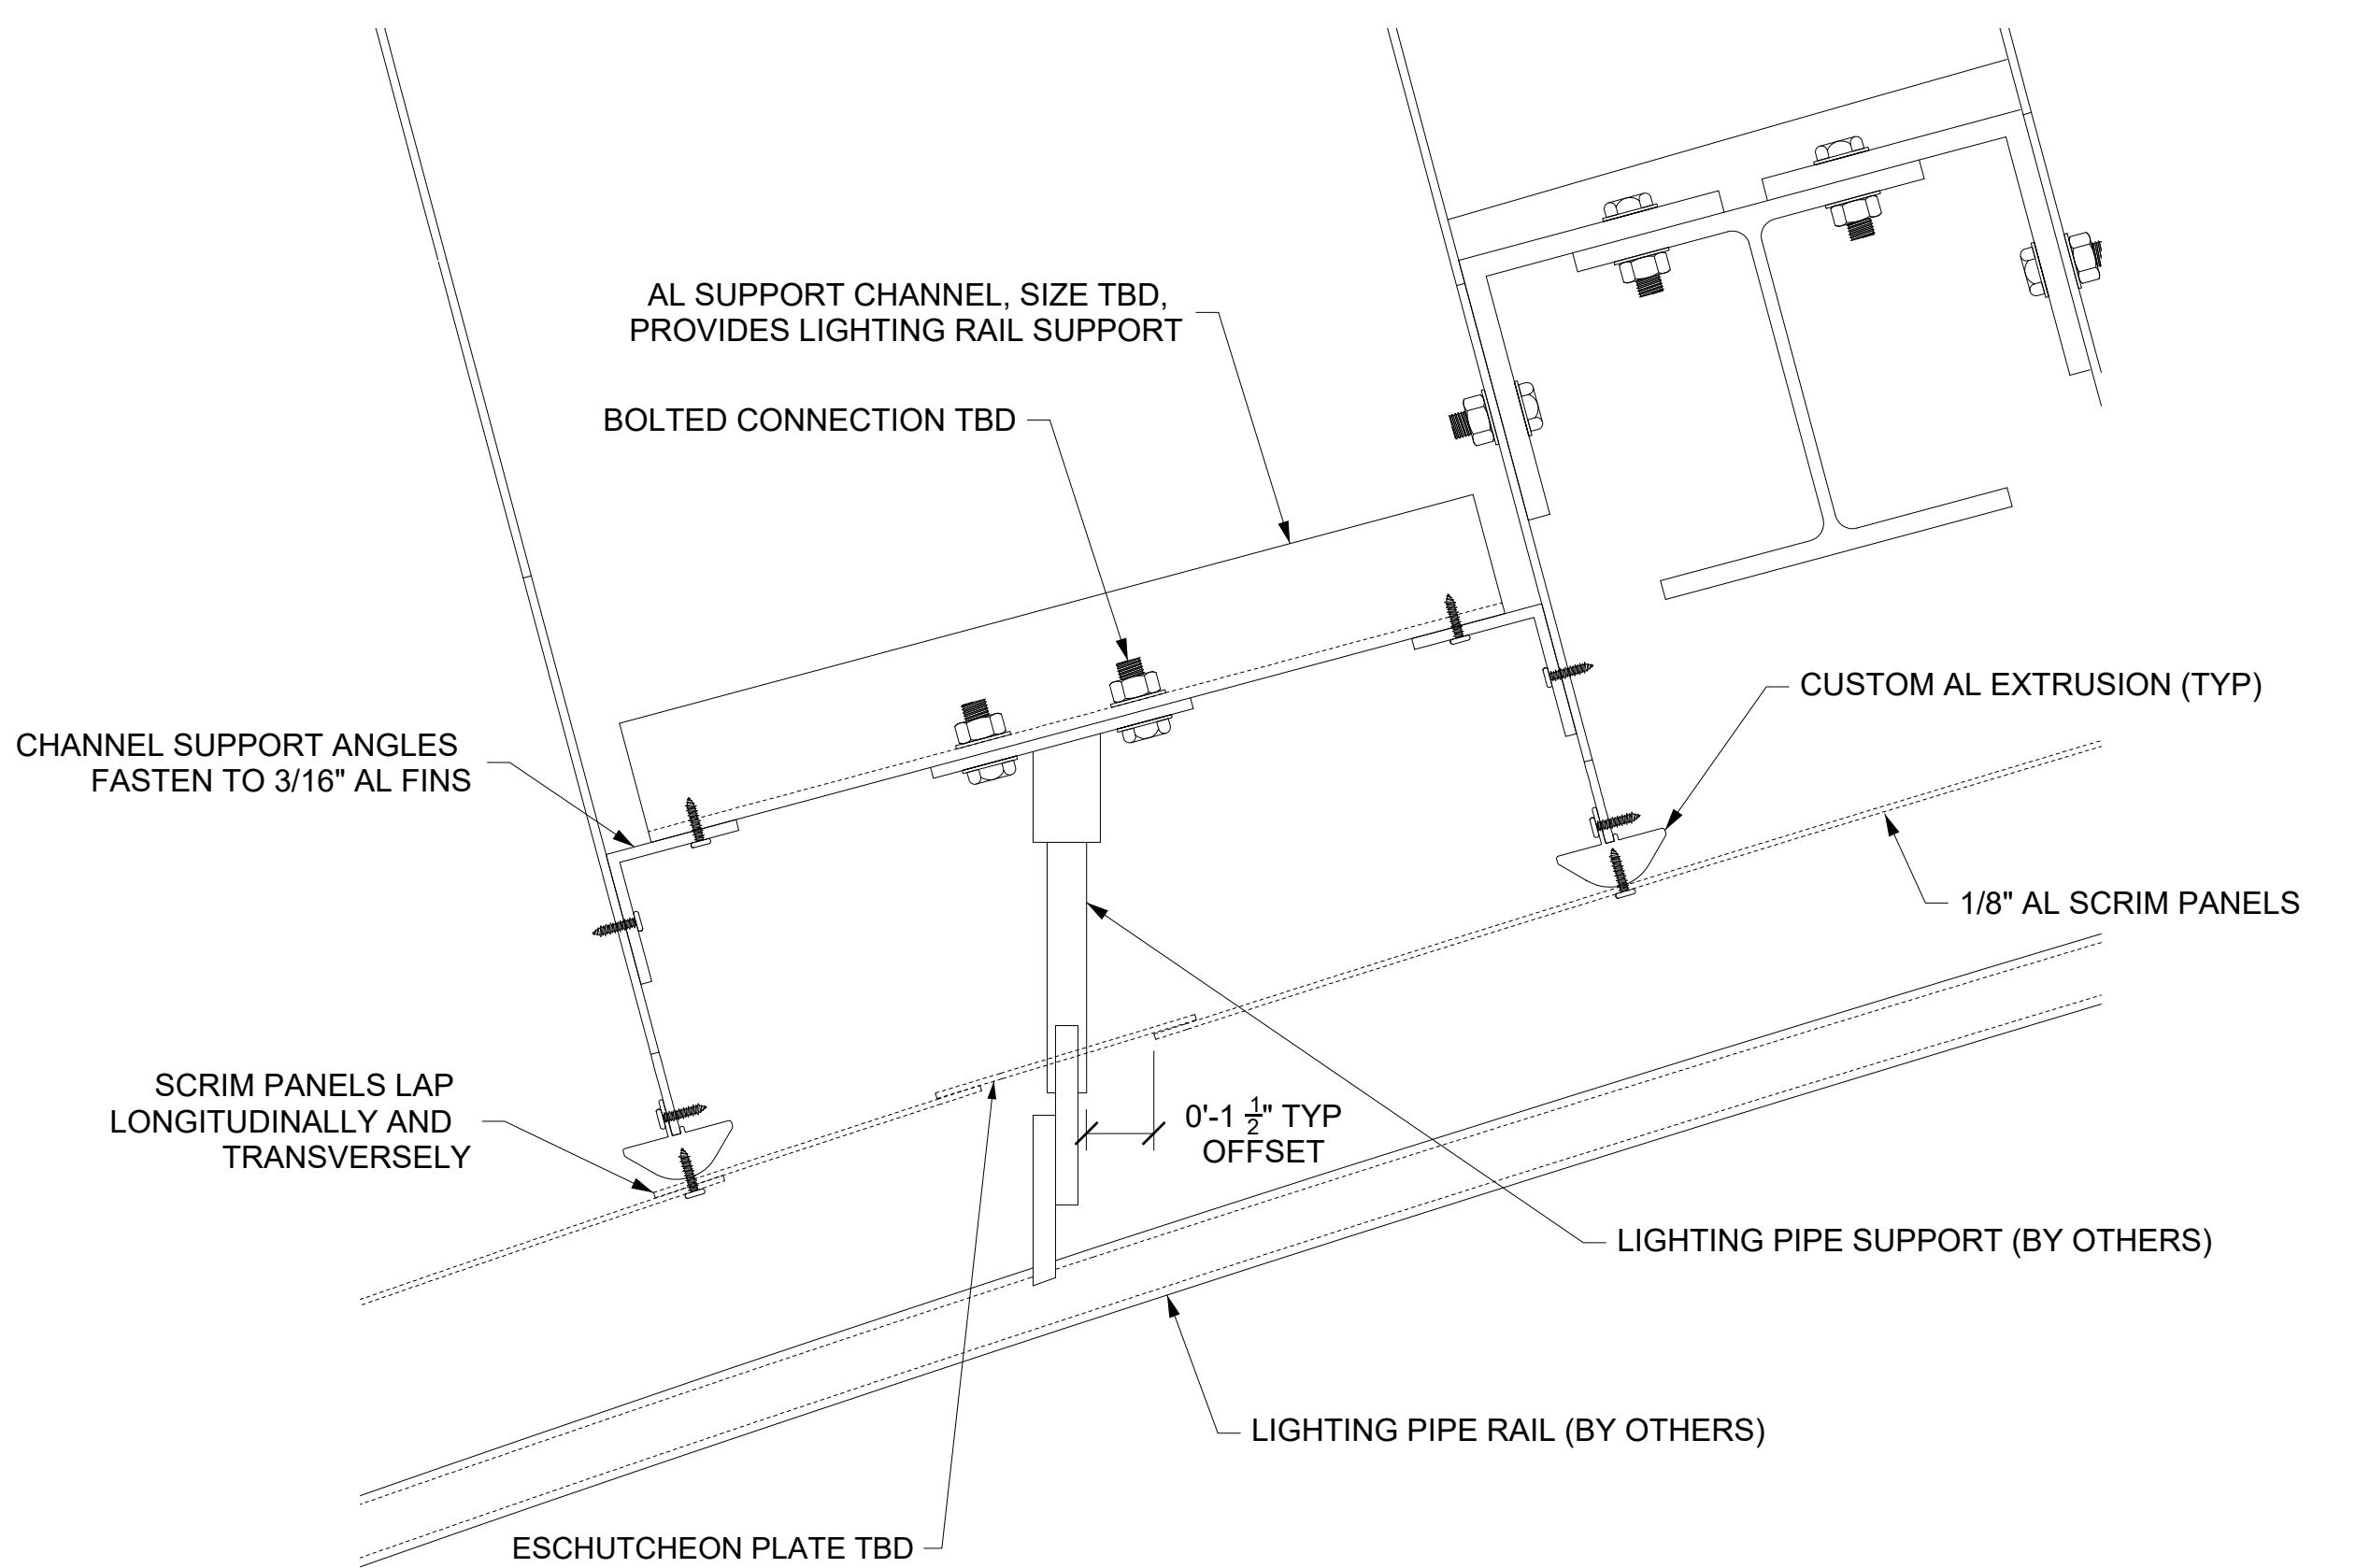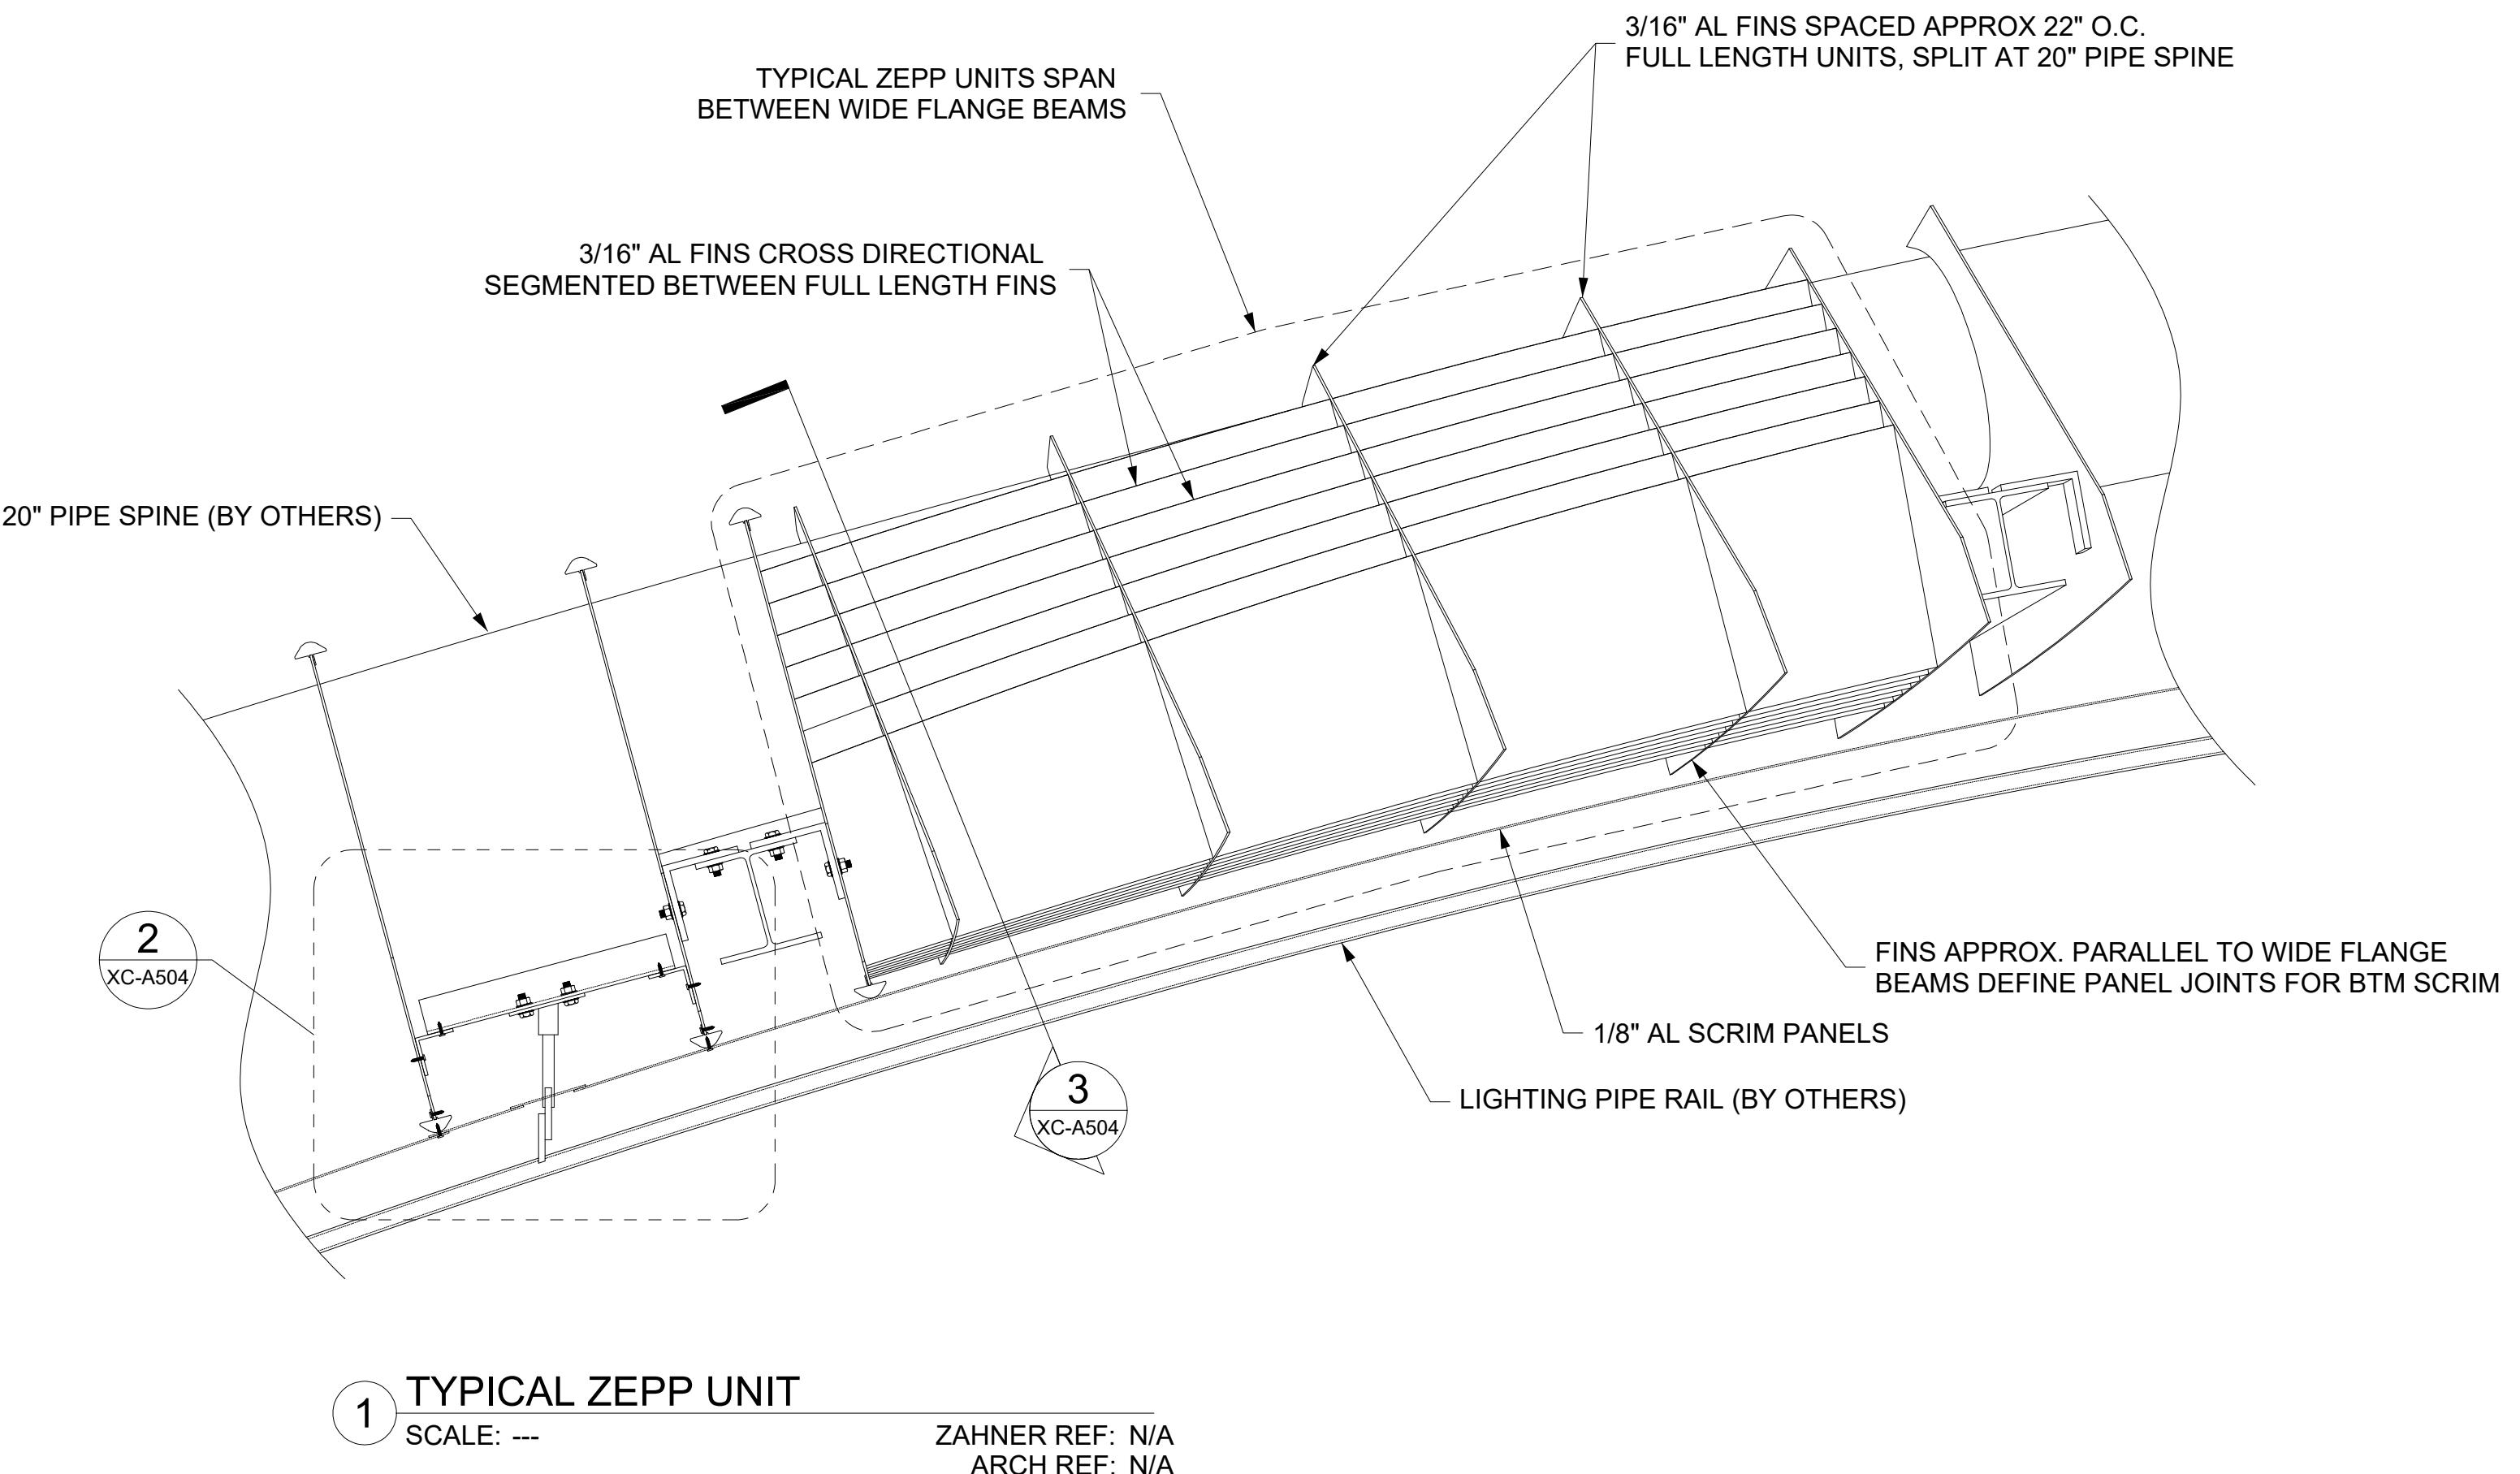


SET ISSUE DATES		
DATE	ISSUE	
01/20/22 100% DRAWINGS		
REVISIONS		
NO.	DATE	DESCRIPTION

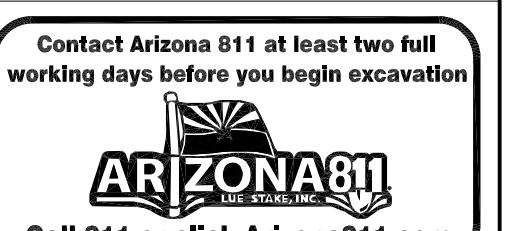

DATE: 01/20/2022	REVISION:	BY:
ENGINEER		
		PUBLIC WORKS
		CAPITAL PROJECT MANAGEMENT
7447 E. INDIAN SCHOOL RD. SCOTTSDALE, ARIZONA 85251		

EAST BOWL - TYP ZEPP DETAILS

PROJECT TITLE	CITY OF SCOTTSDALE CIVIC CENTER PLAZA		
THIS SHEET SCALED FOR 24X36" BORDER	SCALE	DESIGNED	BID NO.
	DRAWN DS	AS-BUILT	COS PROJECT NO. DG04

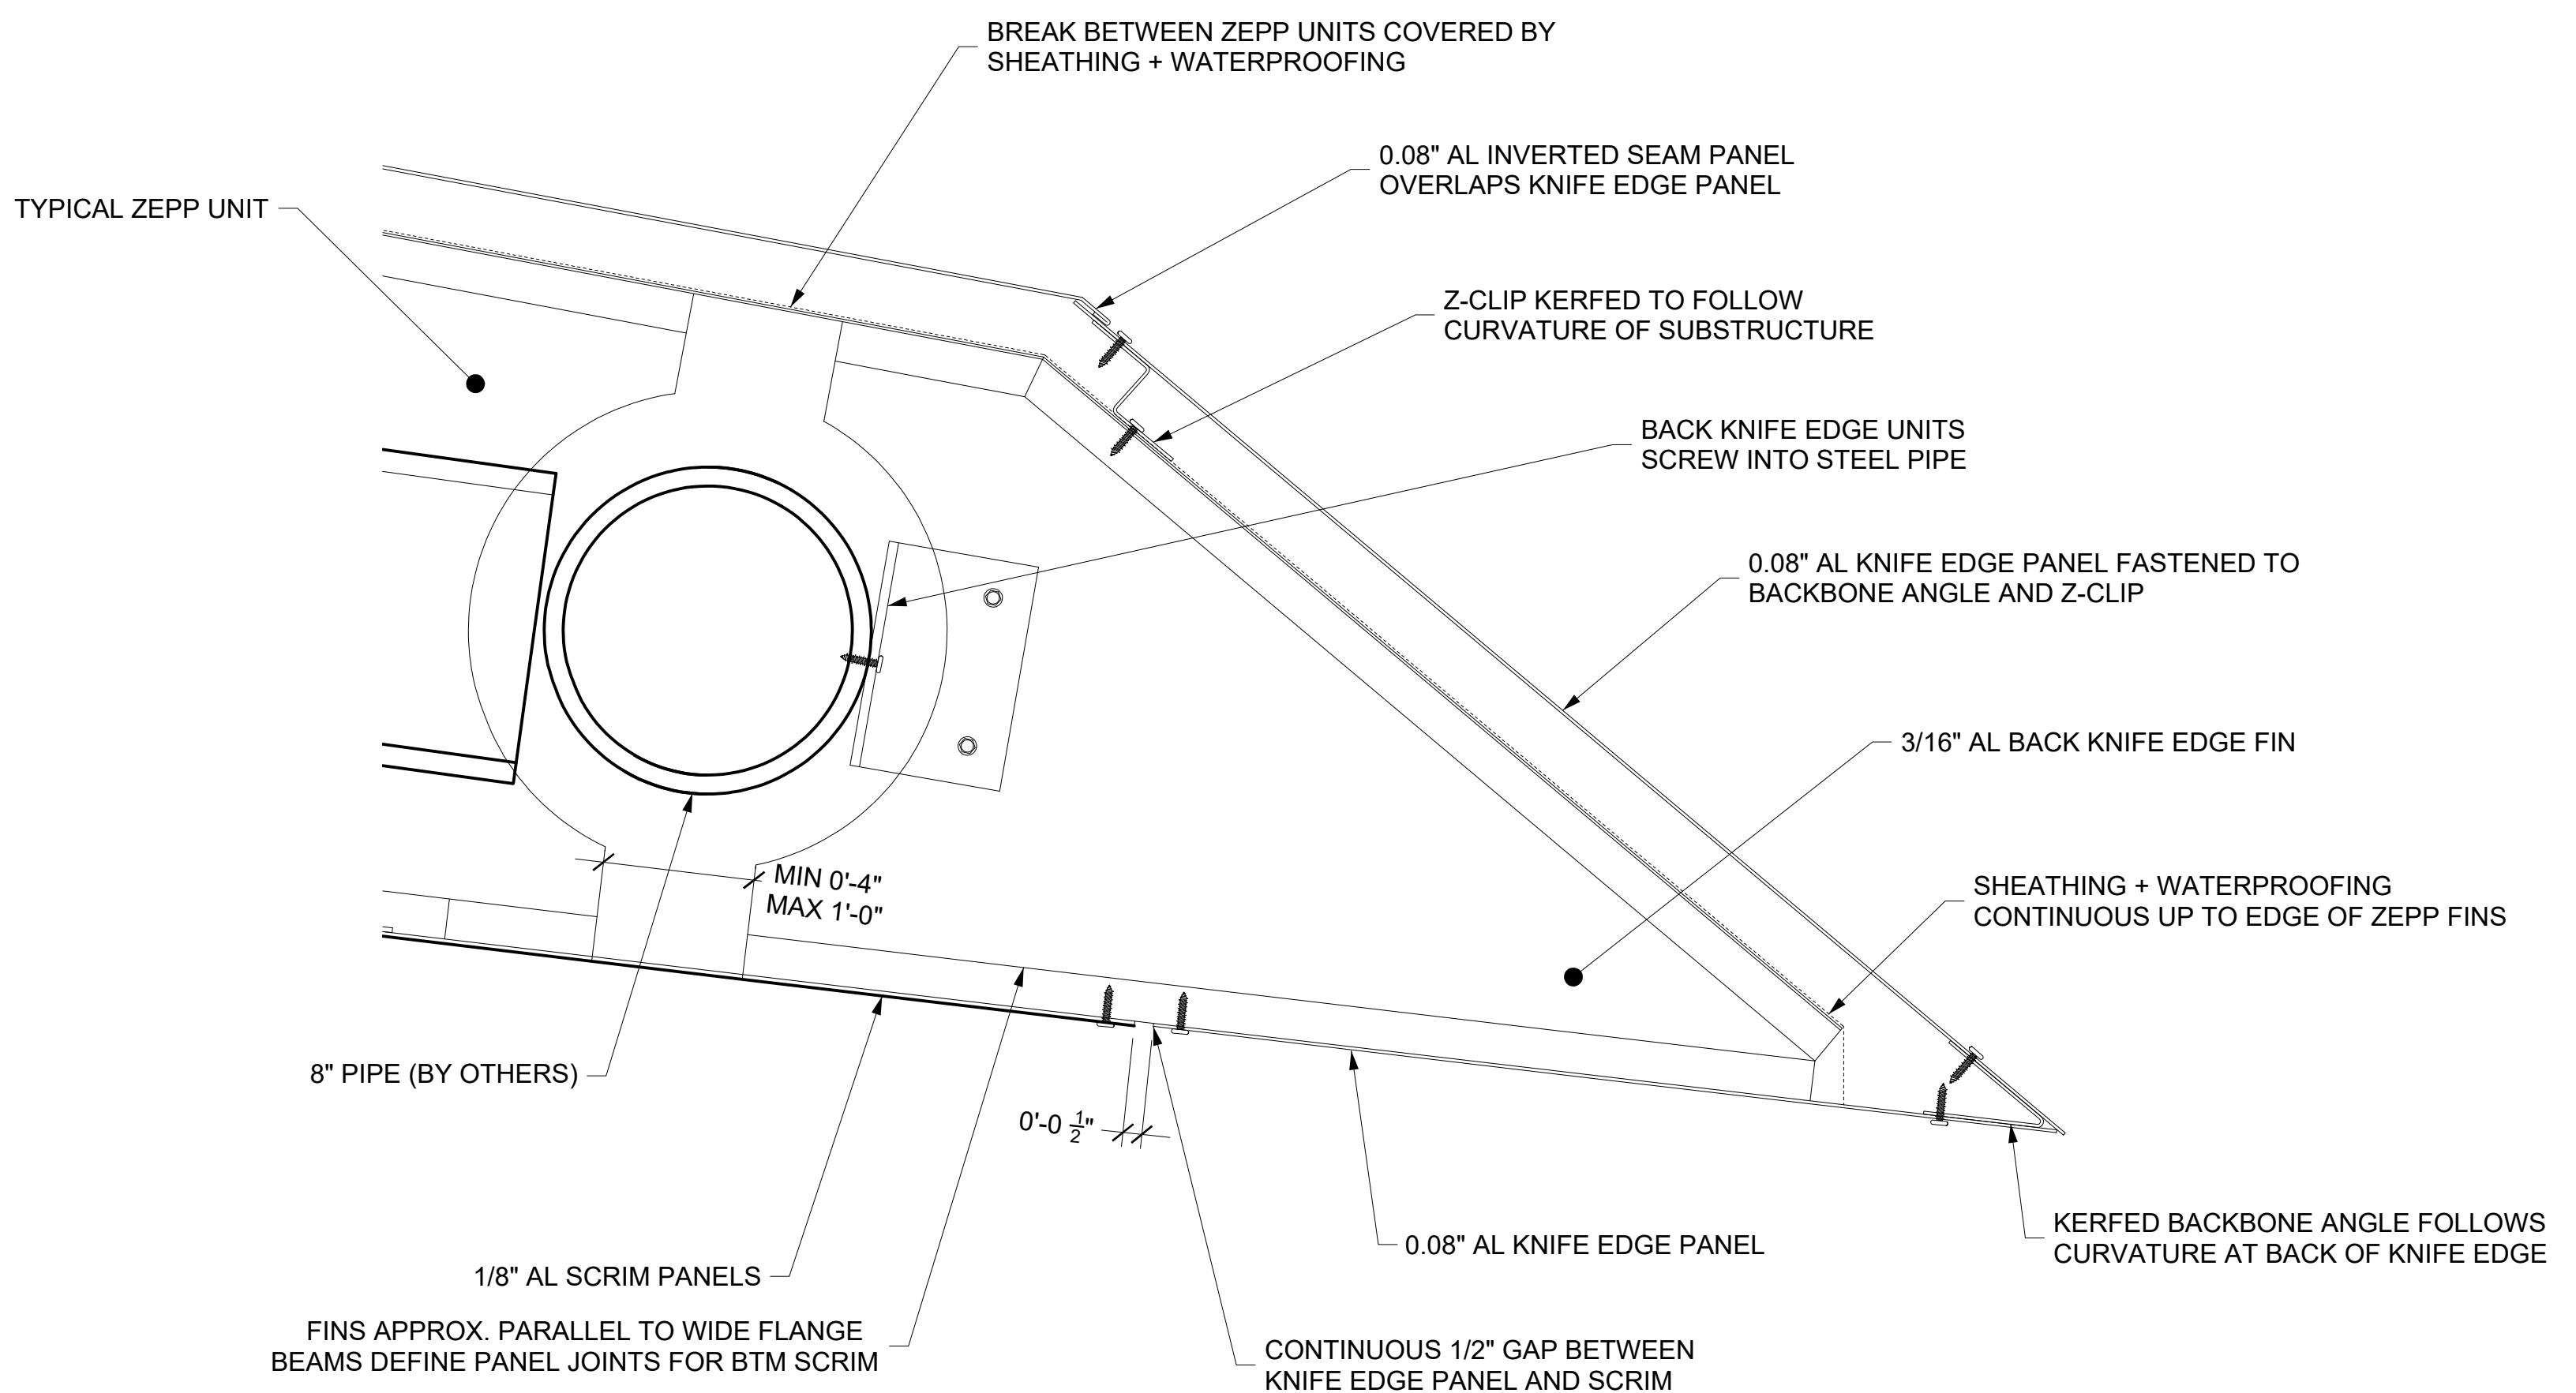

1 BACK KNIFE EDGE DETAIL

SCALE: 3' = 1'-0"

ZAHNER REF: N/A
ARCOLI REF: N/A

The logo consists of a stylized 'RPA' monogram enclosed in a square frame. The letters are bold and have a geometric, hatched texture. To the right of the monogram, the company name 'RITOCH-POWELL & Associates' is written in a large, sans-serif font. Below the name is the phone number '602-263-1177' and the website 'WWW.RPAENG.COM'. The entire logo is set against a white background.

L A K E | F L A T O


© 2021 Lake|Flato Architects, Inc.

311 THIRD STREET
SAN ANTONIO, TEXAS 78205
P 210.227.3335 F 210.224.9515
www.lakeflato.com

ZAHNER

ARCHITECTURAL METAL

REVISIONS

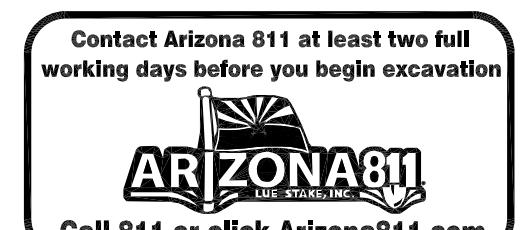


DATE 01/09/2000 | REVISION

DATE: 01/20/2022	REVISION:	BY:
ENGINEER		
		
		PUBLIC WORKS CAPITAL PROJECT MANAGEMENT
7447 E. INDIAN SCHOOL RD. SCOTTSDALE, ARIZONA 85251		

EAST BOWL - BACK KNIFE EDGE DETAIL

PROJECT TITLE	CITY OF SCOTTSDALE CIVIC CENTER PLAZA
---------------	--


THIS SHEET SCALED FOR 24X36" BORDER	SCALE	DESIGNED		BID NO.	XC-A505
		DRAWN DS	AS-BUILT	COS PROJECT NO. DG04	

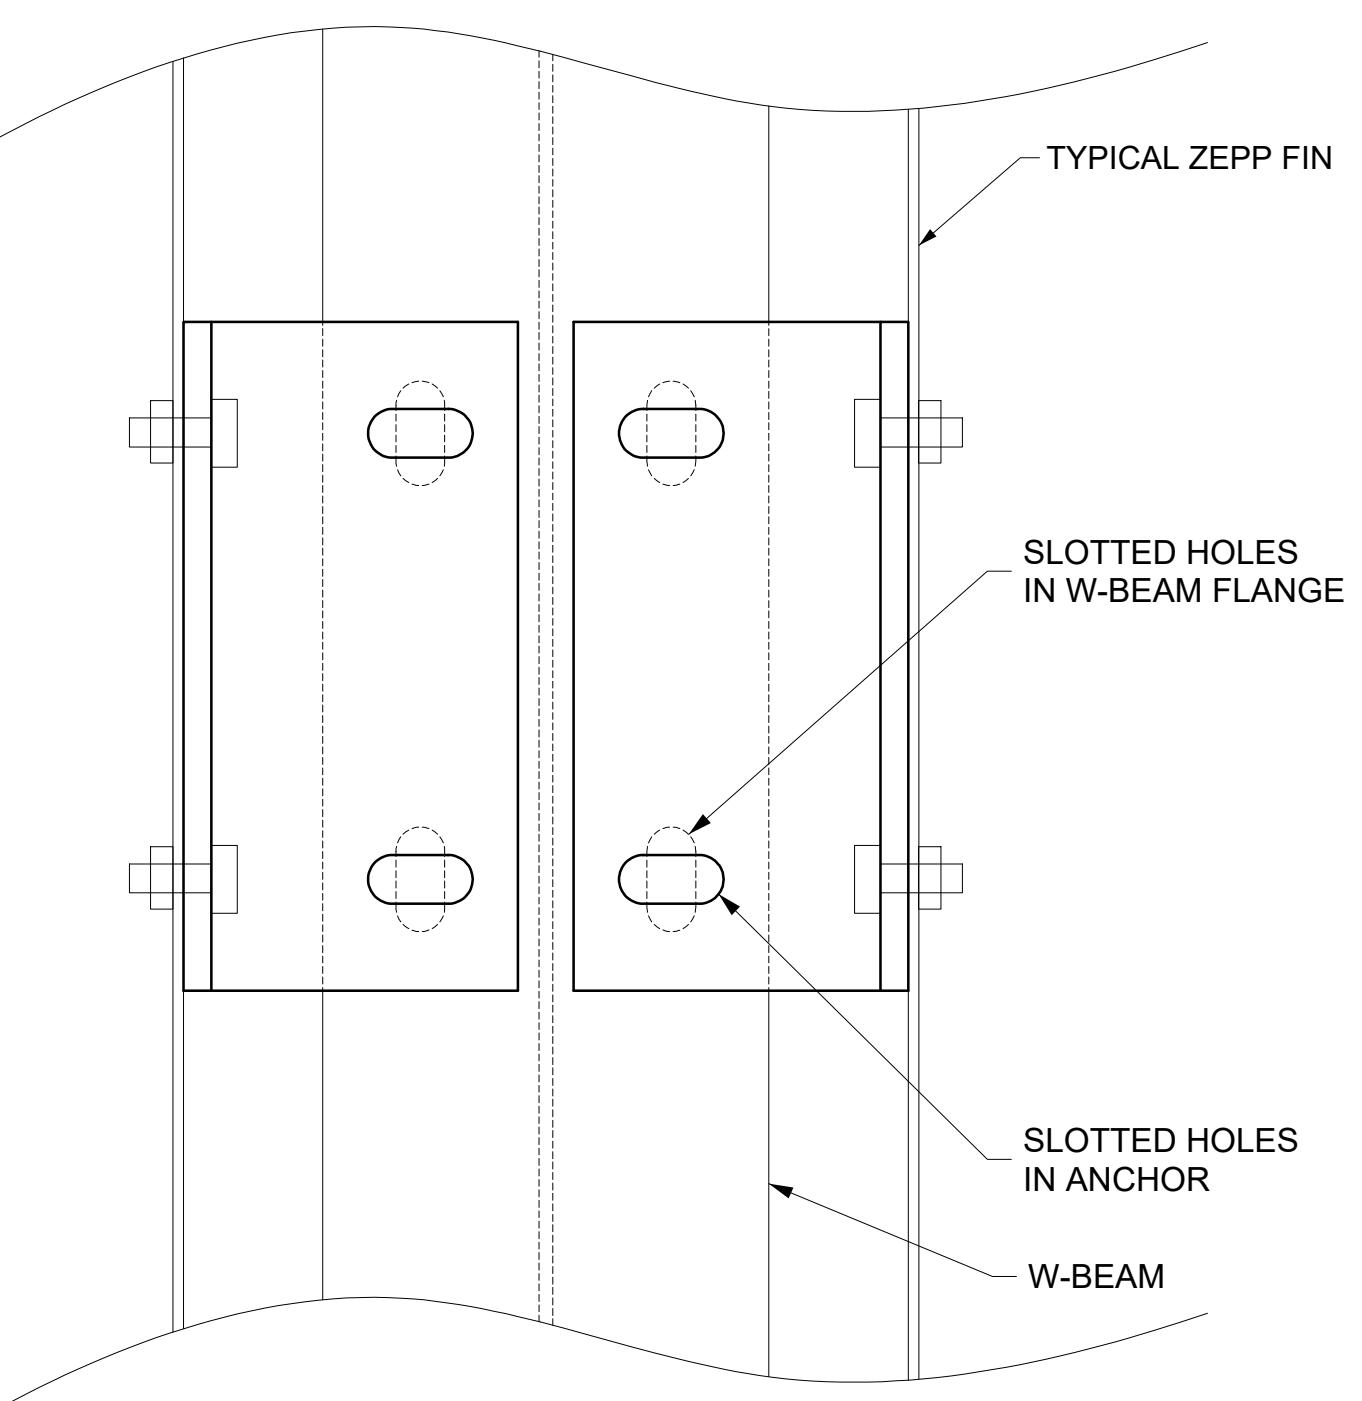

2 SECTION A-A
SCALE: ---

SCALE: --

ZAHNER REF: N/A
ARCH REF: N/A

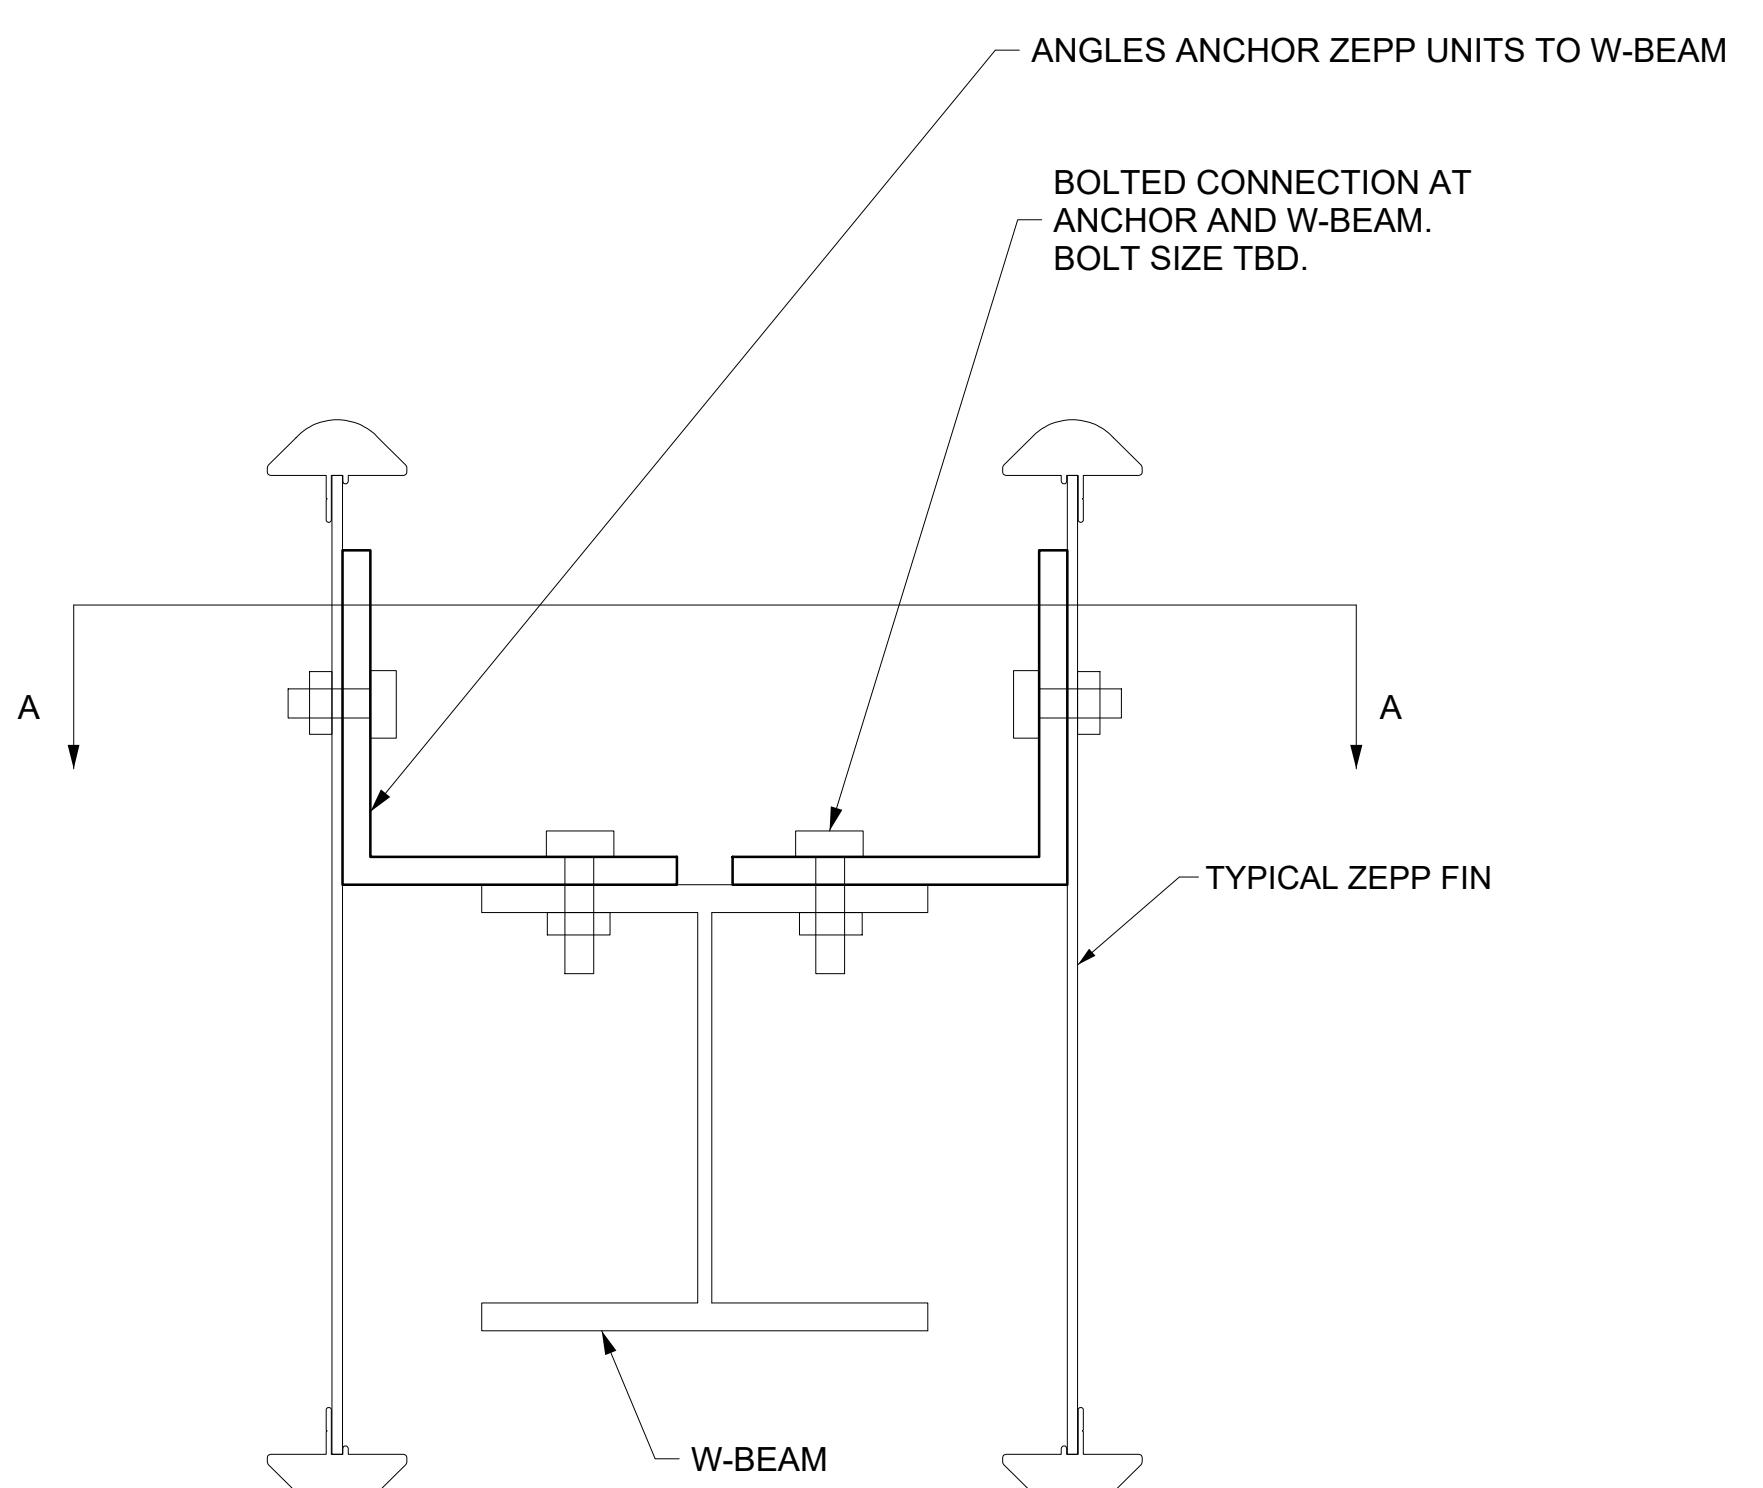


2 ANCHOR DETAIL

(2) ANSWER
SCALE:


ZAHNER REF: N/A
ARCH REF: N/A

SET ISSUE DATES					
DATE	ISSUE				
01/20/22 100% DRAWINGS					
<hr/> <hr/> <hr/> <hr/> <hr/>					
REVISIONS					
NO.	DATE	DESCRIPTION			
		<hr/> <hr/> <hr/> <hr/> <hr/>			
<div style="border: 1px solid black; padding: 10px; text-align: center;"> <p>Contact Arizona 811 at least two full working days before you begin excavation</p>  <p>Call 811 or click Arizona811.com</p> </div>					
DATE: 01/20/2022		REVISION:		BY:	
ENGINEER		 <div style="display: flex; justify-content: space-between;"> <p>PUBLIC WORKS</p> <p>CAPITAL PROJECT MANAGEMENT</p> </div> <p>7447 E. INDIAN SCHOOL RD. SCOTTSDALE, ARIZONA 85251</p>			
SHEET TITLE					
EAST BOWL - ANCHOR DETAILS					
PROJECT TITLE		CITY OF SCOTTSDALE CIVIC CENTER PLAZA			
D R	SCALE	DESIGNED		BID NO.	XC-A506
		DRAWN DS	AS-BUILT	COS PROJECT NO. DG04	

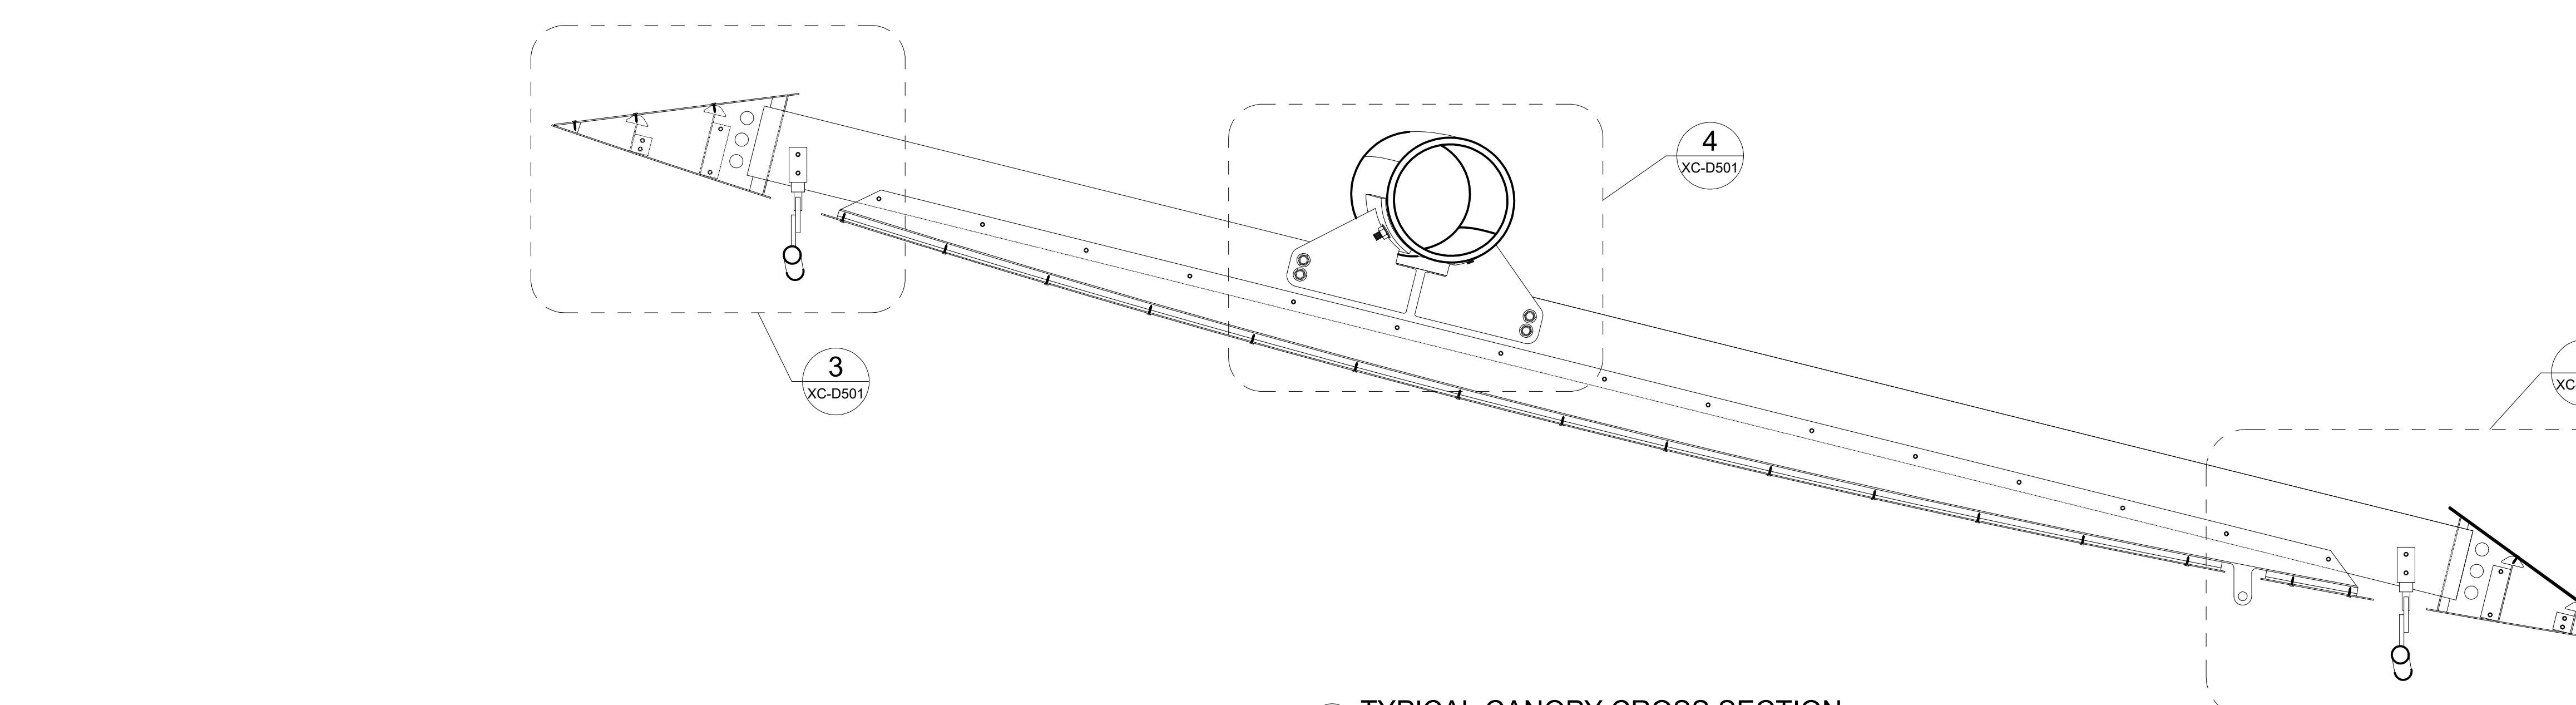


1 TYPICAL CANOPY CROSS SECTION

SCALE: 1" = 1'-0"
ZAHNER REF: N/A
ARCH REF: N/A

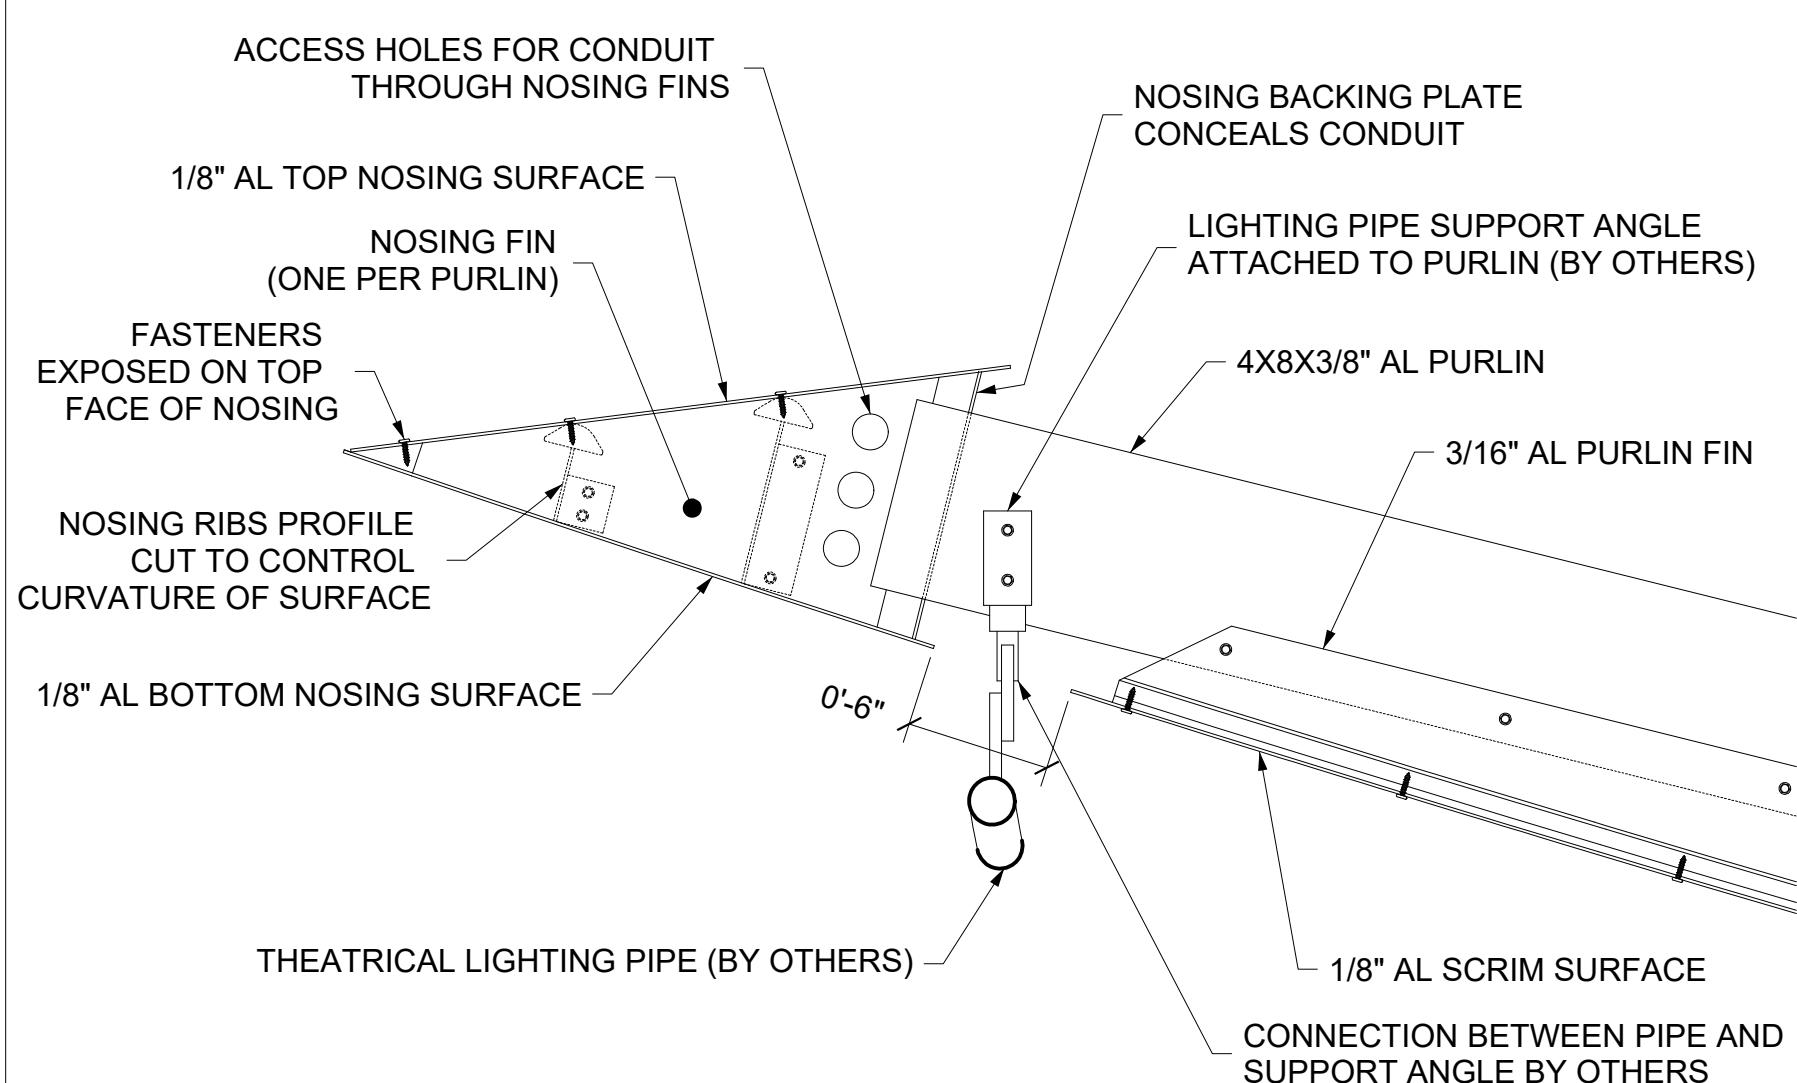


3 OUTSIDE NOSING DETAIL

SCALE: 1" = 1'-0"
ZAHNER REF: N/A
ARCH REF: N/A

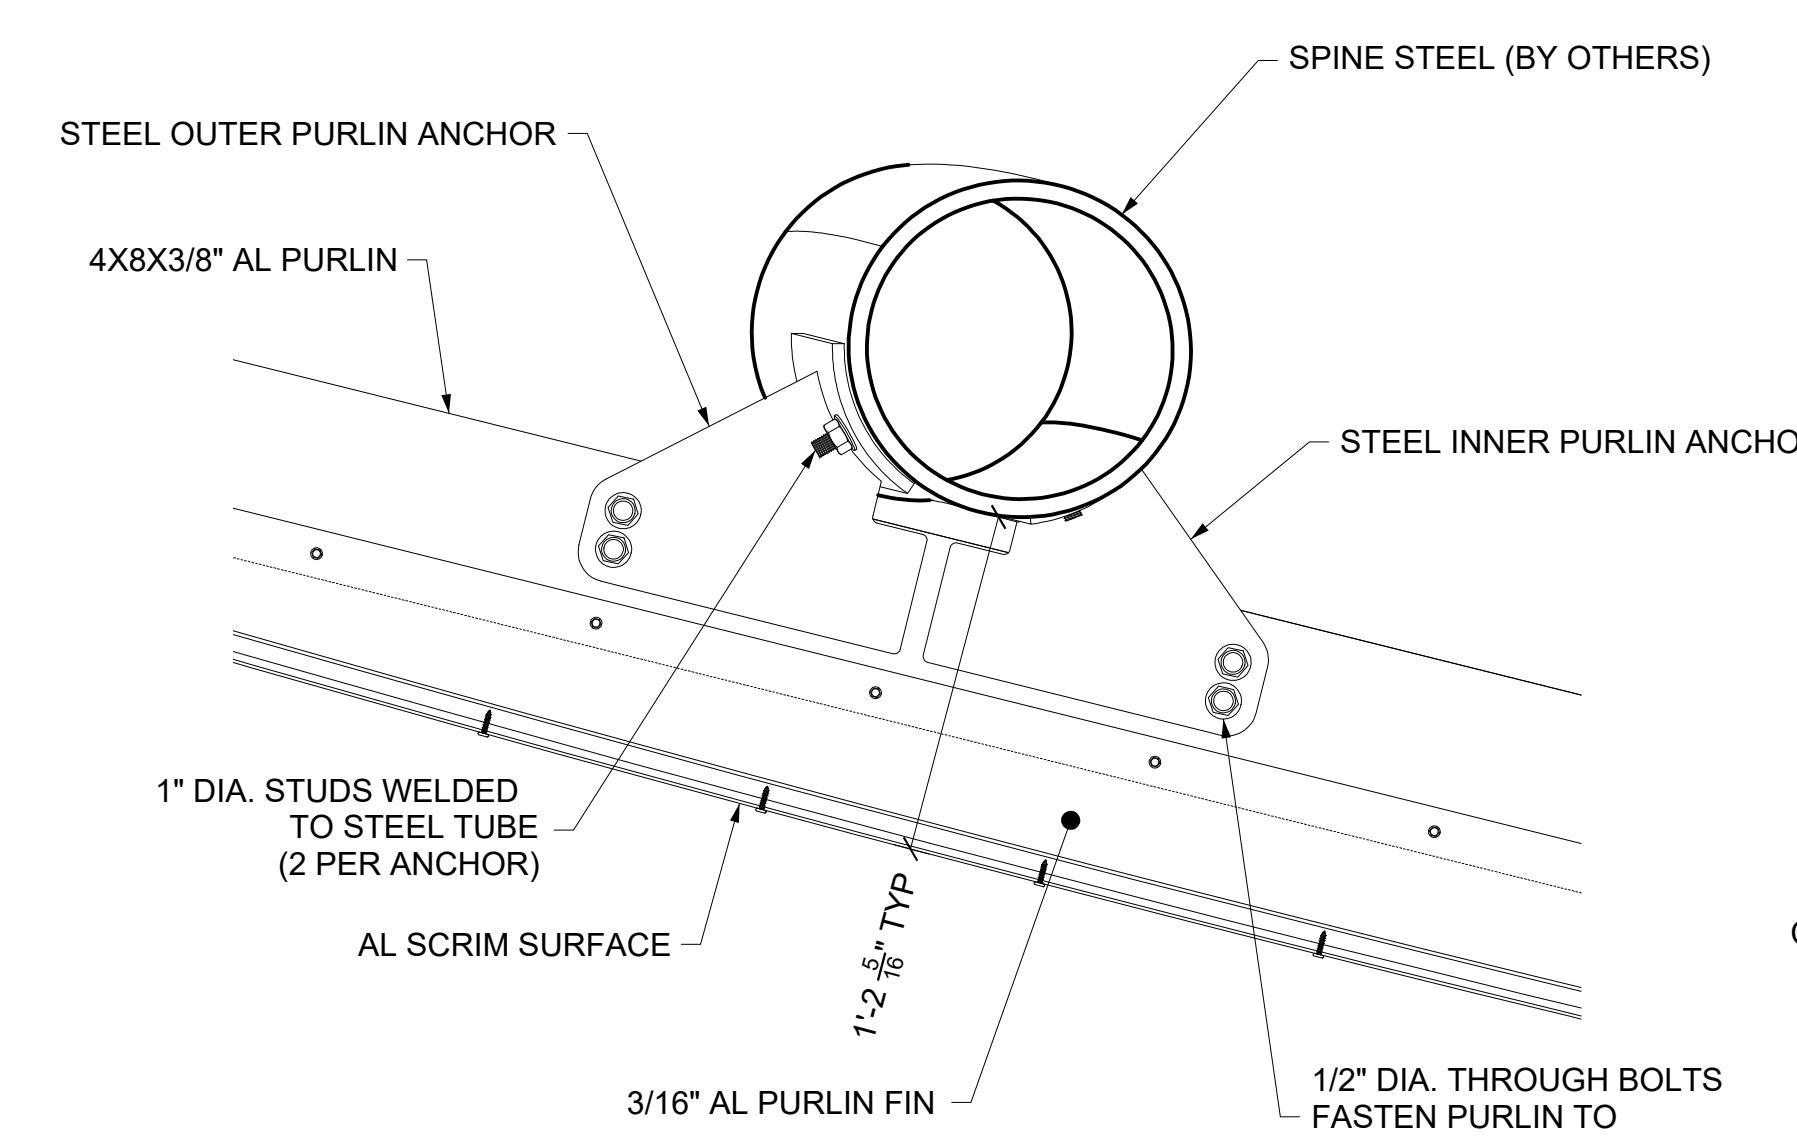


4 ANCHOR DETAIL

SCALE: 1" = 1'-0"
ZAHNER REF: N/A
ARCH REF: N/A

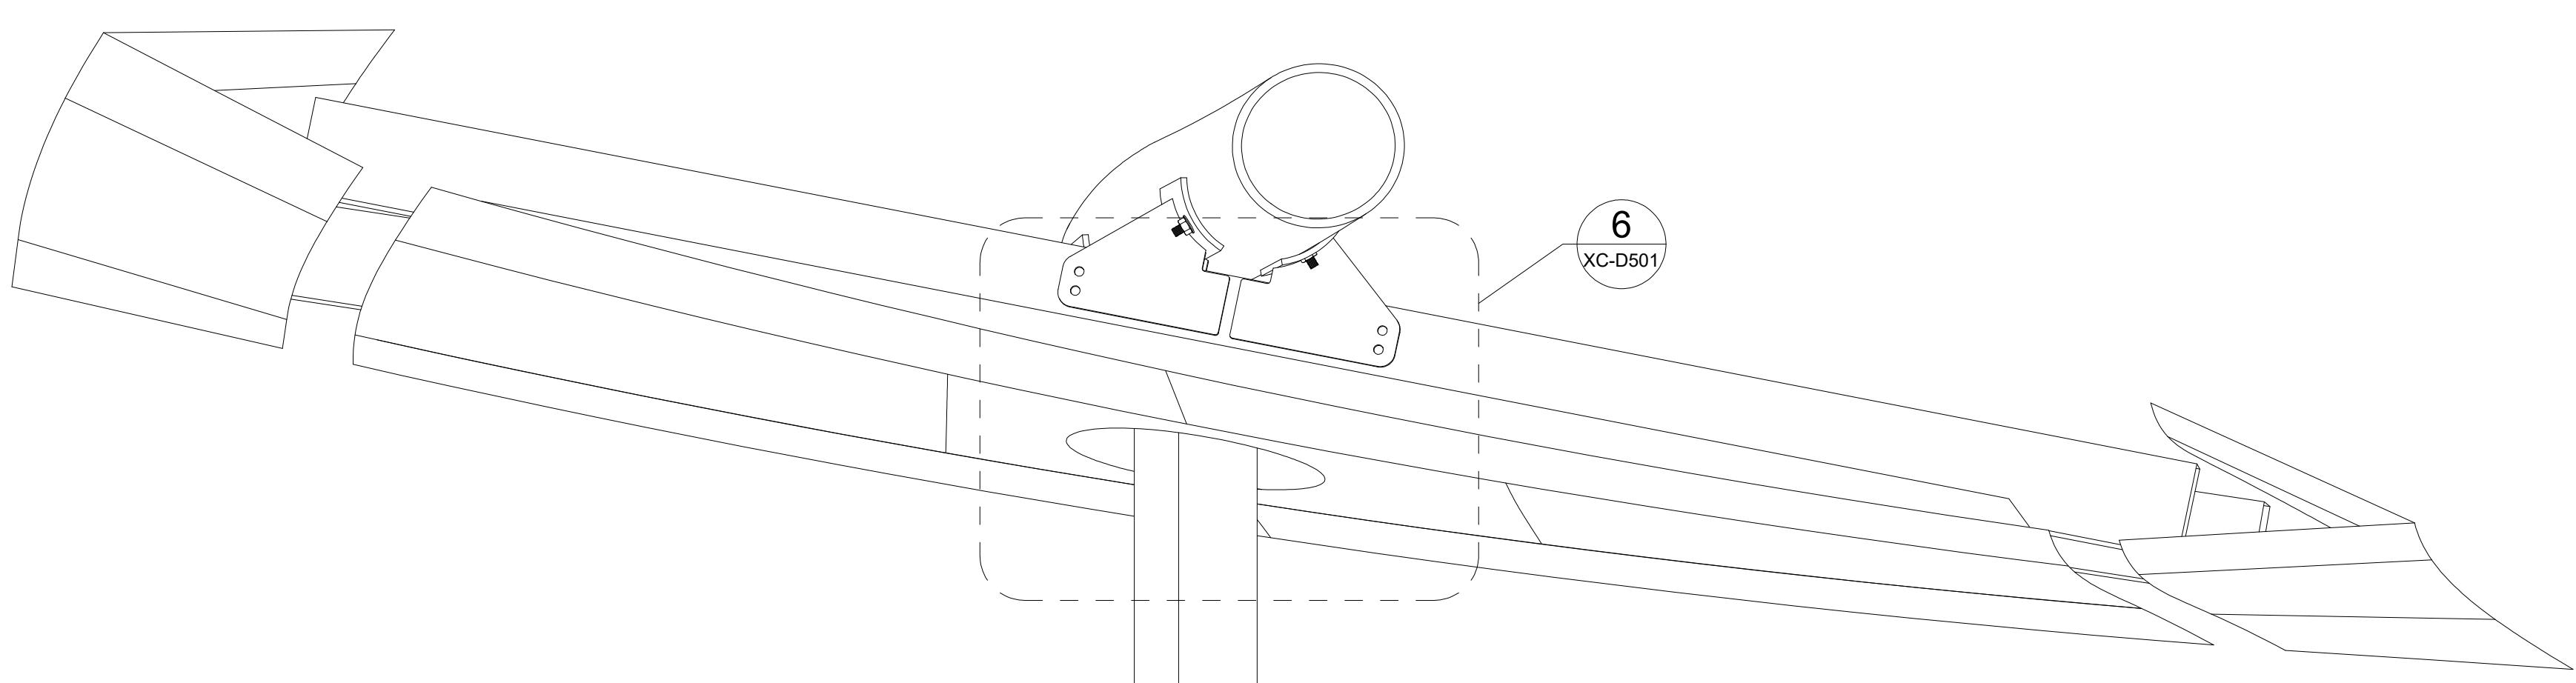


2 CANOPY CROSS SECTION AT COLUMNS

SCALE: 1" = 1'-0"
ZAHNER REF: N/A
ARCH REF: N/A

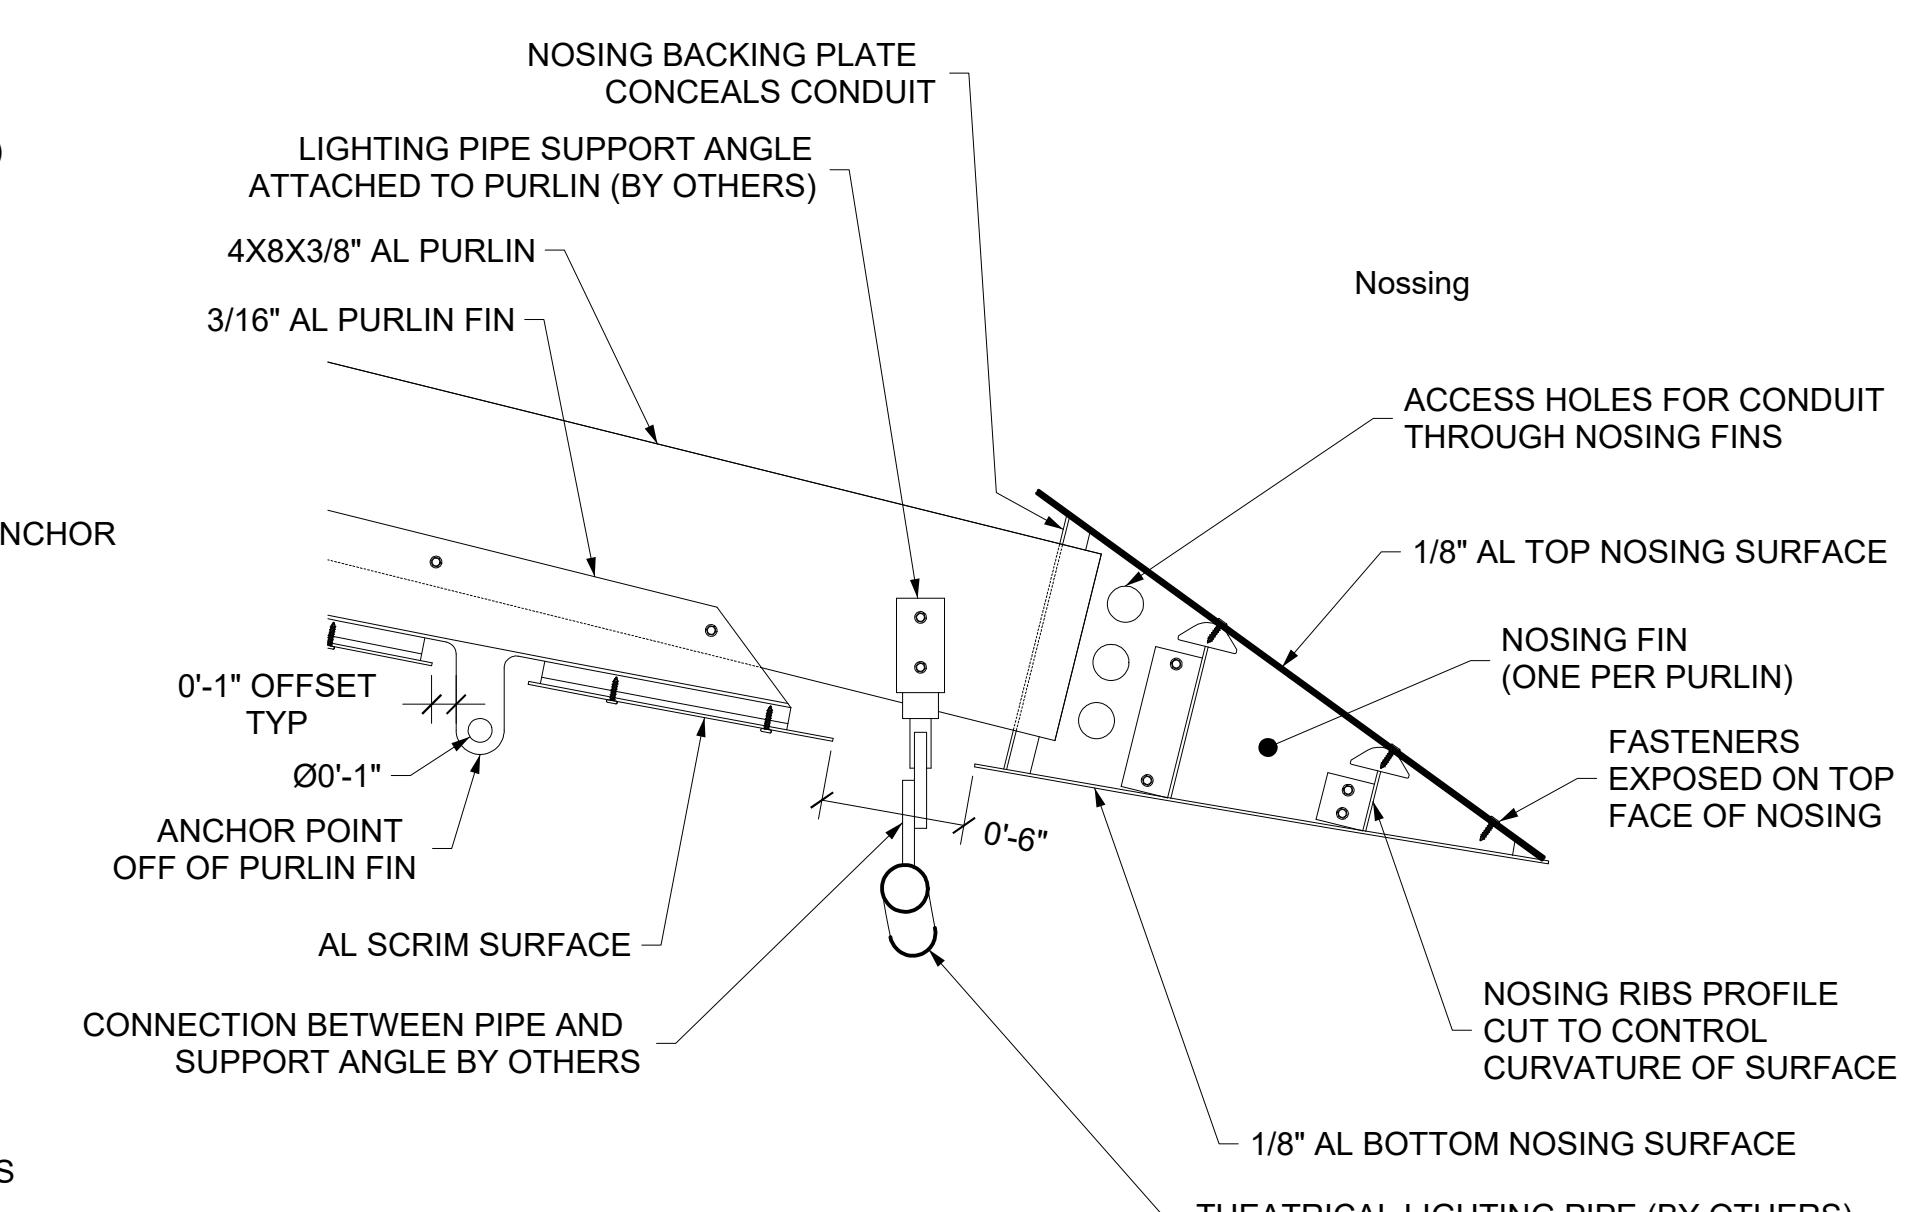

5 INSIDE NOSING DETAIL

SCALE: 1" = 1'-0"
ZAHNER REF: N/A
ARCH REF: N/A

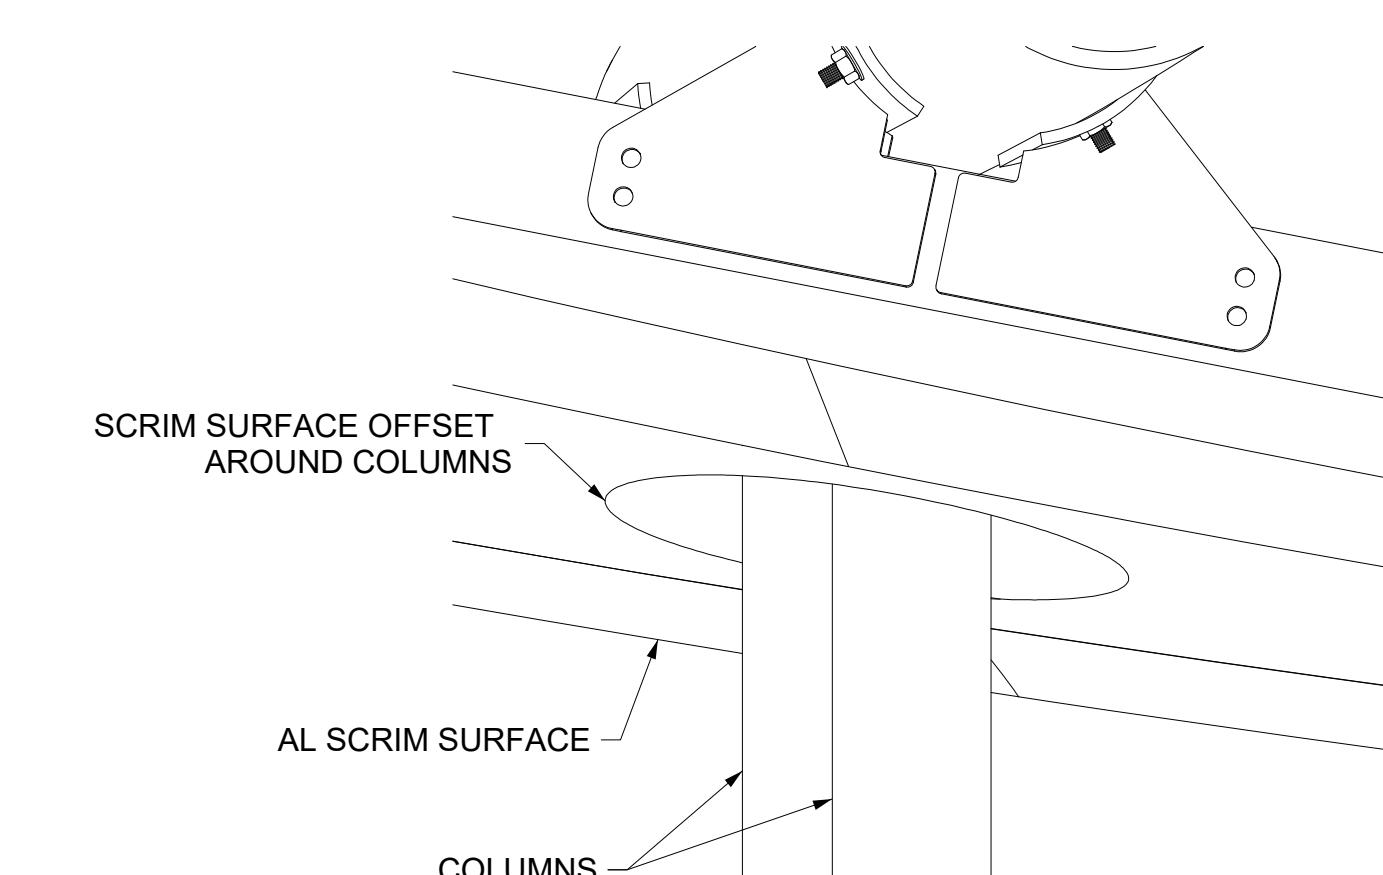

6 SCRIM DETAIL AT COLUMN

SCALE: 1" = 1'-0"
ZAHNER REF: N/A
ARCH REF: N/A


THIS SHEET SCALED
FOR 24X36" BORDER

SET ISSUE DATES		
DATE	ISSUE	
01/20/22 100% DRAWINGS		

REVISIONS		
NO.	DATE	DESCRIPTION




DATE: 01/20/2022	REVISION:	BY:
ENGINEER		
CITY OF SCOTTSDALE CIVIC CENTER PLAZA		
CAPITAL PROJECT MANAGEMENT		
7447 E. INDIAN SCHOOL RD. SCOTTSDALE, ARIZONA 85251		
SHEET TITLE		
360 CANOPY - TYPICAL CANOPY SECTION DETAILS		
PROJECT TITLE		
SCALE	DESIGNED	BID NO.
DRAWN DS	AS-BUILT	COS PROJECT NO. DG04

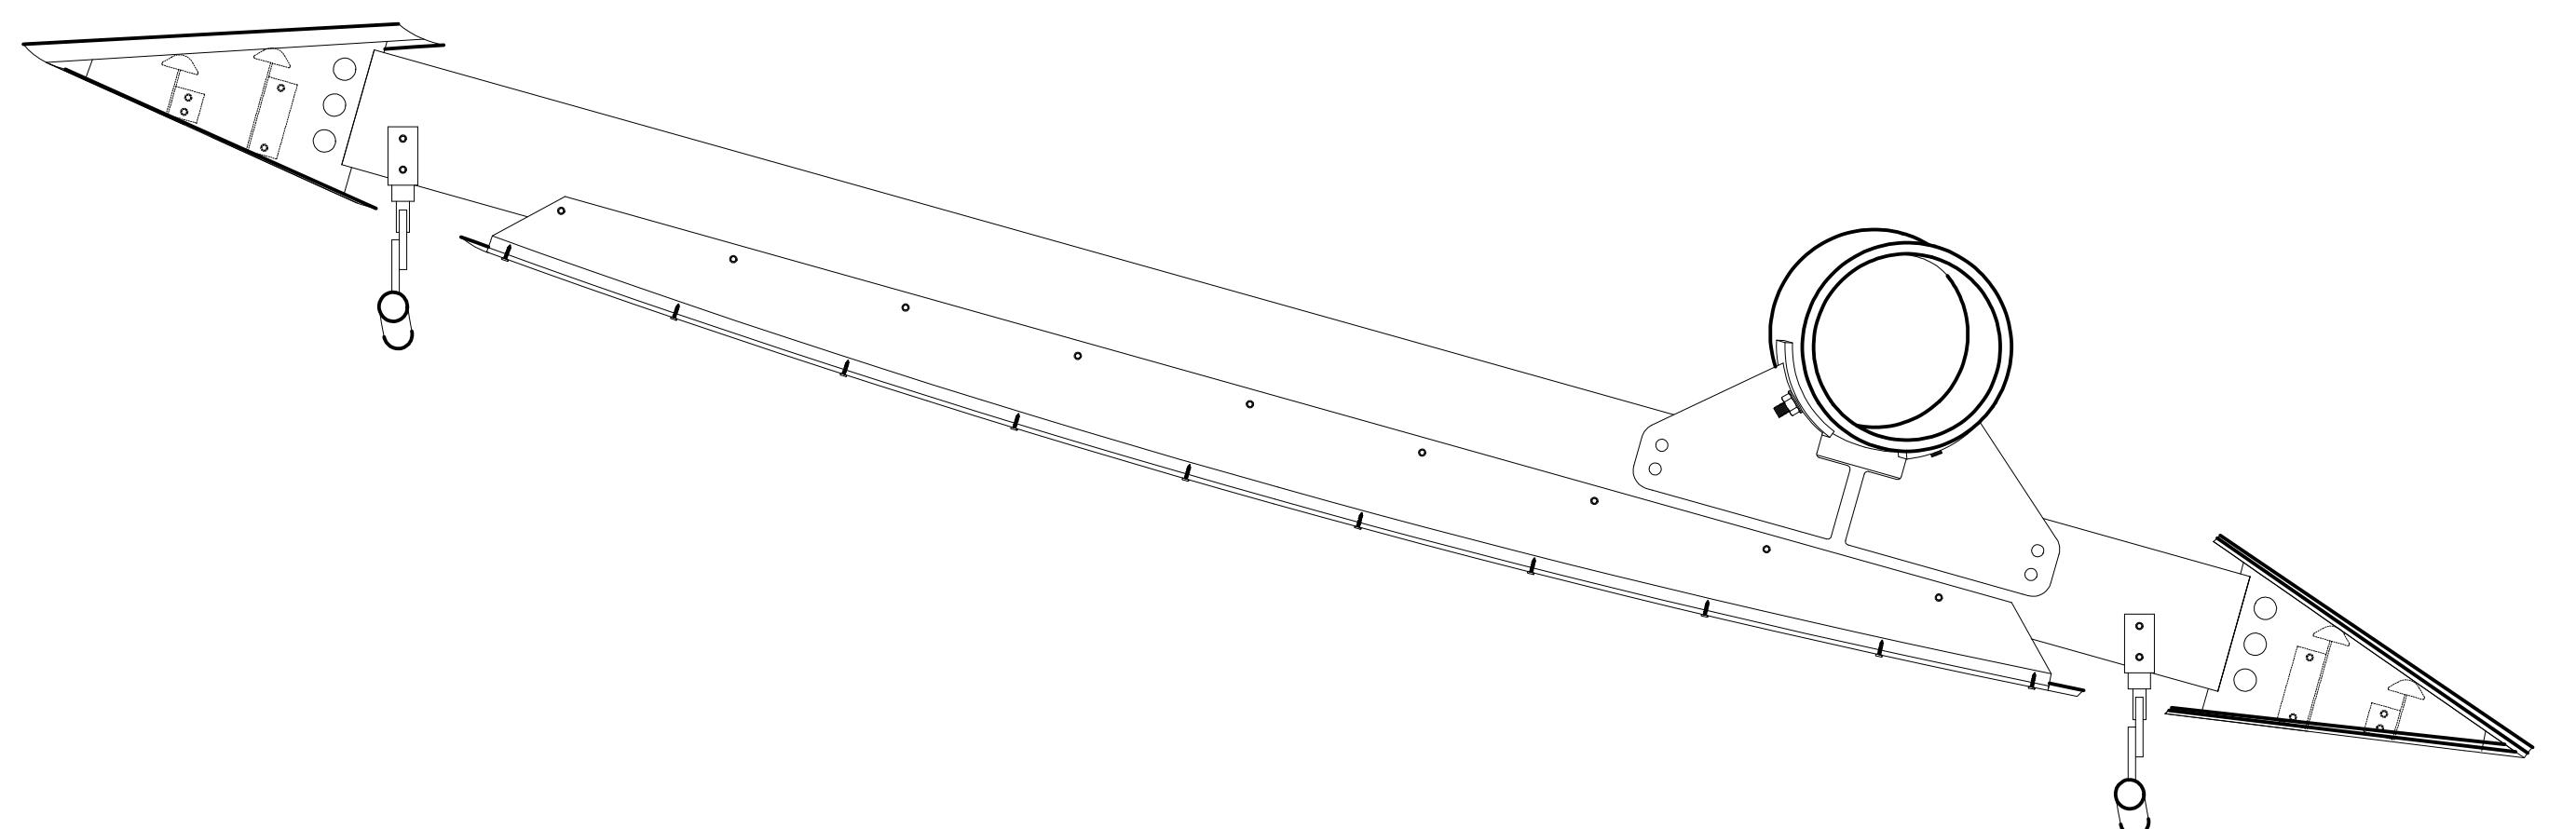

① CANOPY CROSS SECTION AT WALKING PATH


SCALE: 1" = 1'-0"
ZAHNER REF: N/A
ARCH REF: N/A

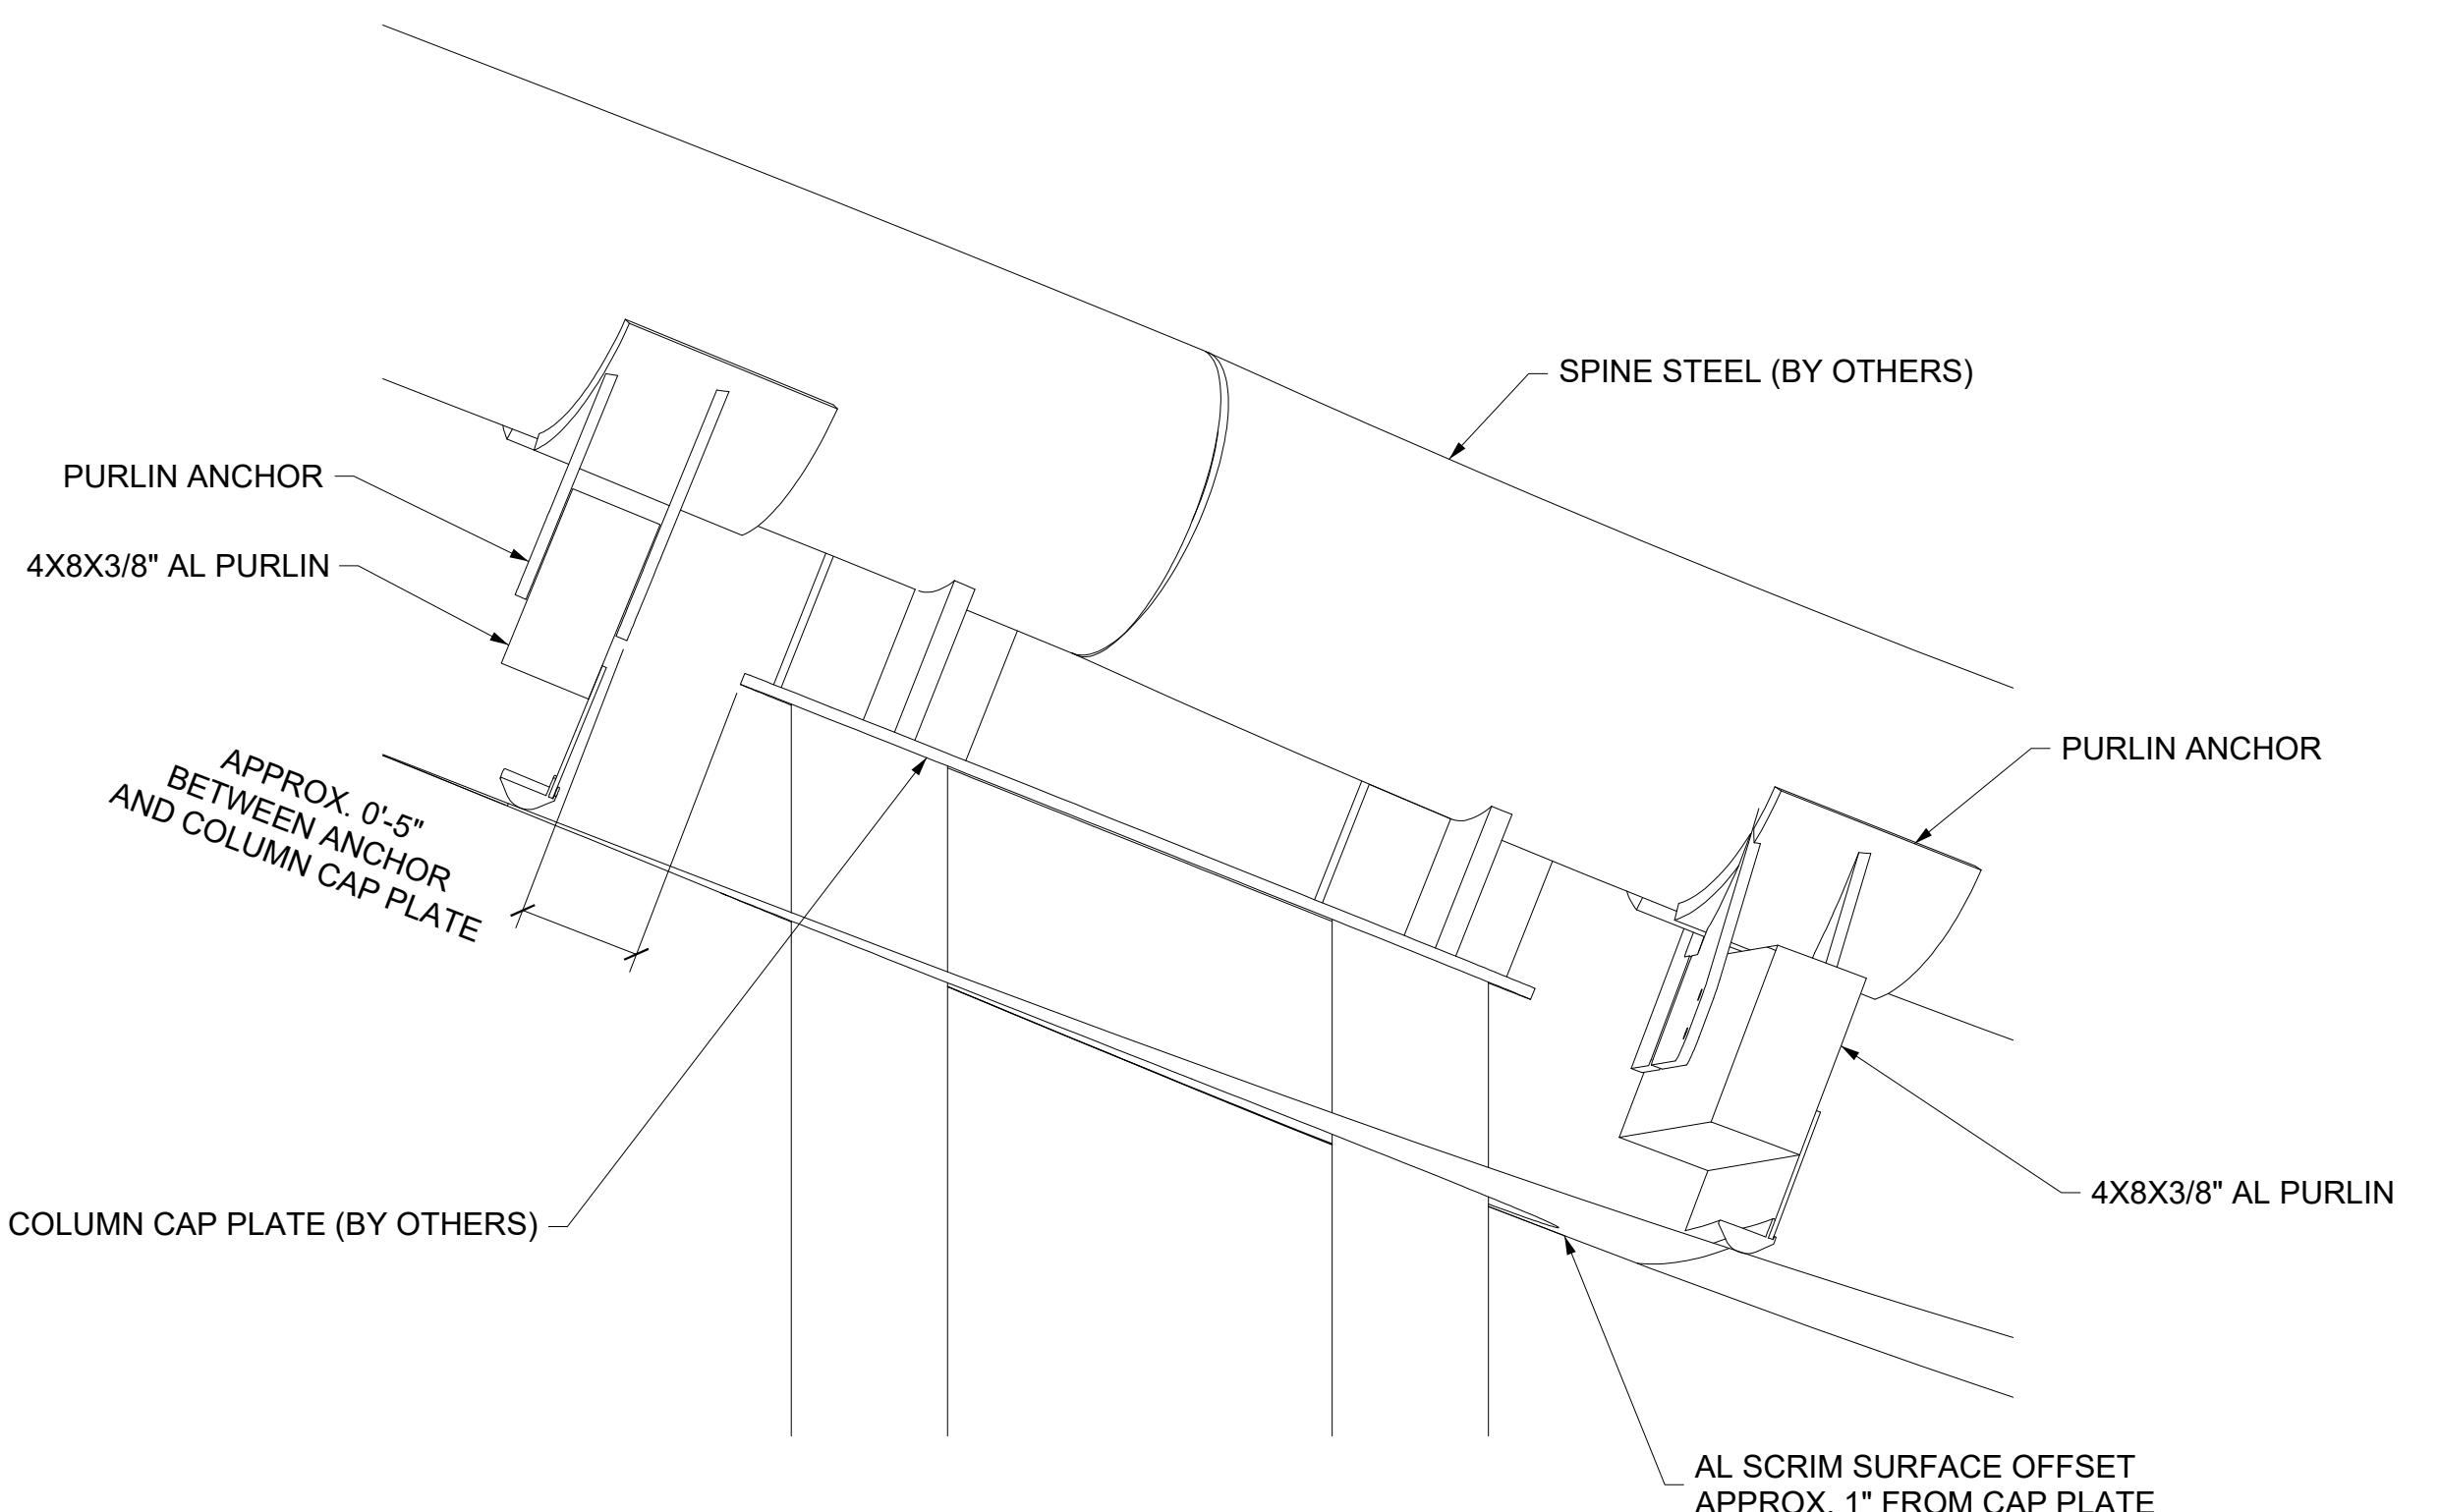

② CANOPY CROSS SECTION AT COLUMNS

SCALE: 1 1/2" = 1'-0"
ZAHNER REF: N/A
ARCH REF: N/A

SET ISSUE DATES		
DATE	ISSUE	
01/20/22 100% DRAWINGS		
REVISIONS		
NO.	DATE	DESCRIPTION

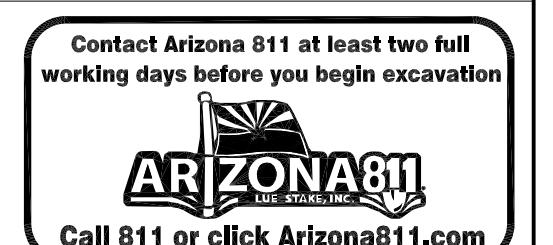

DATE: 01/20/2022		REVISION:	BY:
ENGINEER		PUBLIC WORKS	
		CAPITAL PROJECT MANAGEMENT	
SHEET TITLE		7447 E. INDIAN SCHOOL RD., SCOTTSDALE, ARIZONA 85251	

360 CANOPY - CROSS SECTION AT WALKING PATH

PROJECT TITLE CITY OF SCOTTSDALE
CIVIC CENTER PLAZA

THIS SHEET SCALED FOR 24X36" BORDER	SCALE	DESIGNED	BID NO.	XC-D502
	DRAWN DS	AS-BUILT	COS PROJECT NO. DG04	