


Z100

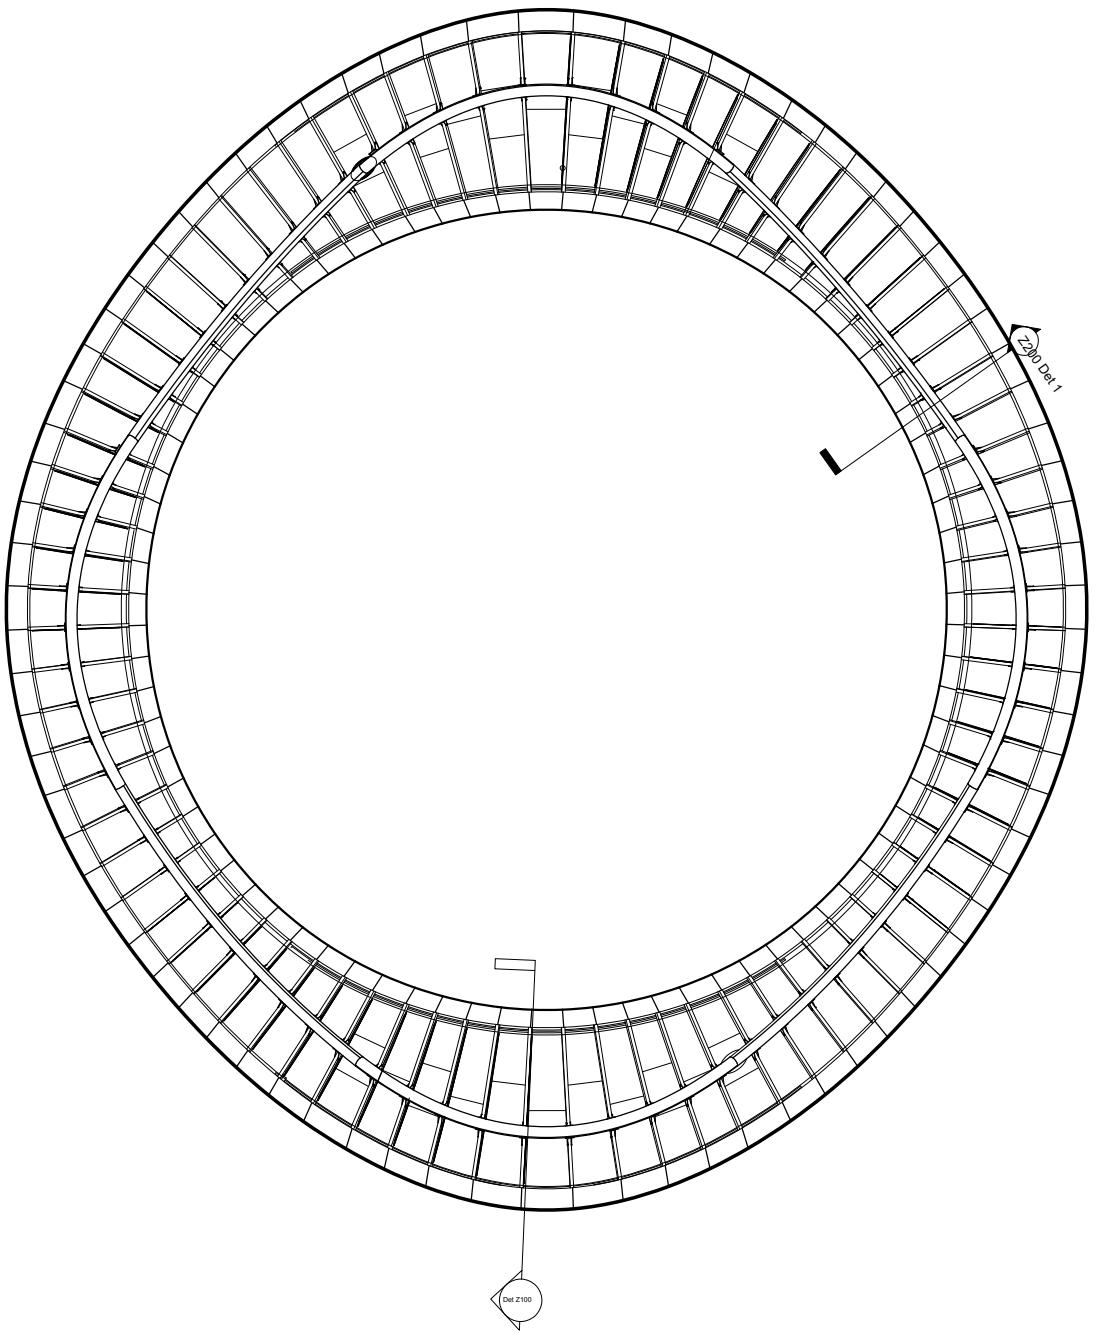

test hyperlink




PROPRIETARY NOTICE
This drawing sheet and contents herein are the property of A.Zahner Company. Use of this drawing, contents or design for purposes other than estimating, drawing preparation and/or manufacturing for A.Zahner Company shall be cause for legal recourse by A.Zahner Company.

NOTES: UNLESS OTHERWISE SPECIFIED
ALL DIMENSIONS ARE IN INCHES
ALL DIMENSIONS ARE O.D.
ALL BRAKES ARE CONSIDERED TO BE 90°
FINISH FACE IS UP

REV.	DATE	DR. BY:	CHECKED BY:	DESCRIPTION	ARCHITECT:	TITLE:	ITEM #: XXXXXX	DS:
0	1/1/1111	XYZ			ARCHITECT:	PROJECT NUMBER: ThisNumber	SHEET NUMBER:	
					CONTRACTOR:	PROJECT NAME : ThisName		
						MO #: xxxxx	PG: 1	OF 4

IF THIS DRAWING IS NOT 11" X 17" THEN IT HAS BEEN ALTERED FROM ITS ORIGINAL SIZE. THIS LINE SHOULD EQUAL 1"

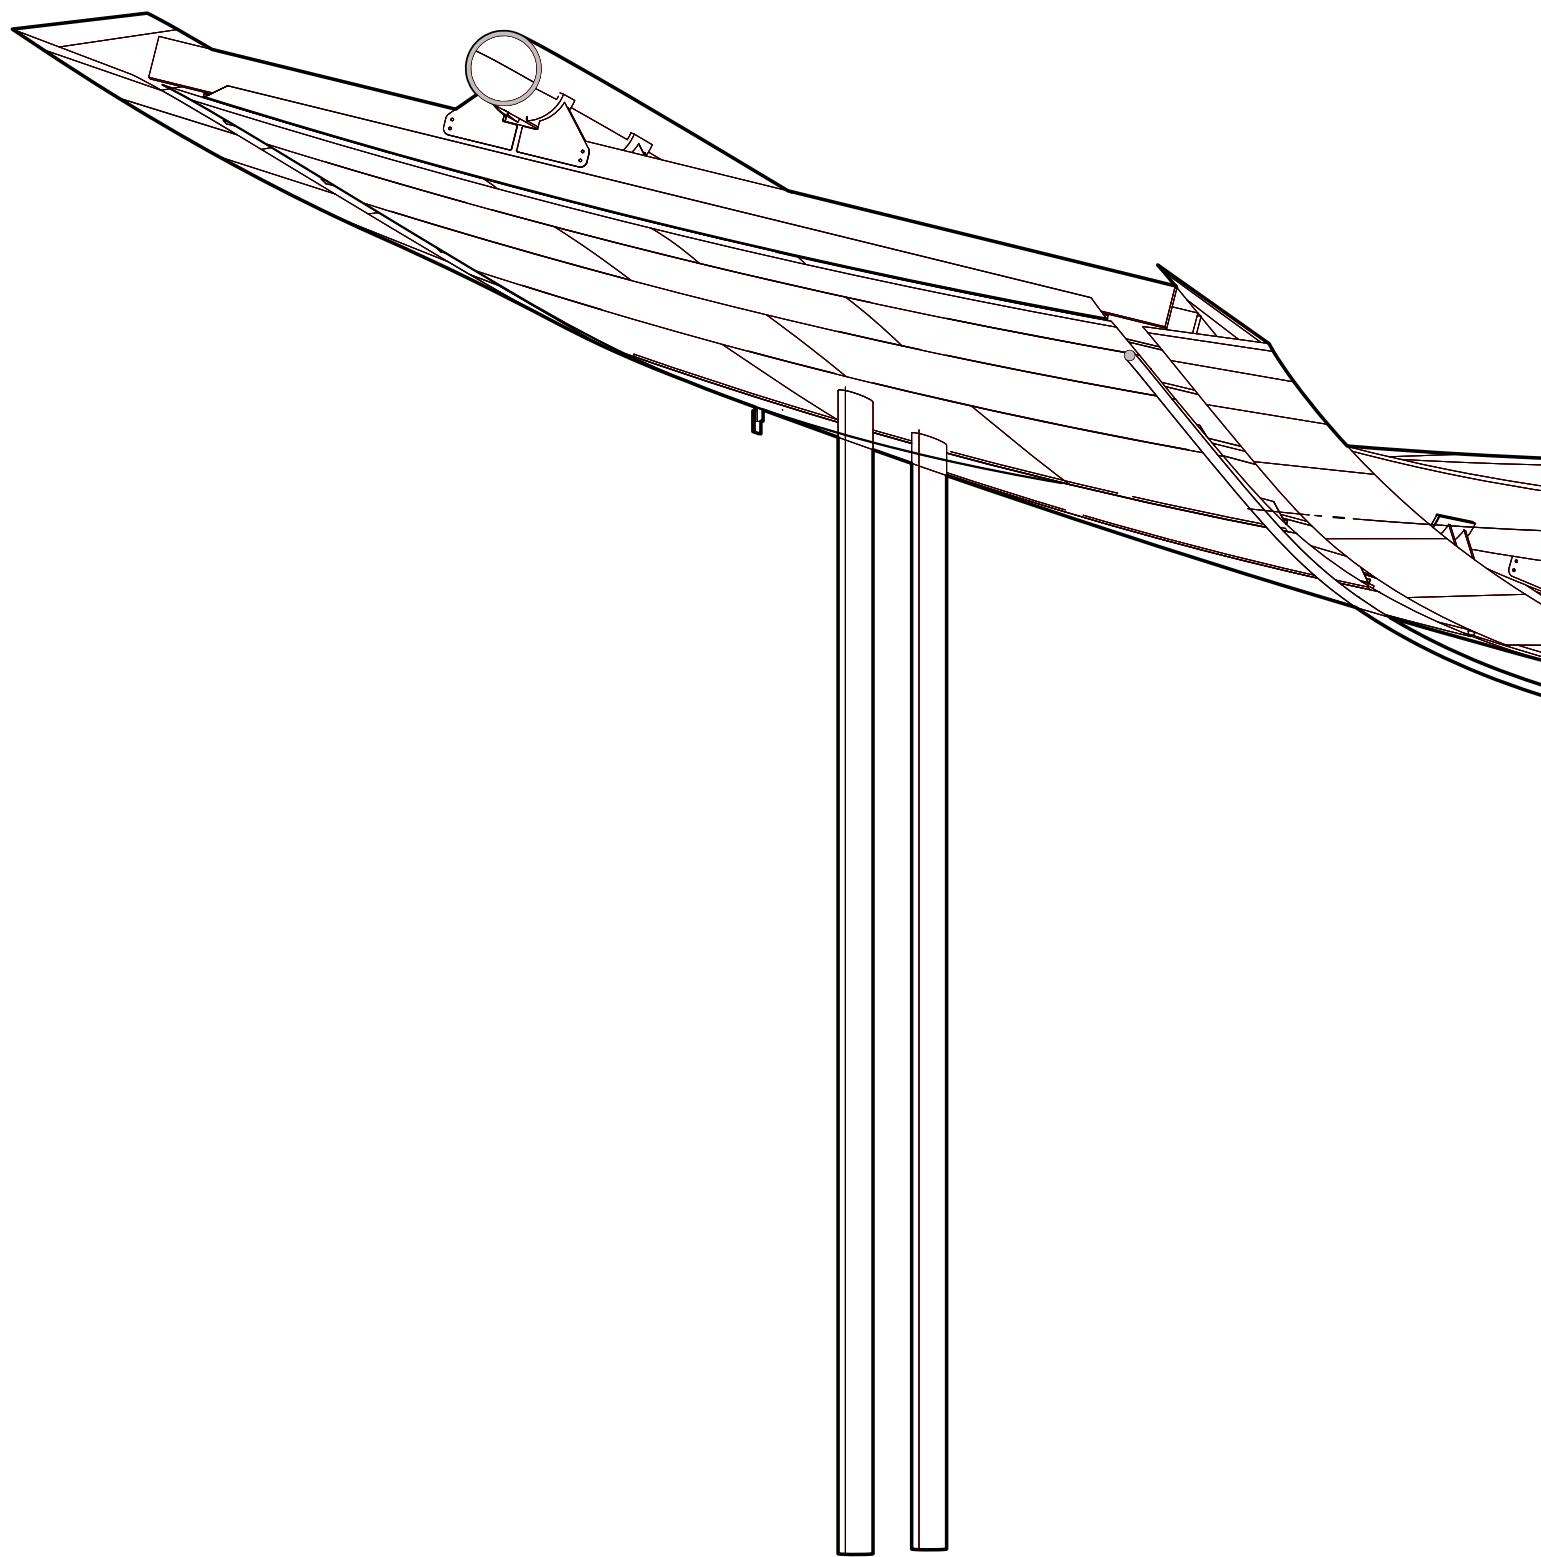

ZAHNER
ARCHITECTURAL METAL
1400 EAST NINTH STREET
KANSAS CITY, MO. 64106
TEL: (816) 474-8882
FAX: (816) 474-7994
WWW.AZAHNER.COM




PROPRIETARY NOTICE
This drawing sheet and contents herein are the property of A.Zahner Company. Use of this drawing, contents or design for purposes other than estimating, drawing preparation and/or manufacturing for A.Zahner Company shall be cause for legal recourse by A.Zahner Company.

NOTES: UNLESS OTHERWISE SPECIFIED
ALL DIMENSIONS ARE IN INCHES
ALL DIMENSIONS ARE O.D.
ALL BRAKES ARE CONSIDERED TO BE 90°
FINISH FACE IS UP

REV.	DATE	DR. BY:	CHECKED BY:	DESCRIPTION	ARCHITECT:	TITLE:	ITEM #: XXXXXX	DS:
0	1/1/1111	XYZ			ARCHITECT:		PROJECT NUMBER: ThisNumber	SHEET NUMBER:
						CONTRACTOR:	DESCRIPTION:	PROJECT NAME : ThisName
							MO #: xxxxxx	PG: 2 OF 4

Z200

test hyperlink

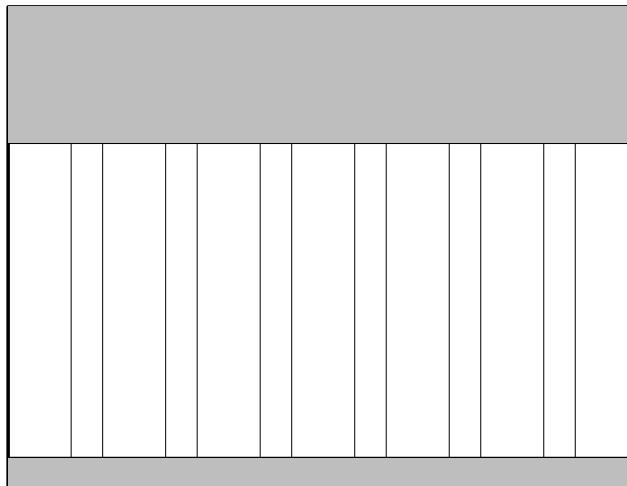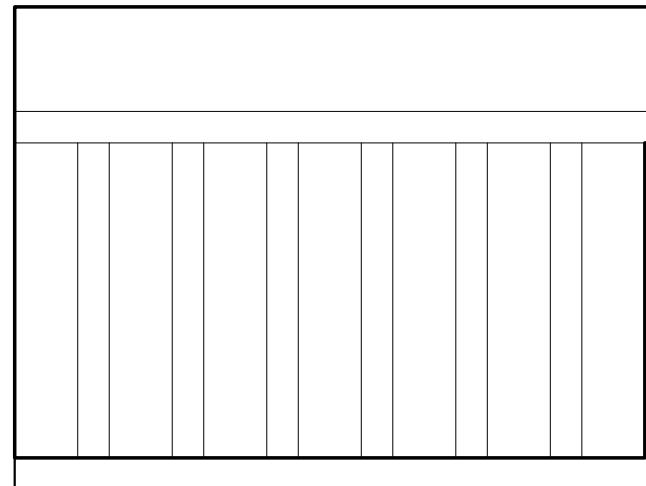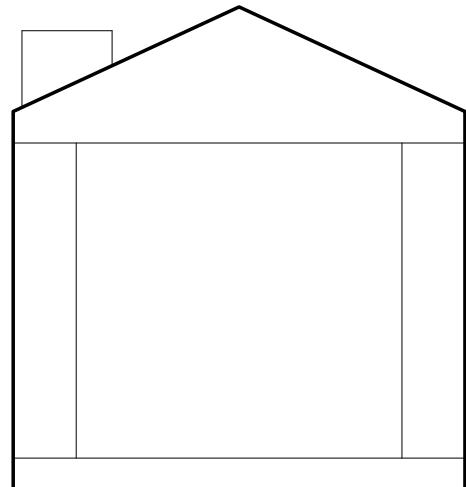

PROPRIETARY NOTICE


This drawing sheet and contents herein are the property of A.Zahner Company. Use of this drawing, contents or design for purposes other than estimating, drawing preparation and/or manufacturing for A.Zahner Company shall be cause for legal recourse by A.Zahner Company.

NOTES: UNLESS OTHERWISE SPECIFIED
ALL DIMENSIONS ARE IN INCHES
ALL DIMENSIONS ARE O.D.
ALL BRAKES ARE CONSIDERED TO BE 90°
FINISH FACE IS UP

REV.	DATE	DR. BY:	CHECKED BY:	DESCRIPTION	ARCHITECT:	TITLE:	ITEM #: XXXXX	DS:
0	1/1/1111	XYZ			ARCHITECT:	PROJECT NUMBER: ThisNumber	SHEET NUMBER:	
					CONTRACTOR:	DESCRIPTION:	PROJECT NAME : ThisName	
							MO #: xxxxx	
								PG: 3 OF 4

IF THIS DRAWING IS NOT 11" X 17" THEN IT HAS BEEN ALTERED FROM ITS ORIGINAL SIZE. THIS LINE SHOULD EQUAL 1"

Z300

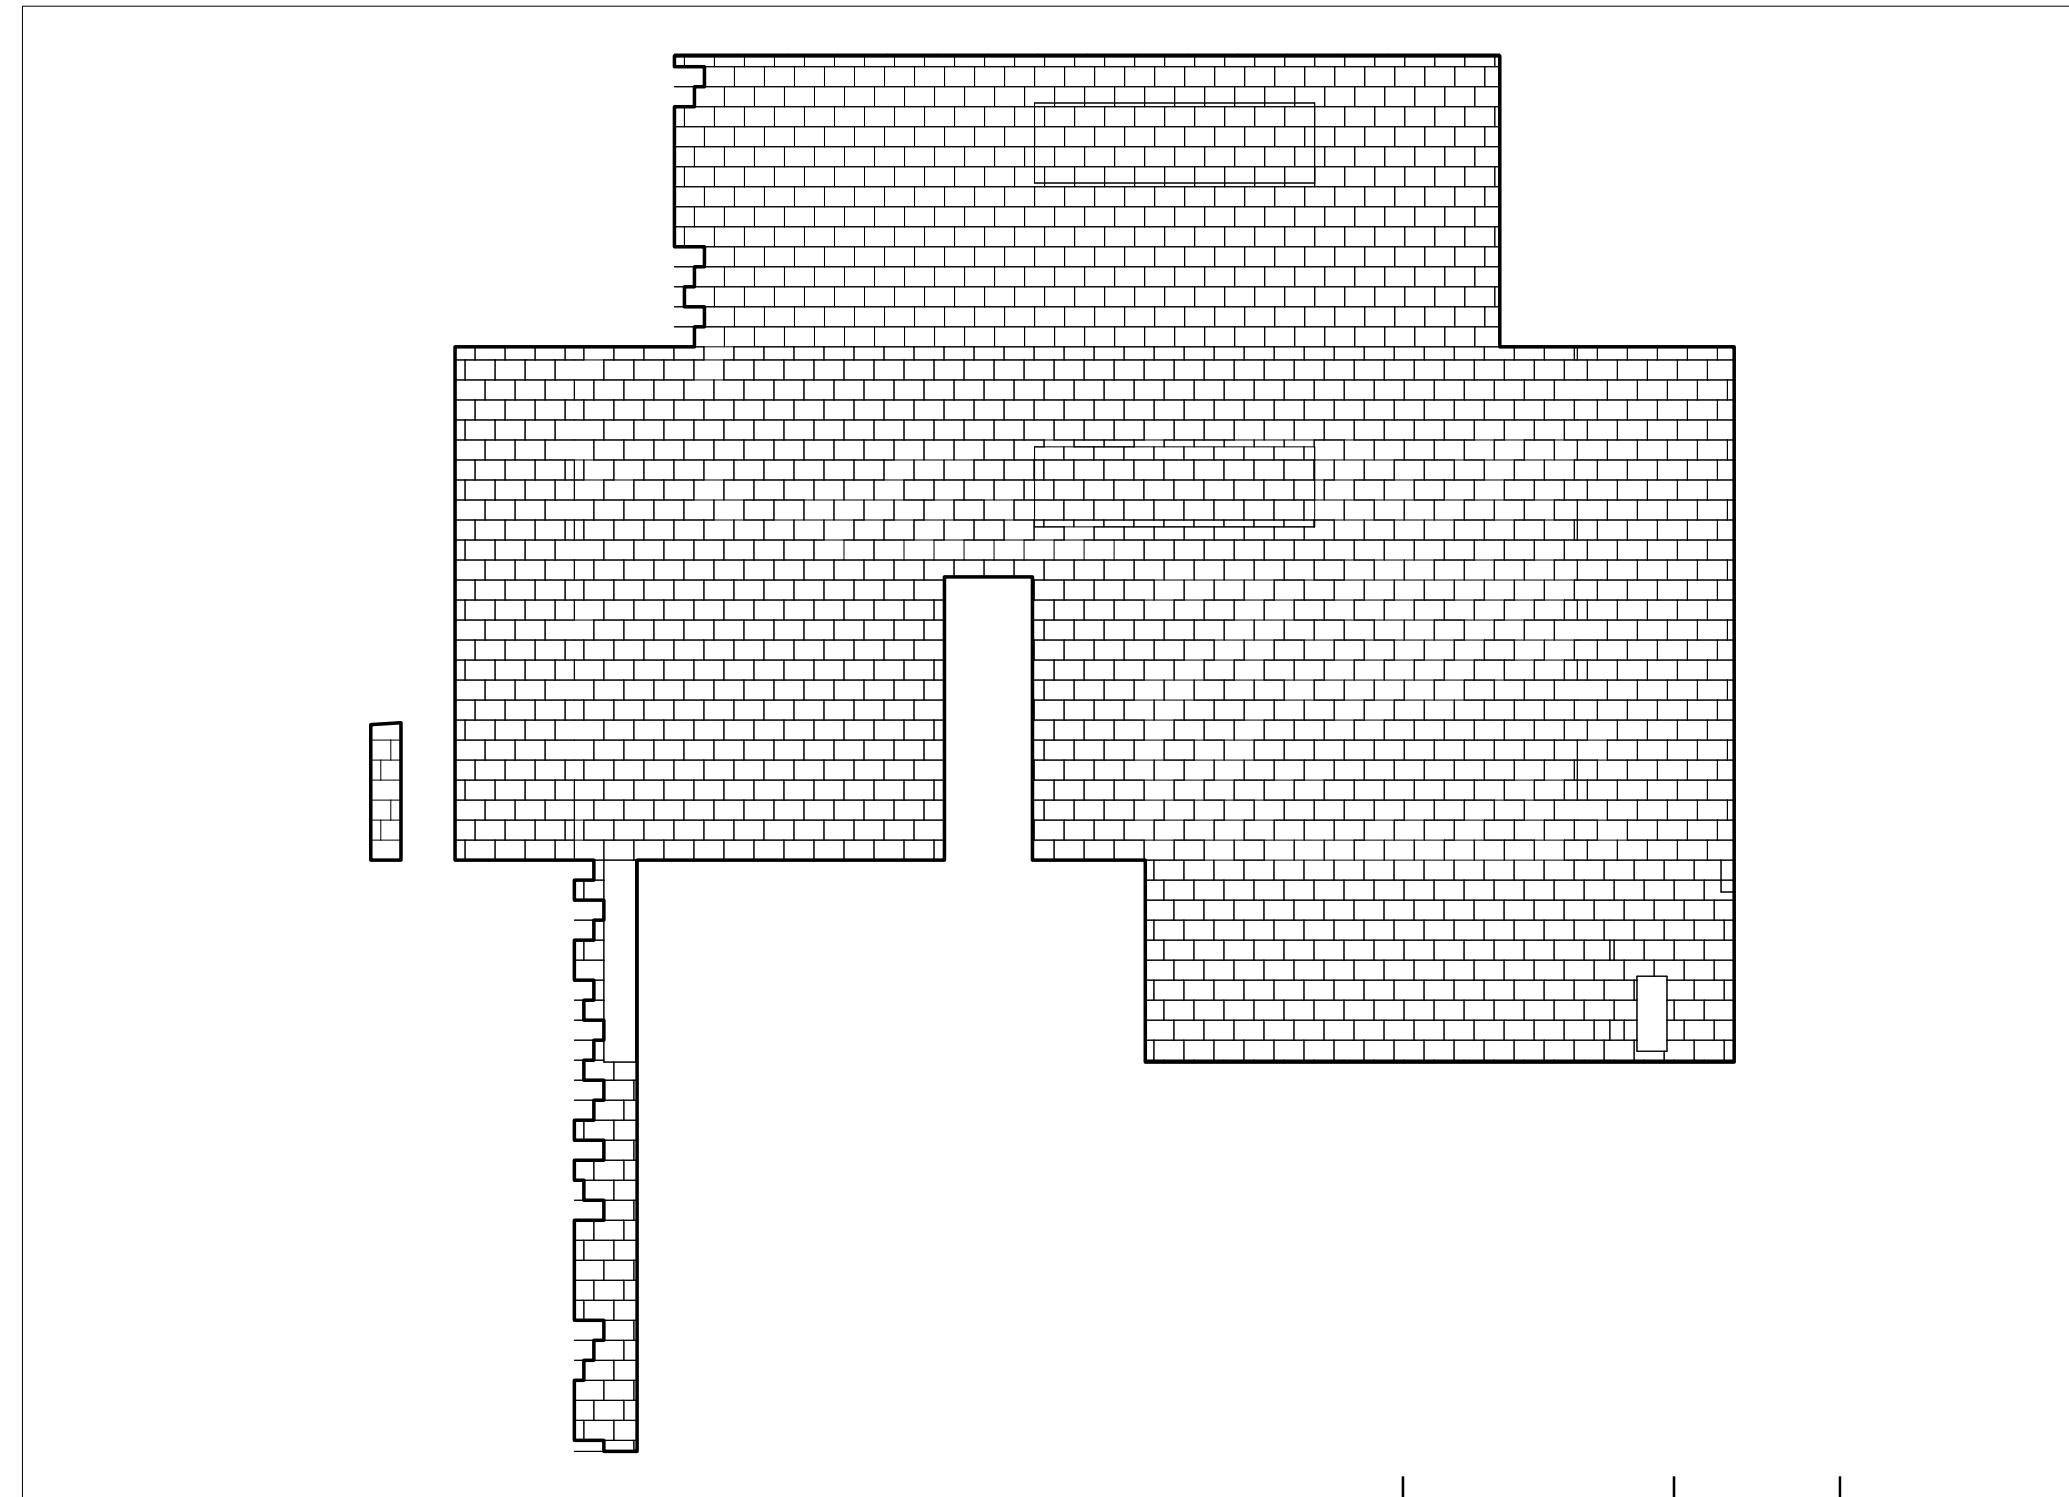

test hyperlink

ZAHNER
ARCHITECTURAL METAL
1400 EAST NINTH STREET
KANSAS CITY, MO. 64106
TEL: (816) 474-8882
FAX: (816) 474-7994
WWW.AZAHNER.COM

PROPRIETARY NOTICE

This drawing sheet and contents herein are the property of A.Zahner Company. Use of this drawing, contents or design for purposes other than estimating, drawing preparation and/or manufacturing for A.Zahner Company shall be cause for legal recourse by A.Zahner Company.

NOTES: UNLESS OTHERWISE SPECIFIED
ALL DIMENSIONS ARE IN INCHES
ALL DIMENSIONS ARE O.D.
ALL BRAKES ARE CONSIDERED TO BE 90°
FINISH FACE IS UP

REV.	DATE	DR. BY:	CHECKED BY:	DESCRIPTION	ARCHITECT:	TITLE:	ITEM #: XXXXX	DS:
0	1/1/1111	XYZ			ARCHITECT:	PROJECT NUMBER: ThisNumber	SHEET NUMBER:	
					CONTRACTOR:	PROJECT NAME : ThisName		
						DESCRIPTION:	MO #: xxxxx	PG: 4 OF 4

IF THIS DRAWING IS NOT 11" X 17" THEN IT HAS BEEN ALTERED FROM ITS ORIGINAL SIZE. THIS LINE SHOULD EQUAL 1"